


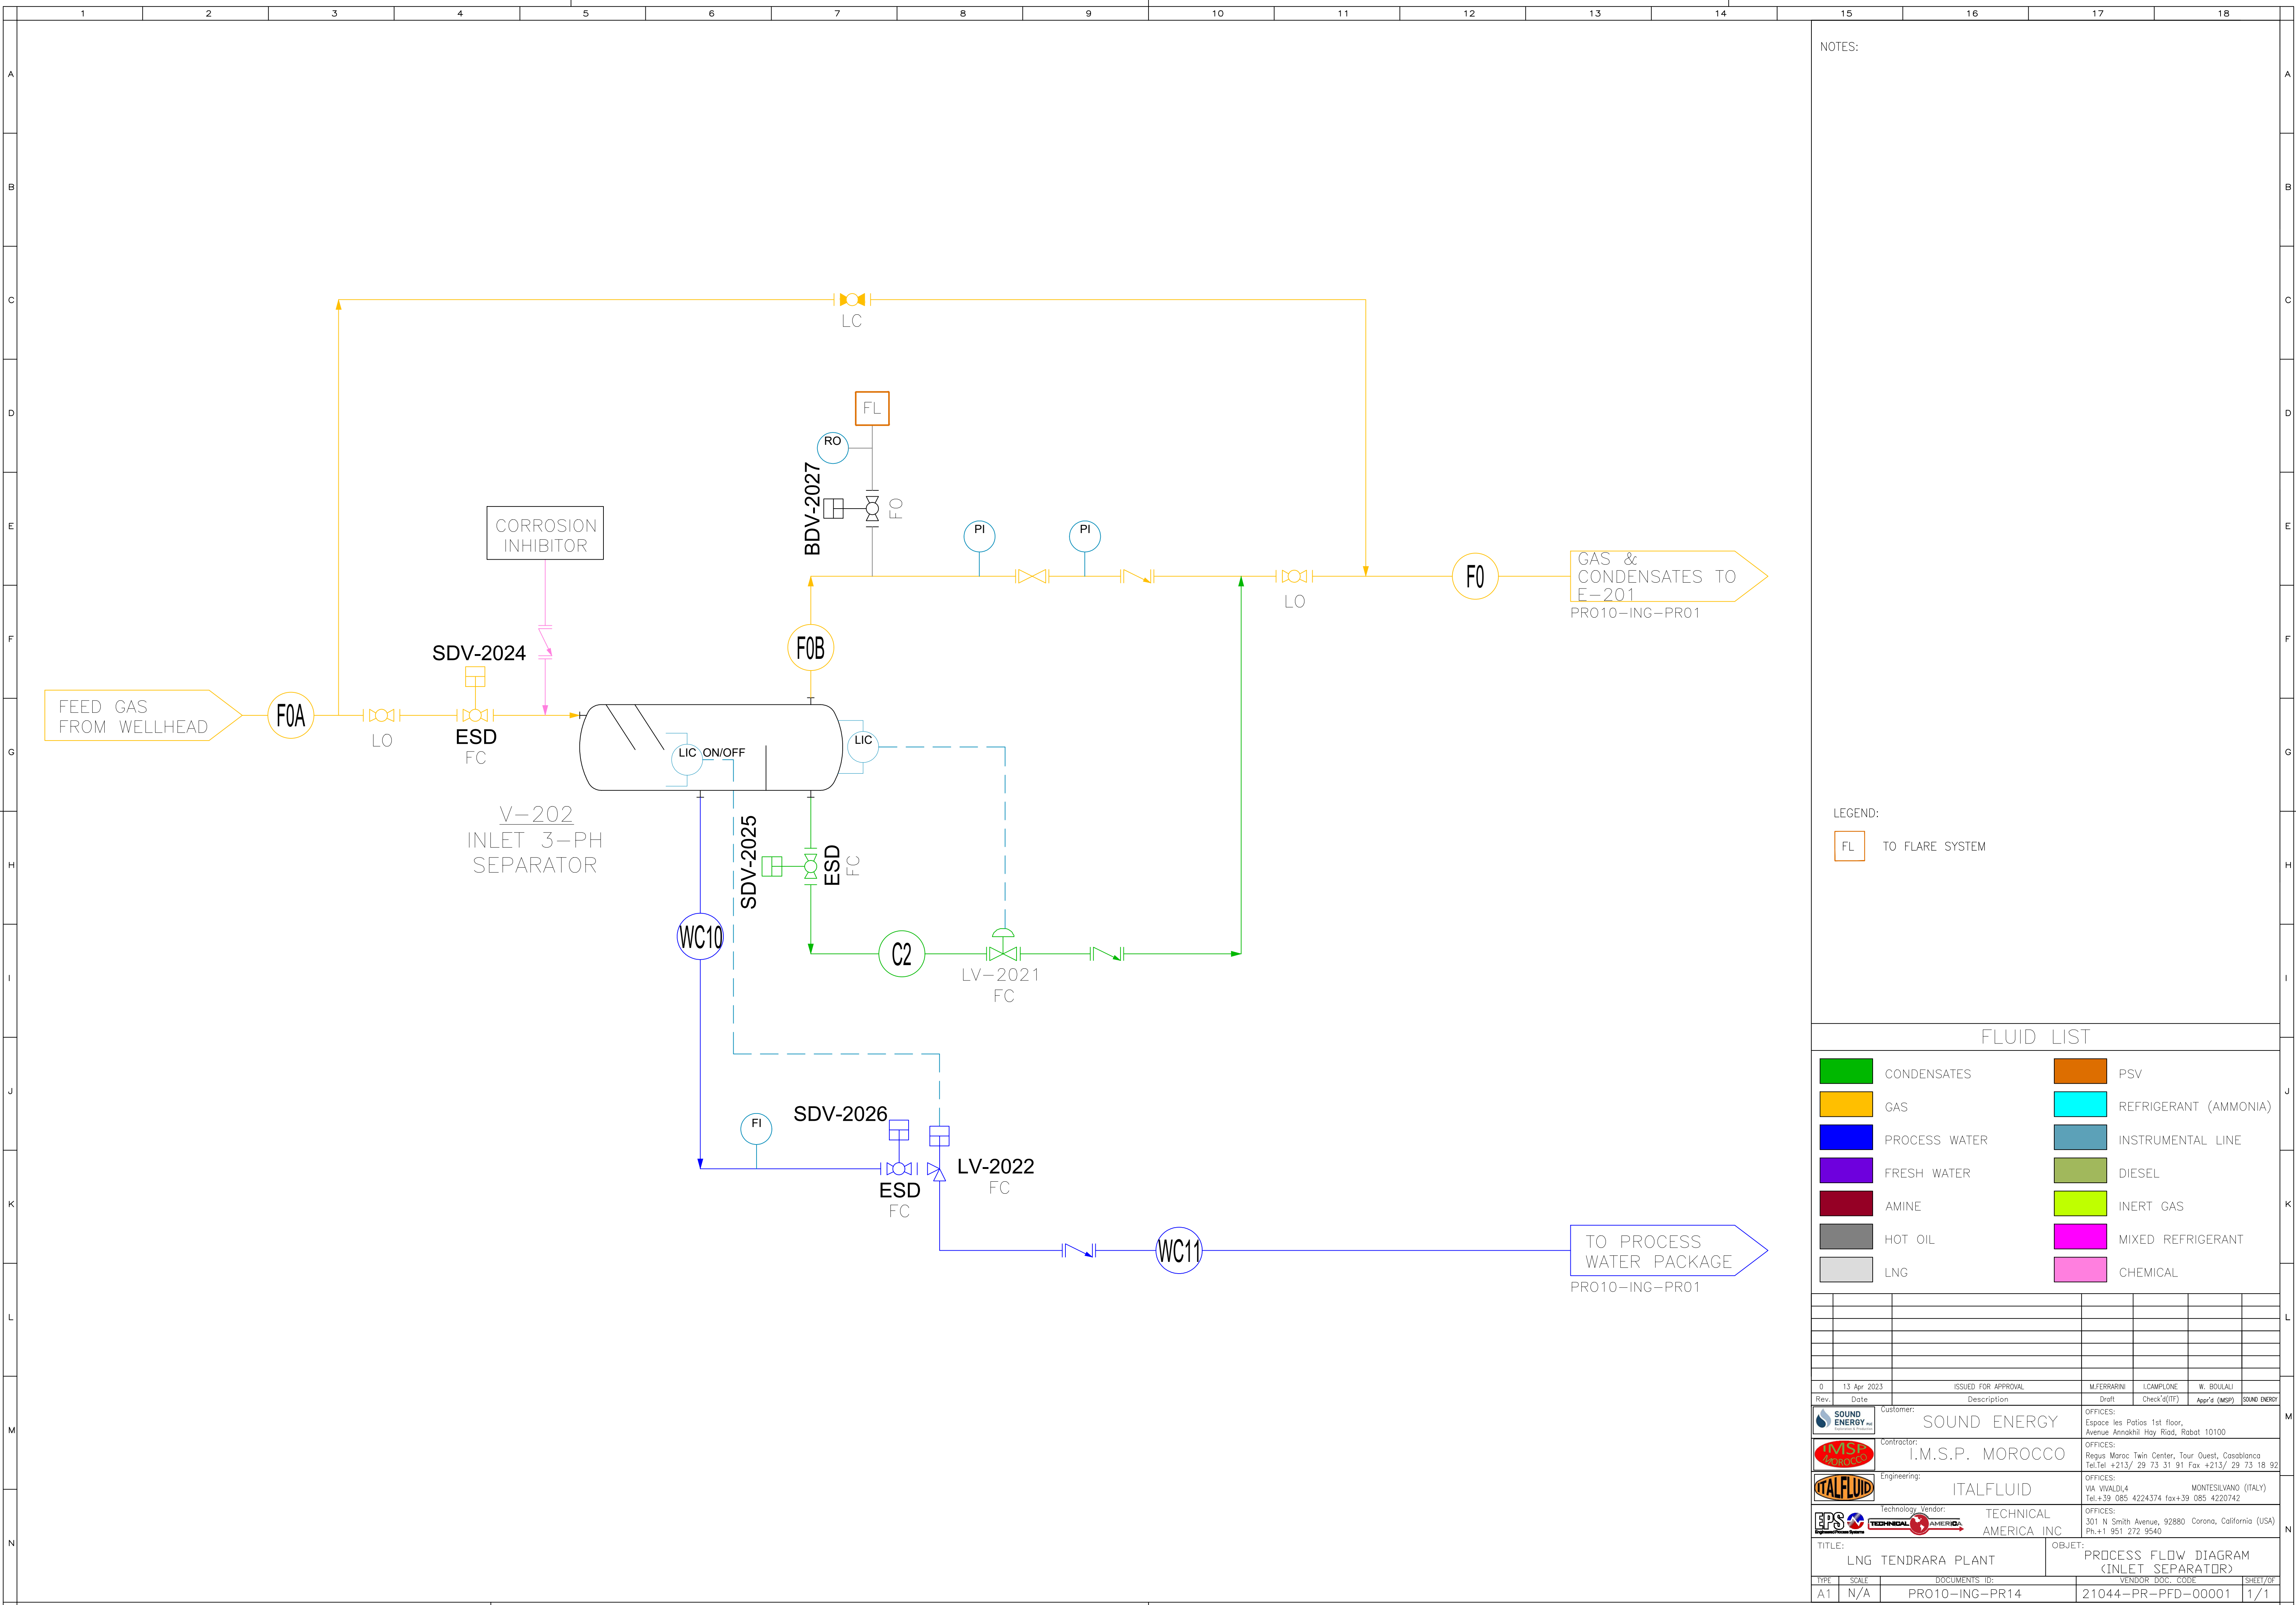

NOTES:


LEGEND:

FL TO FLARE SYSTEM


FLUID LIST

CONDENSATES	PSV
GAS	REFRIGERANT (AMMONIA)
PROCESS WATER	INSTRUMENTAL LINE
FRESH WATER	DIESEL
AMINE	INERT GAS
HOT OIL	MIXED REFRIGERANT
LNG	CHEMICAL

0	13 Apr 2023	ISSUED FOR APPROVAL	M.FERRARINI	L.CAMPIONE	W. BOULALI	
Rev.	Date	Description	Draft	Check'd(IFT)	App'd (MSP)	SOUND ENERGY
		Customer:	SOUND ENERGY			
		Contractor:	I.M.S.P. MOROCCO			
		Engineering:	ITALFLUID			
		Technology Vendor:	TECHNICAL AMERICA INC			
		Offices:	MONTESILVANO (ITALY) Tel:+39 085 4224374 fax+39 085 4220742			
		Offices:	301 N Smith Avenue, 92880 Corona, California (USA) Ph:+1 951 272 9540			
TITLE:			OBJET:			
LNG TENDRARA PLANT			PROCESS FLOW DIAGRAM (INLET SEPARATOR)			
TYPE	SCALE	DOCUMENTS ID:	VENDOR DOC. CODE		SHEET/OF	
A1	N/A	PRO10-ING-PR14	21044-PR-PFD-00001		1/1	

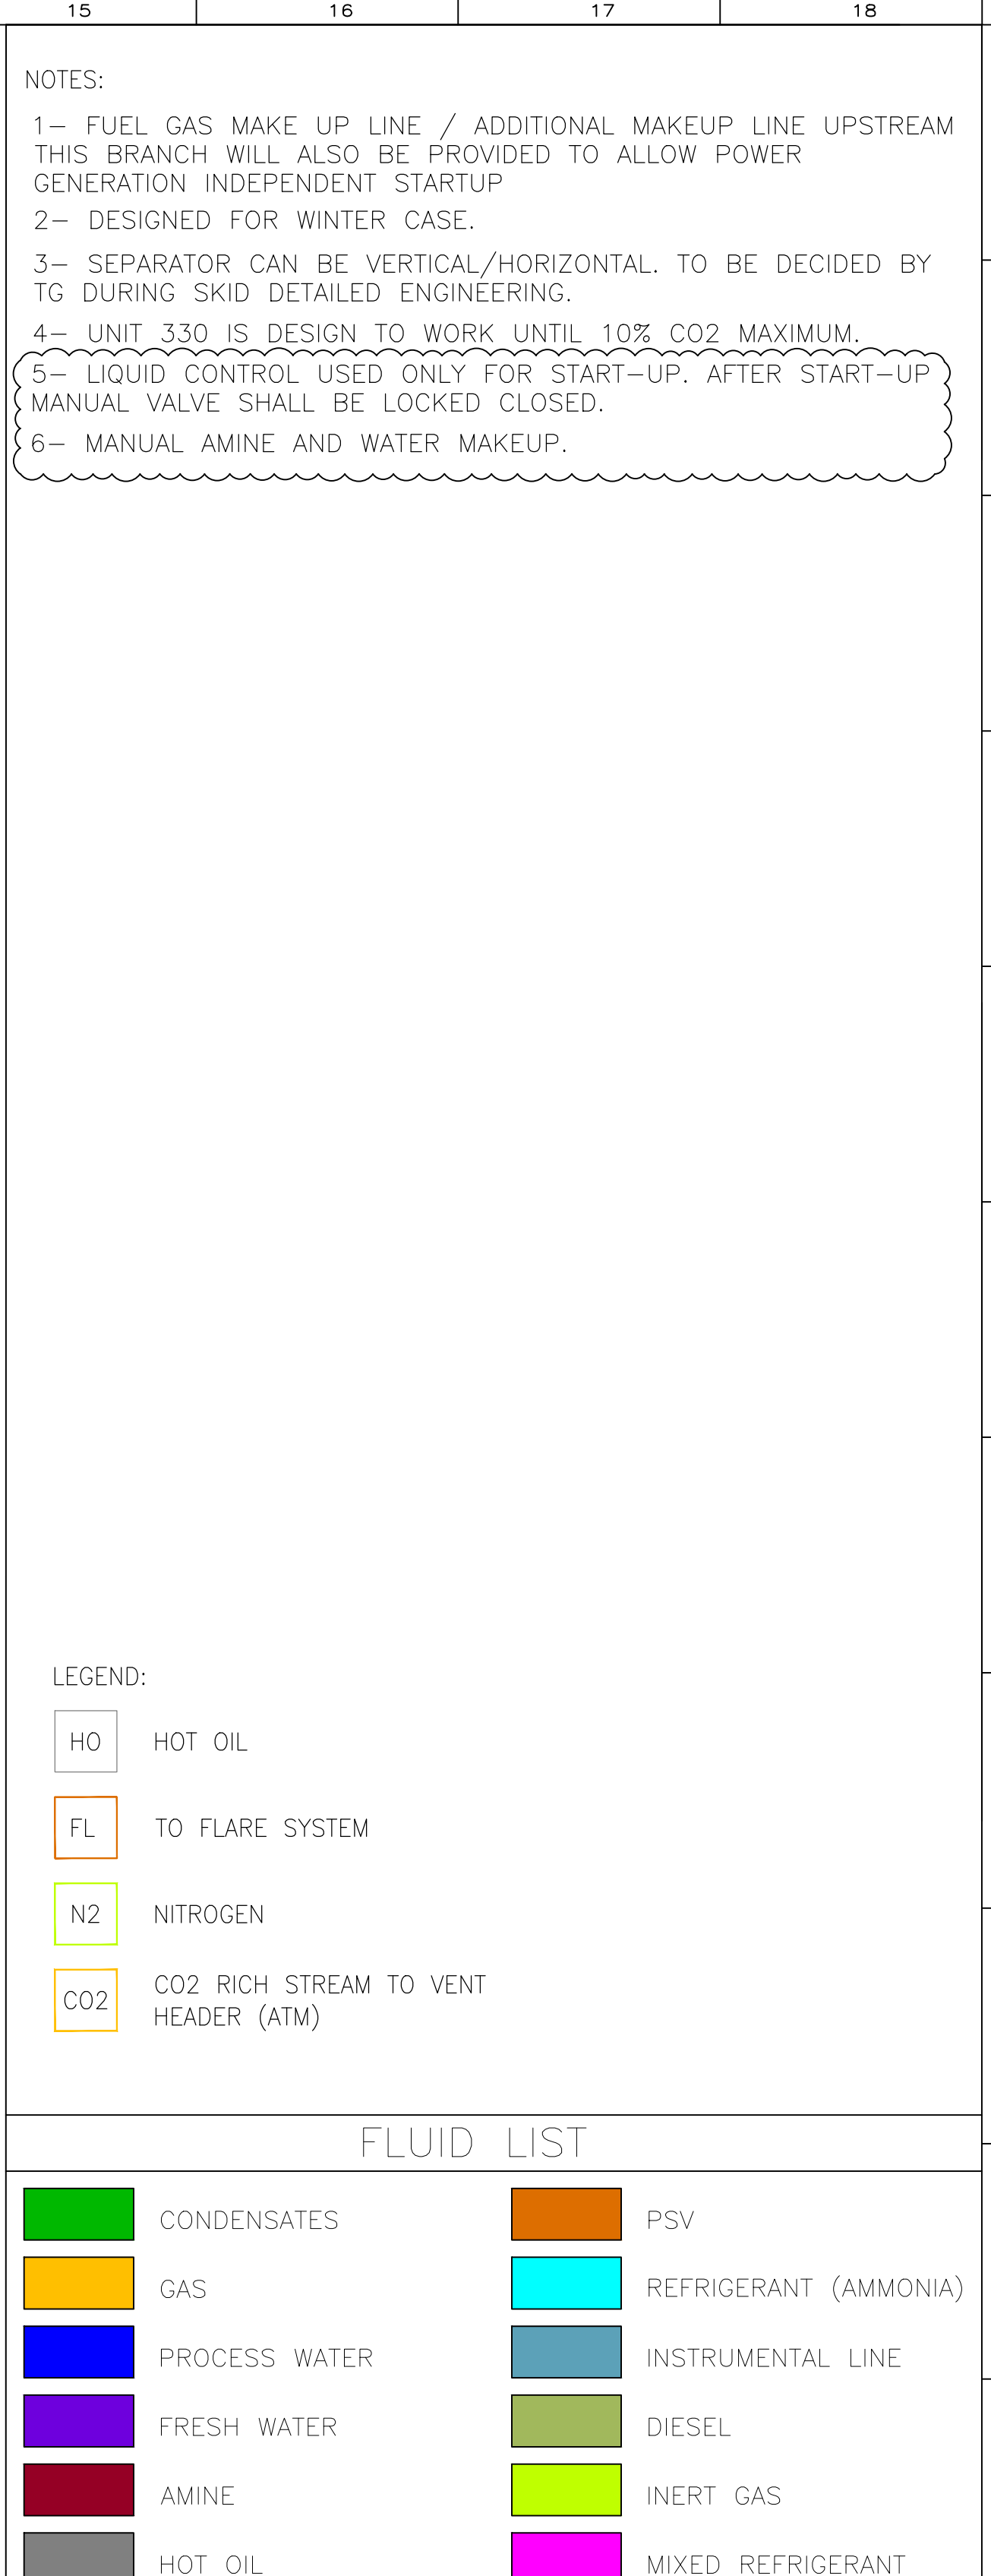

Documento di proprietà aziendale. La Società tutela i propri diritti a termine di legge.	This document is Company property. The Company lawfully reserves all rights.	
--	--	--

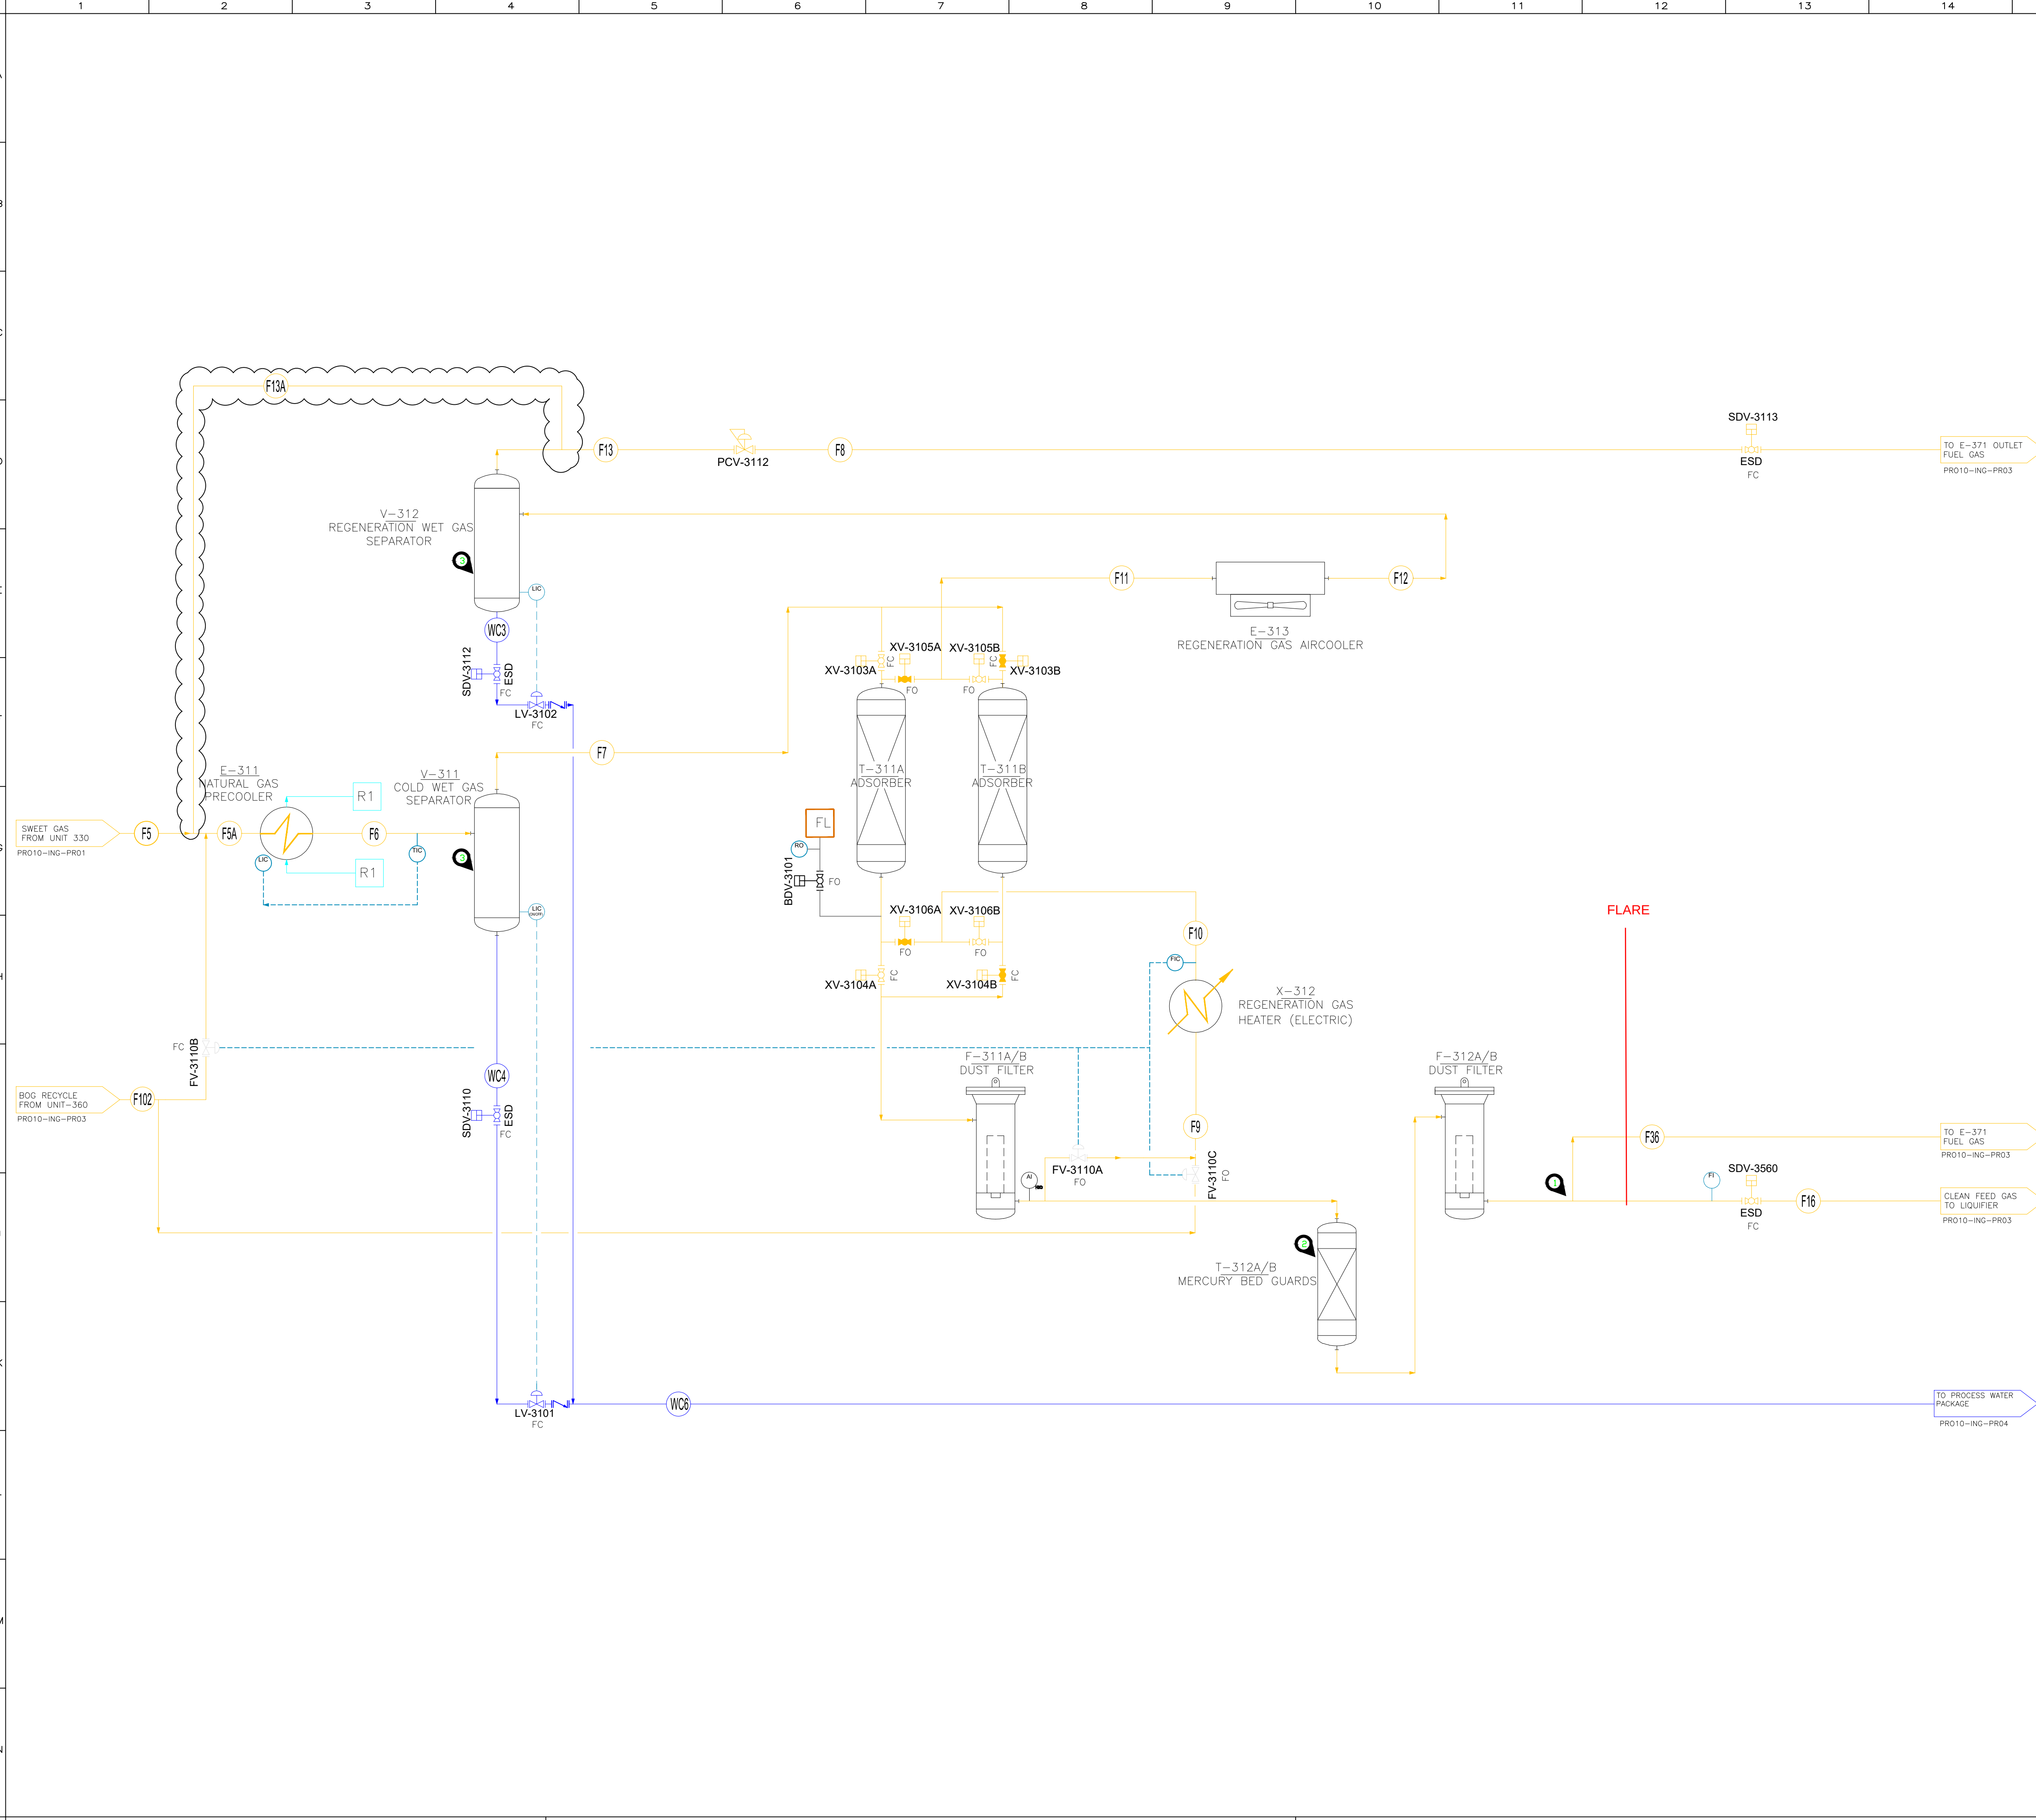

NOTES:

1- FUEL GAS MAKE UP LINE / ADDITIONAL MAKEUP LINE UPSTREAM THIS BRANCH WILL ALSO BE PROVIDED TO ALLOW POWER GENERATION INDEPENDENT STARTUP


2- NOT REGENERABLE MERCURY BED

3- SEPARATOR CAN BE VERTICAL/HORIZONTAL. TO BE DECIDED BY TG DURING SKID DETAILED ENGINEERING.

- LEGEND:
- FL TO FLARE SYSTEM
 - R1 R1 REFRIGERANT (AMMONIA)

FLUID LIST			
	CONDENSATES		PSV
	GAS		REFRIGERANT (AMMONIA)
	PROCESS WATER		INSTRUMENTAL LINE
	FRESH WATER		DIESEL
	AMINE		INERT GAS
	HOT OIL		MIXED REFRIGERANT
	LNG		

8	19 Dic 2024	ISSUED FOR APPROVAL	TAM (LD)	I.CAMPLONE	W. BOULALI	
7	6 Oct 2022	ISSUED FOR APPROVAL	TAM (LD)	I.CAMPLONE	W. BOULALI	
6	24 Jun 2022	ISSUED FOR APPROVAL	TAM (LD)	I.CAMPLONE	W. BOULALI	
5	25 Apr 2022	ISSUED FOR APPROVAL	TAM (LD)	I.CAMPLONE	W. BOULALI	
4	22 Feb 2022	PRELIMINARY ISSUE FOR TECHNICAL PROPOSED	M.FERRARINI	I.CAMPLONE	W. BOULALI	
3	15 Dec 2021	PRELIMINARY ISSUE FOR TECHNICAL PROPOSED	M.FERRARINI	I.CAMPLONE	W. BOULALI	
2	12 Mar 2021	PRELIMINARY ISSUE FOR TECHNICAL PROPOSED	M.FERRARINI	I.CAMPLONE	W. BOULALI	
1	24 Jan 2021	PRELIMINARY ISSUE FOR TECHNICAL PROPOSED	M.FERRARINI	I.CAMPLONE	W. BOULALI	
0	22 Sept 2020	PRELIMINARY ISSUE FOR TECHNICAL PROPOSED	M.FERRARINI	I.CAMPLONE	W. BOULALI	
Rev.	Date	Description	Draft	Check'd (ITF)	App'd (MSP)	SOUND ENERGY
		Customer:	SOUND ENERGY		OFFICES: Espace les Patios 1st floor, Avenue Annakhil Hay Riad, Rabat 10100	
		Contractor:	I.M.S.P. MOROCCO		OFFICES: Regus Maroc Twin Center, Tour Ouest, Casablanca Tel:tel +213 +29 73 31 91 Fax +213/ 29 73 16 92	
		Engineering:	ITALFLUID		VIA VIVALDI,4 MONTESSILVANO (ITALY) Tel.+39 085 4224374 fax+39 085 4220742	
		Technology Vendor:	TECHNICAL AMERICA INC		OFFICES: 301 N Smith Avenue, 92880 Corona, California (USA) Ph:+1 951 272 9540	
						
TITLE:			OBJECT:			
LNG TENDRARA PLANT			PROCESS FLOW DIAGRAM (GAS DEHYDRATION)			
TYPE	SCALE	DOCUMENTS ID:		VENDOR DOC. CODE		SHEET/OF
A1	N/A	PRO10-ING-PR02		21044-PR-PFD-00001		1/1

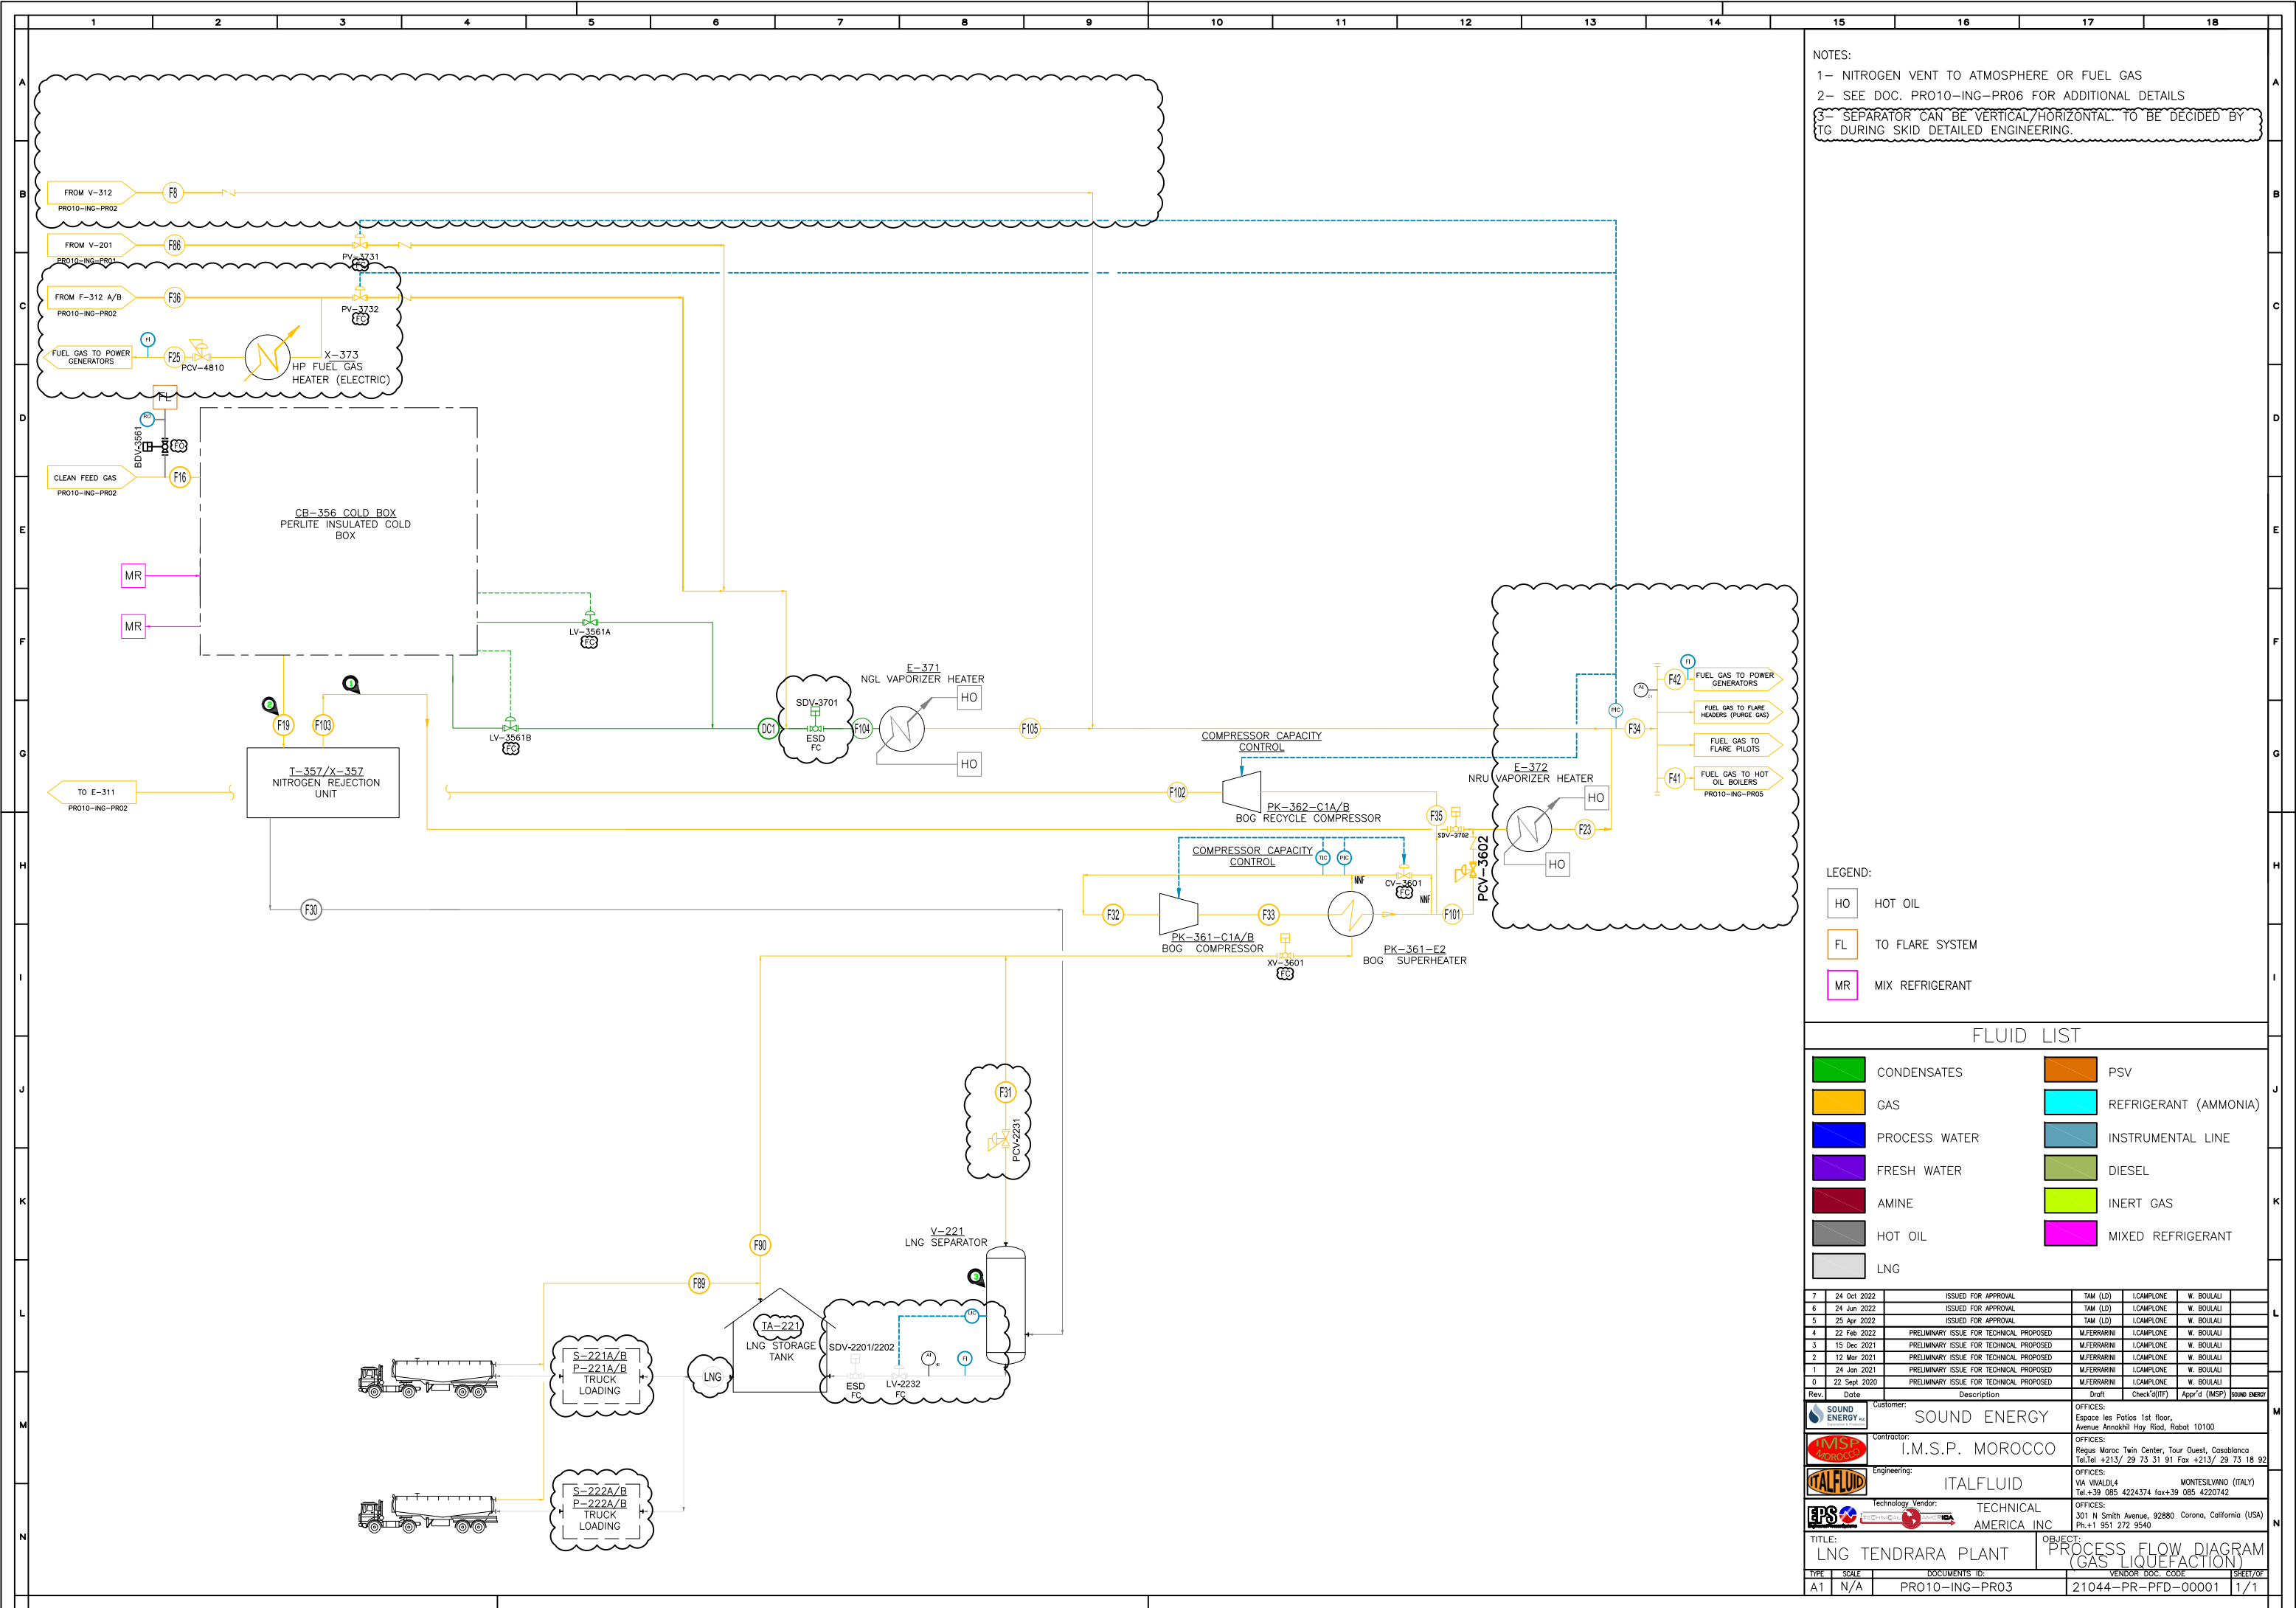

NOTES:
1- NITROGEN VENT TO ATMOSPHERE OR FUEL GAS
2- SEE DOC. PRO10-ING-PR06 FOR ADDITIONAL DETAILS
3- SEPARATOR CAN BE VERTICAL/HORIZONTAL. TO BE DECIDED BY TG DURING SKID DETAILED ENGINEERING.

LEGEND:
HO HOT OIL
FL TO FLARE SYSTEM
MR MIX REFRIGERANT

FLUID LIST			
	CONDENSATES		PSV
	GAS		REFRIGERANT (AMMONIA)
	PROCESS WATER		INSTRUMENTAL LINE
	FRESH WATER		DIESEL
	AMINE		INERT GAS
	HOT OIL		MIXED REFRIGERANT
	LNG		

7	24 Oct 2022	ISSUED FOR APPROVAL	TAM (LD)	LCAMPLONE	W. BOULAL	
6	24 Jun 2022	ISSUED FOR APPROVAL	TAM (LD)	LCAMPLONE	W. BOULAL	
5	25 Apr 2022	ISSUED FOR APPROVAL	TAM (LD)	LCAMPLONE	W. BOULAL	
4	22 Feb 2022	PRELIMINARY ISSUE FOR TECHNICAL PROPOSED	M.FERRARINI	LCAMPLONE	W. BOULAL	
3	15 Dec 2021	PRELIMINARY ISSUE FOR TECHNICAL PROPOSED	M.FERRARINI	LCAMPLONE	W. BOULAL	
2	12 Mar 2021	PRELIMINARY ISSUE FOR TECHNICAL PROPOSED	M.FERRARINI	LCAMPLONE	W. BOULAL	
1	24 Jun 2021	PRELIMINARY ISSUE FOR TECHNICAL PROPOSED	M.FERRARINI	LCAMPLONE	W. BOULAL	
0	22 Sep 2020	PRELIMINARY ISSUE FOR TECHNICAL PROPOSED	M.FERRARINI	LCAMPLONE	W. BOULAL	
Rev.	Date	Description	Draft	Check'd (ITF)	App'd (MSP)	SOUND ENERGY
Customer: SOUND ENERGY			OFFICES: Espace les Patios 1st floor, Avenue Annakhlil Hay Road, Rabat 10100			
Contractor: I.M.S.P. MOROCCO			OFFICES: Regus Maroc Twin Center, Tour Ouest, Casablanca Tel.+39 085 4224374 Fax.+39 085 4220742			
Engineering: ITALFLUID			OFFICES: VIA VIVALDI,4 MONTE SILVANO (ITALY) Tel.+39 085 4224374 fax.+39 085 4220742			
Technology Vendor: TECHNICAL AMERICA INC.			OFFICES: 301 N Smith Avenue, 92880 Corona, California (USA) Ph.+1 951 272 9540			
TITLE: LNG TENDRARA PLANT			OBJECT: PROCESS FLOW DIAGRAM (GAS LIQUEFACTION)			
TYPE	SCALE	DOCUMENTS ID:	VENDOR DOC. CODE		SHEET/DF	
A1	N/A	PRO10-ING-PR03	21044-PR-PFD-00001		1/1	