


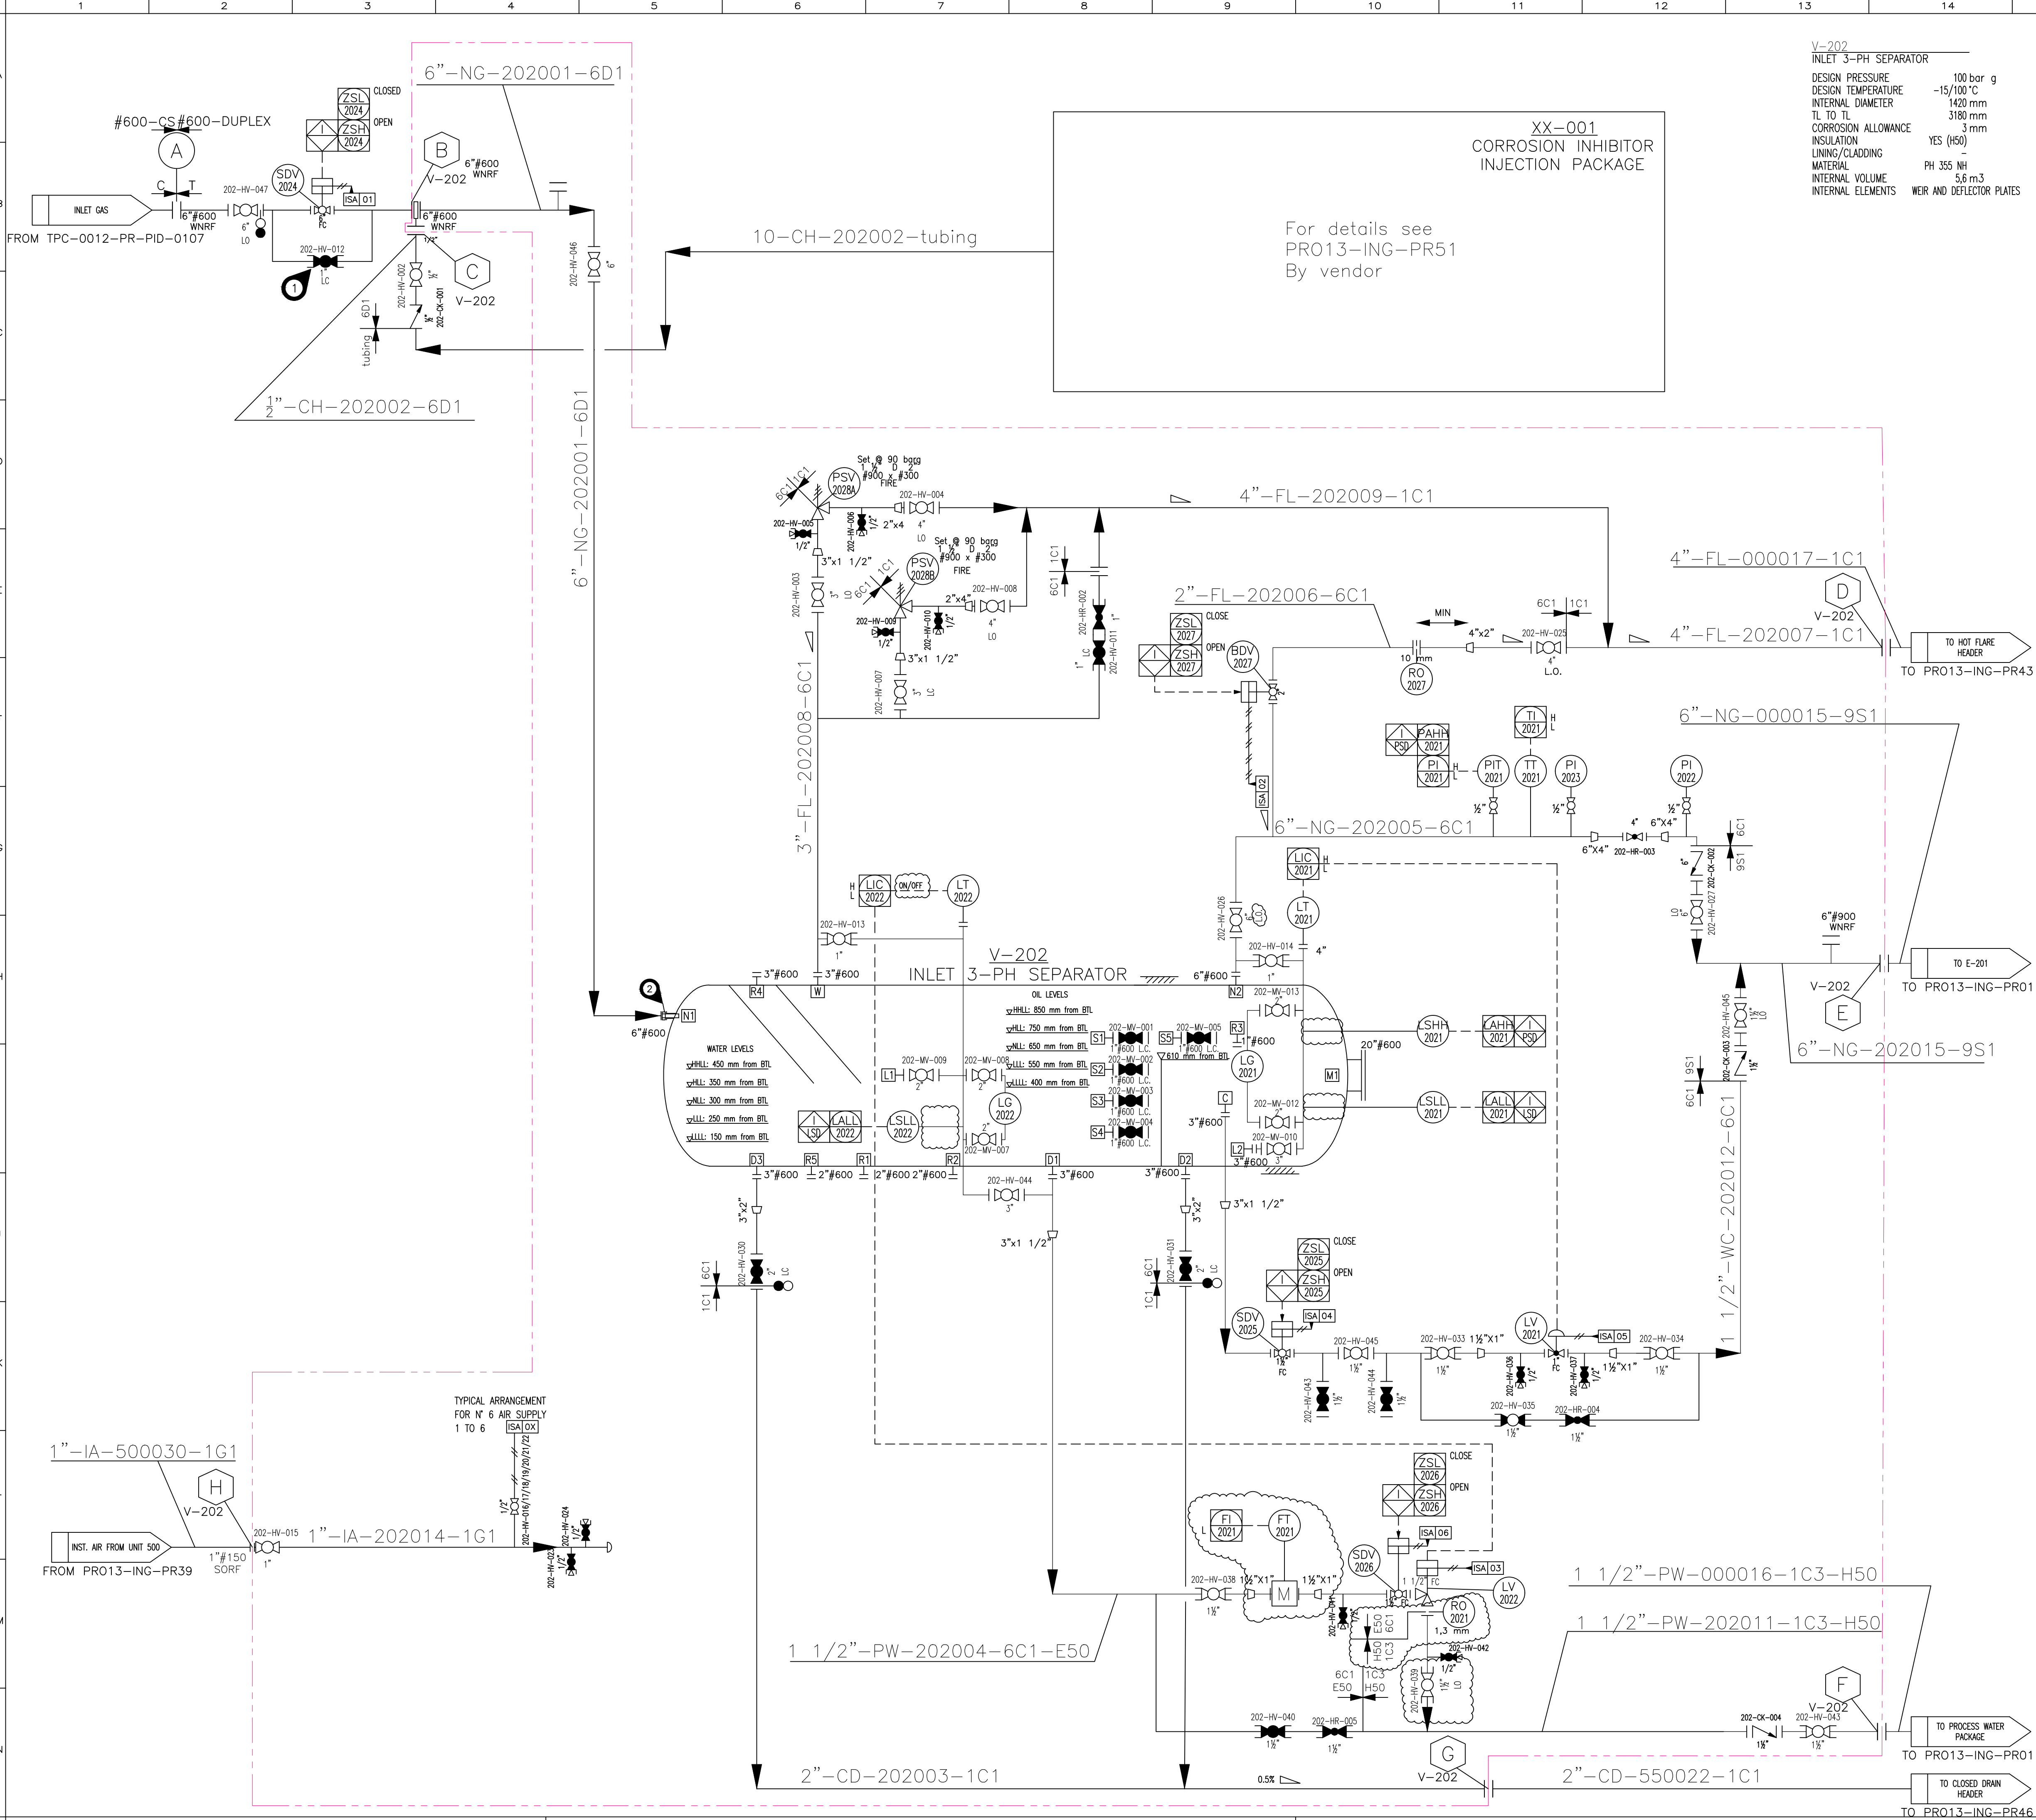

V-202
INLET 3-PH SEPARATOR
DESIGN PRESSURE 100 bar g
DESIGN TEMPERATURE -15/100 °C
INTERNAL DIAMETER 1420 mm
TL TO TL 3180 mm
CORROSION ALLOWANCE 3 mm
INSULATION YES (H50)
LINING/CLADDING PH 355 NH
MATERIAL INTERNAL VOLUME 5.6 m³
INTERNAL ELEMENTS WEIR AND DEFLECTOR PLATES

XX-001
CORROSION INHIBITOR
INJECTION PACKAGE

For details see
PRO13-ING-PR51
By vendor

REFERENCE DOCUMENTS	
P&ID LEGEND	PRO13-ING-PR00 21044-PR-PID-00000
PROCESS FLOW DIAGRAM	PRO10-ING-PRO1/02/03/04 21044-PR-PFD-00001
UTILITY FLOW DIAGRAM	PRO10-ING-PR11 21044-PR-UFD-00001
MATERIAL SELECTION DIAGRAM	PRO08-ING-FR01 21044-PR-MSD-00001

- NOTES
- 1 BYPASS OF SDV-2024 INSTALLED FOR START UP.
 - 2 INNER DUPLEX PIPE WELDED TO A DRIP RING

Rev.	Date	Description	Draft	Check'd (ITF)	App'd (ITF)	SOUND ENERGY
5	27-03-2025	APPROVED FOR CONSTRUCTION	P.MARZIANI	A.ZAPPONE	L.CAMPLONE	
4	14-10-2024	APPROVED FOR CONSTRUCTION	P.MARZIANI	A.ZAPPONE	L.CAMPLONE	
3	16-10-2023	REVISED WHERE INDICATED	P.MARZIANI	A.ZAPPONE	L.CAMPLONE	
2	23-06-2023	REVISED WHERE INDICATED	P.MARZIANI	A.ZAPPONE	L.CAMPLONE	
1	22-05-2023	ISSUED FOR APPROVAL	P.MARZIANI	A.ZAPPONE	L.CAMPLONE	
0	04-05-2023	ISSUED FOR APPROVAL	M.FERRARINI	A.ZAPPONE	L.CAMPLONE	
Customer: SOUND ENERGY						
Contractor: ITALFLUID						
Engineering: ITALFLUID						
Technology Vendor: TECHNICAL AMERICA INC						
OFFICES: Espace les Patios 1st floor, Avenue Annakhil Hay Riad, Rabat 10100						
OFFICES: VIA VIVALDI,4 MONTESSILVANO (ITALY) Tel.+39 085 4224374 fax+39 085 4220742						
OFFICES: VIA VIVALDI,4 MONTESSILVANO (ITALY) Tel.+39 085 4224374 fax+39 085 4220742						
OFFICES: Ph.+1 951 272 9540 Corona, California (USA)						
TITLE: P&ID PLANT INLET - LNG TENDRARA PLANT			OBJECT: P&ID PLANT INLET - UNIT 200 - V-202			
TYPE: N/A			VENDOR DOC. CODE			
SCALE: PRO13-ING-PR50			SHEET/OF: 1/1			