


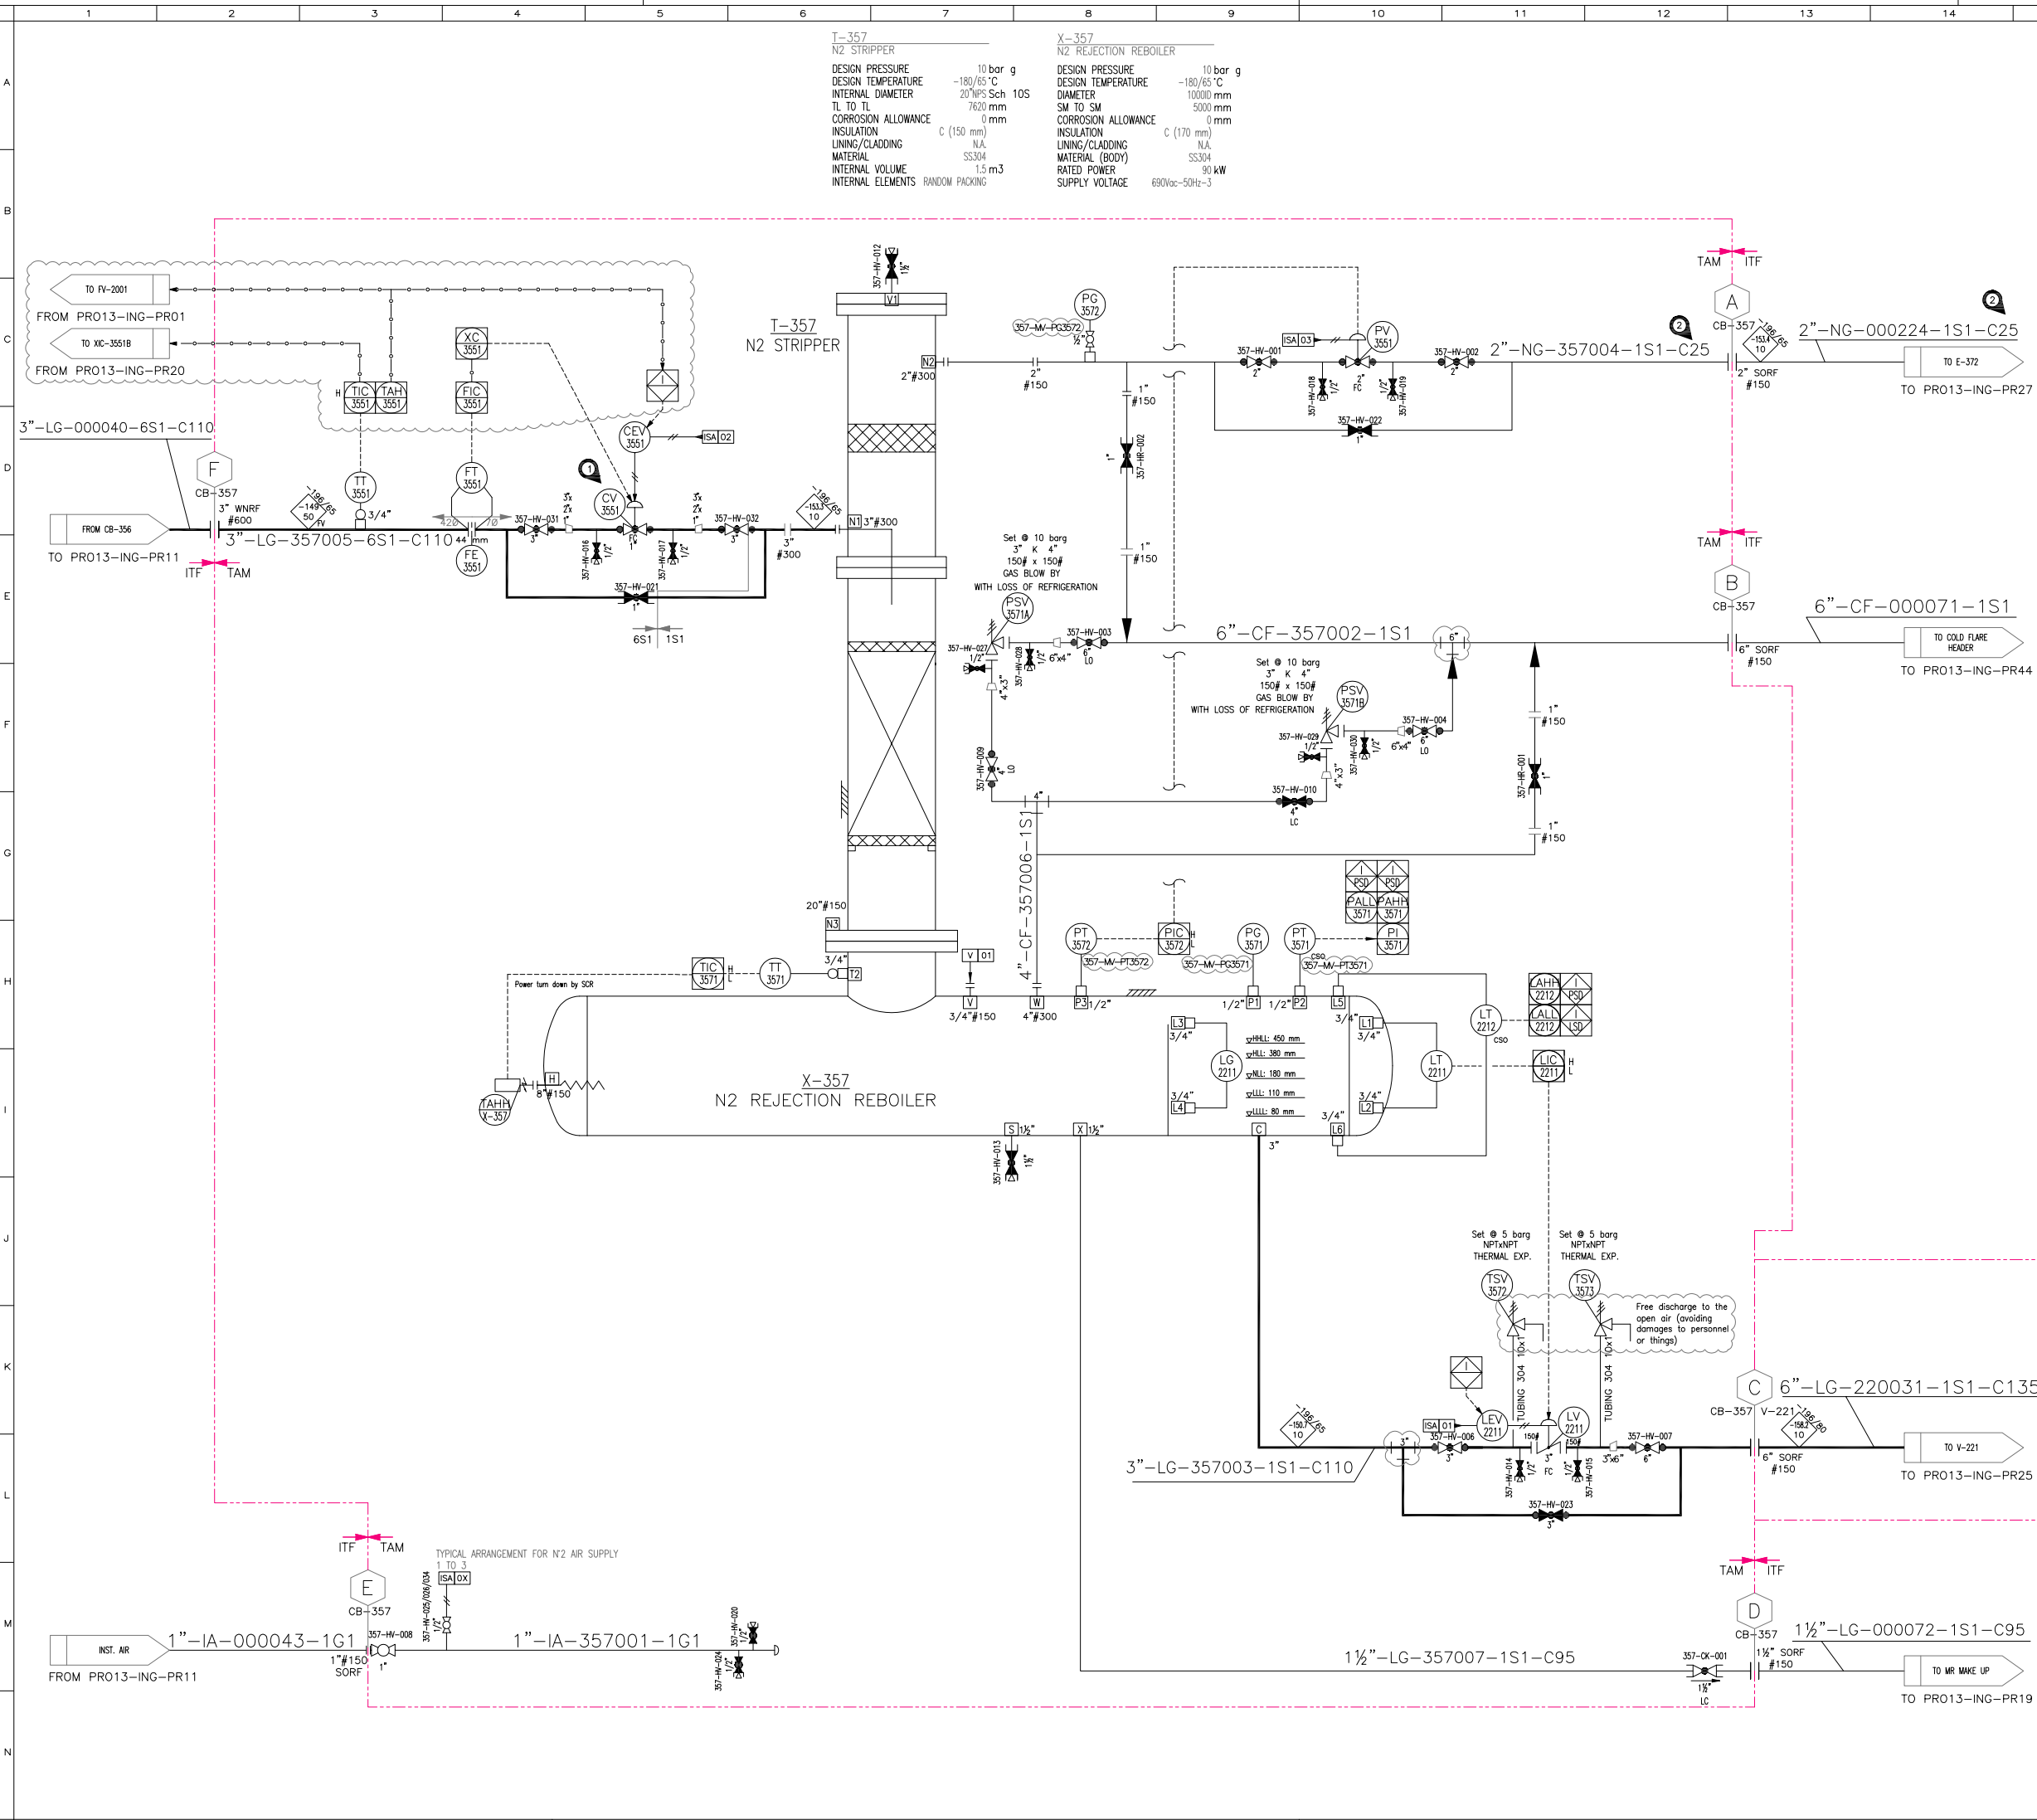

15		16		17		18	
REFERENCE DOCUMENTS							
P&ID LEGEND				PRO13-ING-PRO0			
PROCESS FLOW DIAGRAM				21044-PR-PID-00000			
UTILITY FLOW DIAGRAM				PRO10-ING-PRO1/02/03/04			
MATERIAL SELECTION DIAGRAM				21044-PR-PFD-00001			
				PRO10-ING-PR11			
				21044-PR-UFD-00001			
				PRO08-ING-FR01			
				21044-PR-MSD-00001			
ISA 0X INSTRUMENT SUPPLY AIR							
V 0X VENT							
NOTES							
1 FIRESAFE GLOBE VALVE.							
2 LINE IS INSULATED NOT FOR COLD CONSERVATION, BUT TO AVOID ICE BUILD UP ON PIPE SURFACE.							
----- TAM SUPPLY LIMIT							