


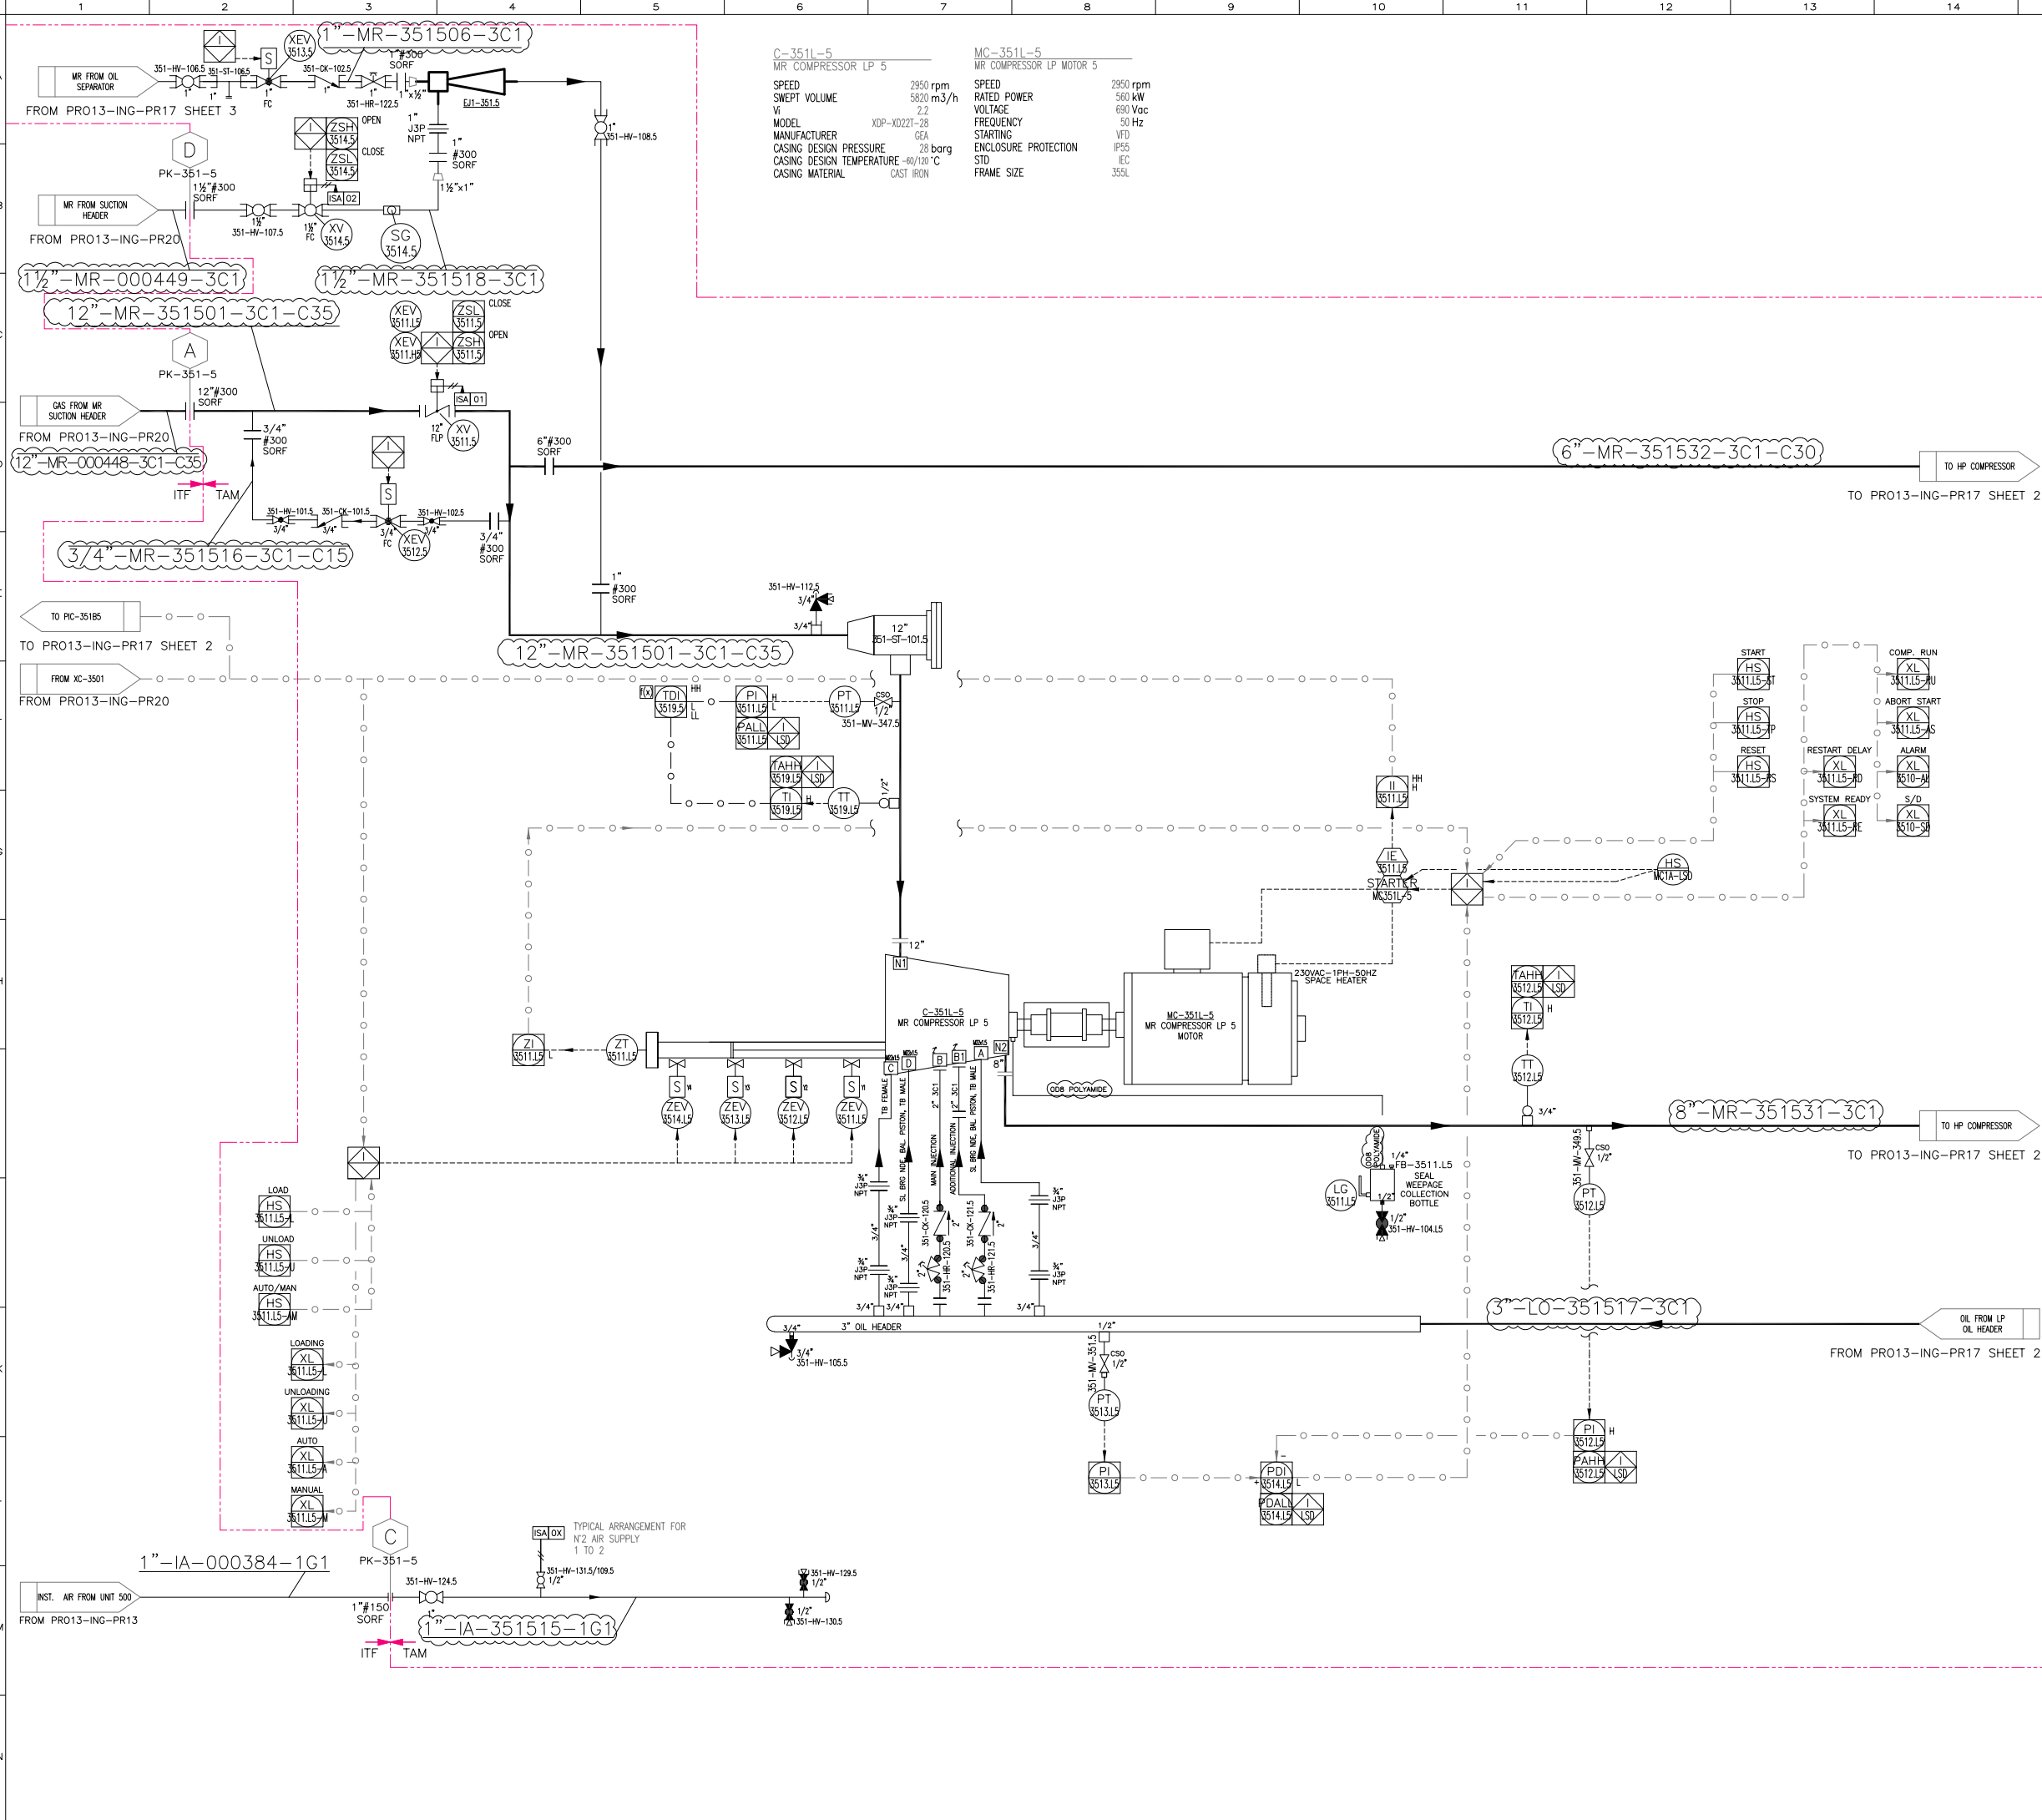

REFERENCE DOCUMENTS

P&ID LEGEND	PRO13-ING-PRO0
PROCESS FLOW DIAGRAM	21044-PR-PID-00000
UTILITY FLOW DIAGRAM	PRO10-ING-PRO1/02/03/04
MATERIAL SELECTION DIAGRAM	21044-PR-PFD-00001
	PRO10-ING-PR11
	21044-PR-UFD-00001
	PRO08-ING-FR01
	21044-PR-MSD-00001

INSTRUMENT SUPPLY AIR

ISA 0X

NOTES:

----- TAM SUPPLY LIMIT

1	25 Mar 2026	ISSUE FOR COMMISSIONING	TAM (JB)	TAM (MM)	LCAMPLONE
0	08 Jan 2026	AS BUILT	TAM (JB)	LCAMPLONE	W.BOUALALI
Rev.	Date	Description	Draft	Check'd	Approved

Customer: MANAENERGY

Contractor: ITALFLUID

Engineering: ITALFLUID

Technology Vendor: TECHNICAL AMERICA INC

OFFICES: Mahaj Riad Center, Batiment 6, Jeme elage, Avenue Al Az, Hay Ryad, 10100 Rabat, Morocco

OFFICES: VIA VVALDI,4 MONTESILVANO (ITALY) Tel.+39 085 4224374 fax+39 085 4220742


OFFICES: VIA VVALDI,4 MONTESILVANO (ITALY) Tel.+39 085 4224374 fax+39 085 4220742

OFFICES: 301 N Smith Avenue, 92880 Corona, California (USA) Ph.+1 951 272 9540

TITLE: LNG TENDRARA PLANT

OBJECT: P&ID PACKAGE PK-351-5 (UNIT 350)

TYPE	SCALE	DOCUMENTS ID:	VENDOR DOC CODE:	SHEET/OF
A1	N/A	PRO13-ING-PR17	21044-PR-PID-35005	1/3

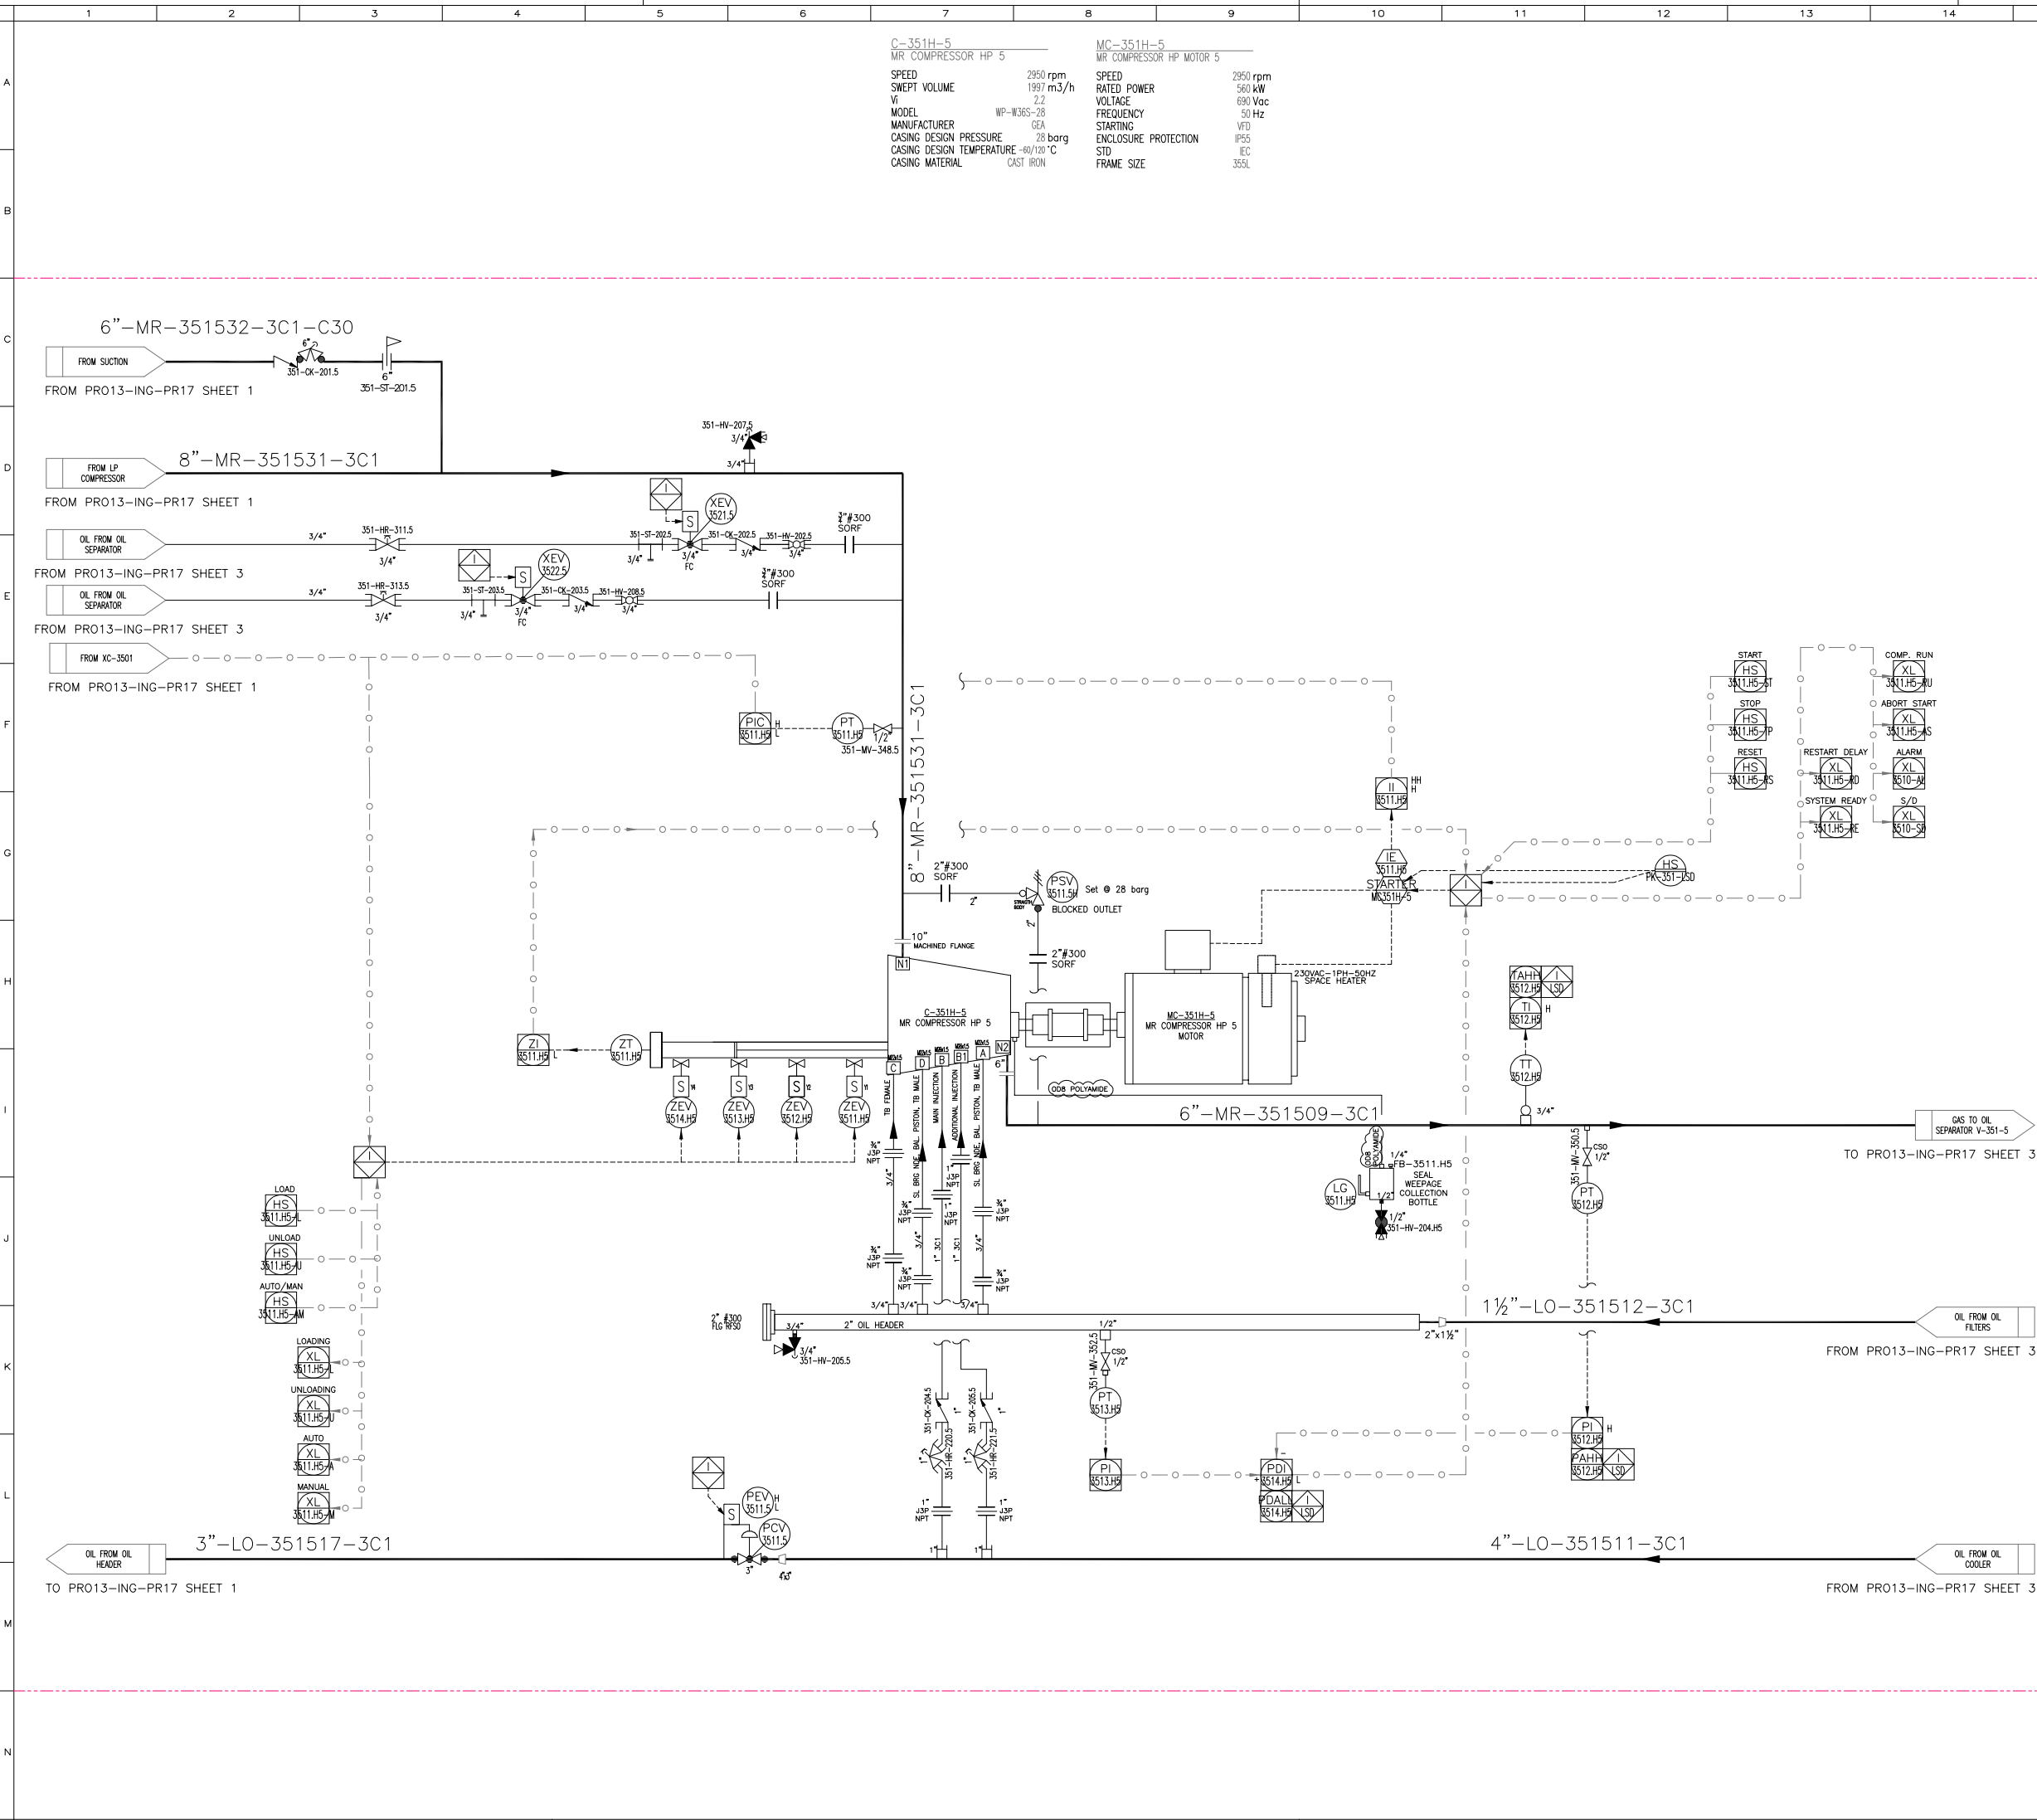

15		16		17		18	
REFERENCE DOCUMENTS							
P&ID LEGEND				PRO13-ING-PROO 21044-PR-PID-00000			
PROCESS FLOW DIAGRAM				PRO10-ING-PRO1/02/03/04 21044-PR-PFD-00001			
UTILITY FLOW DIAGRAM				PRO10-ING-PR11 21044-PR-UFD-00001			
MATERIAL SELECTION DIAGRAM				PRO08-ING-FR01 21044-PR-MSD-00001			
ISA 0X INSTRUMENT SUPPLY AIR							
NOTES: ----- TAM SUPPLY LIMIT							
1	25 Mar 2026	ISSUE FOR COMMISSIONING			TAM (JB)	TAM (MM)	LCAMPLONE
0	08 Jan 2026	AS BUILT			TAM (JB)	LCAMPLONE	W.BOUILAU
Rev.	Date	Description			Draft	Check'd	Approved
Customer: MANAENERGY				OFFICES: Mahaj Riad Center, Batiment 6, 3eme etage, Avenue Al Arz, Hay Ryad, 10100 Rabat, Morocco			
Contractor: ITALFLUID				OFFICES: VA VIVALDI,4 MONTESILVANO (ITALY) Tel.+39 085 4224374 fax+39 085 4220742			
Engineering: ITALFLUID				OFFICES: VA VIVALDI,4 MONTESILVANO (ITALY) Tel.+39 085 4224374 fax+39 085 4220742			
Technology Vendor: TECHNICAL AMERICA INC				OFFICES: 301 N Smith Avenue, 92880 Corona, California (USA) Ph.+1 951 272 9540			
TITLE: LNG TENDRARA PLANT				OBJECT: P&ID PACKAGE PK-351-5 (UNIT 350)			
TYPE	SCALE	DOCUMENTS ID:			VENDOR DOC CODE:		SHEET/OF
A1	N/A	PRO13-ING-PR17			21044-PR-PID-35005		2/3

