


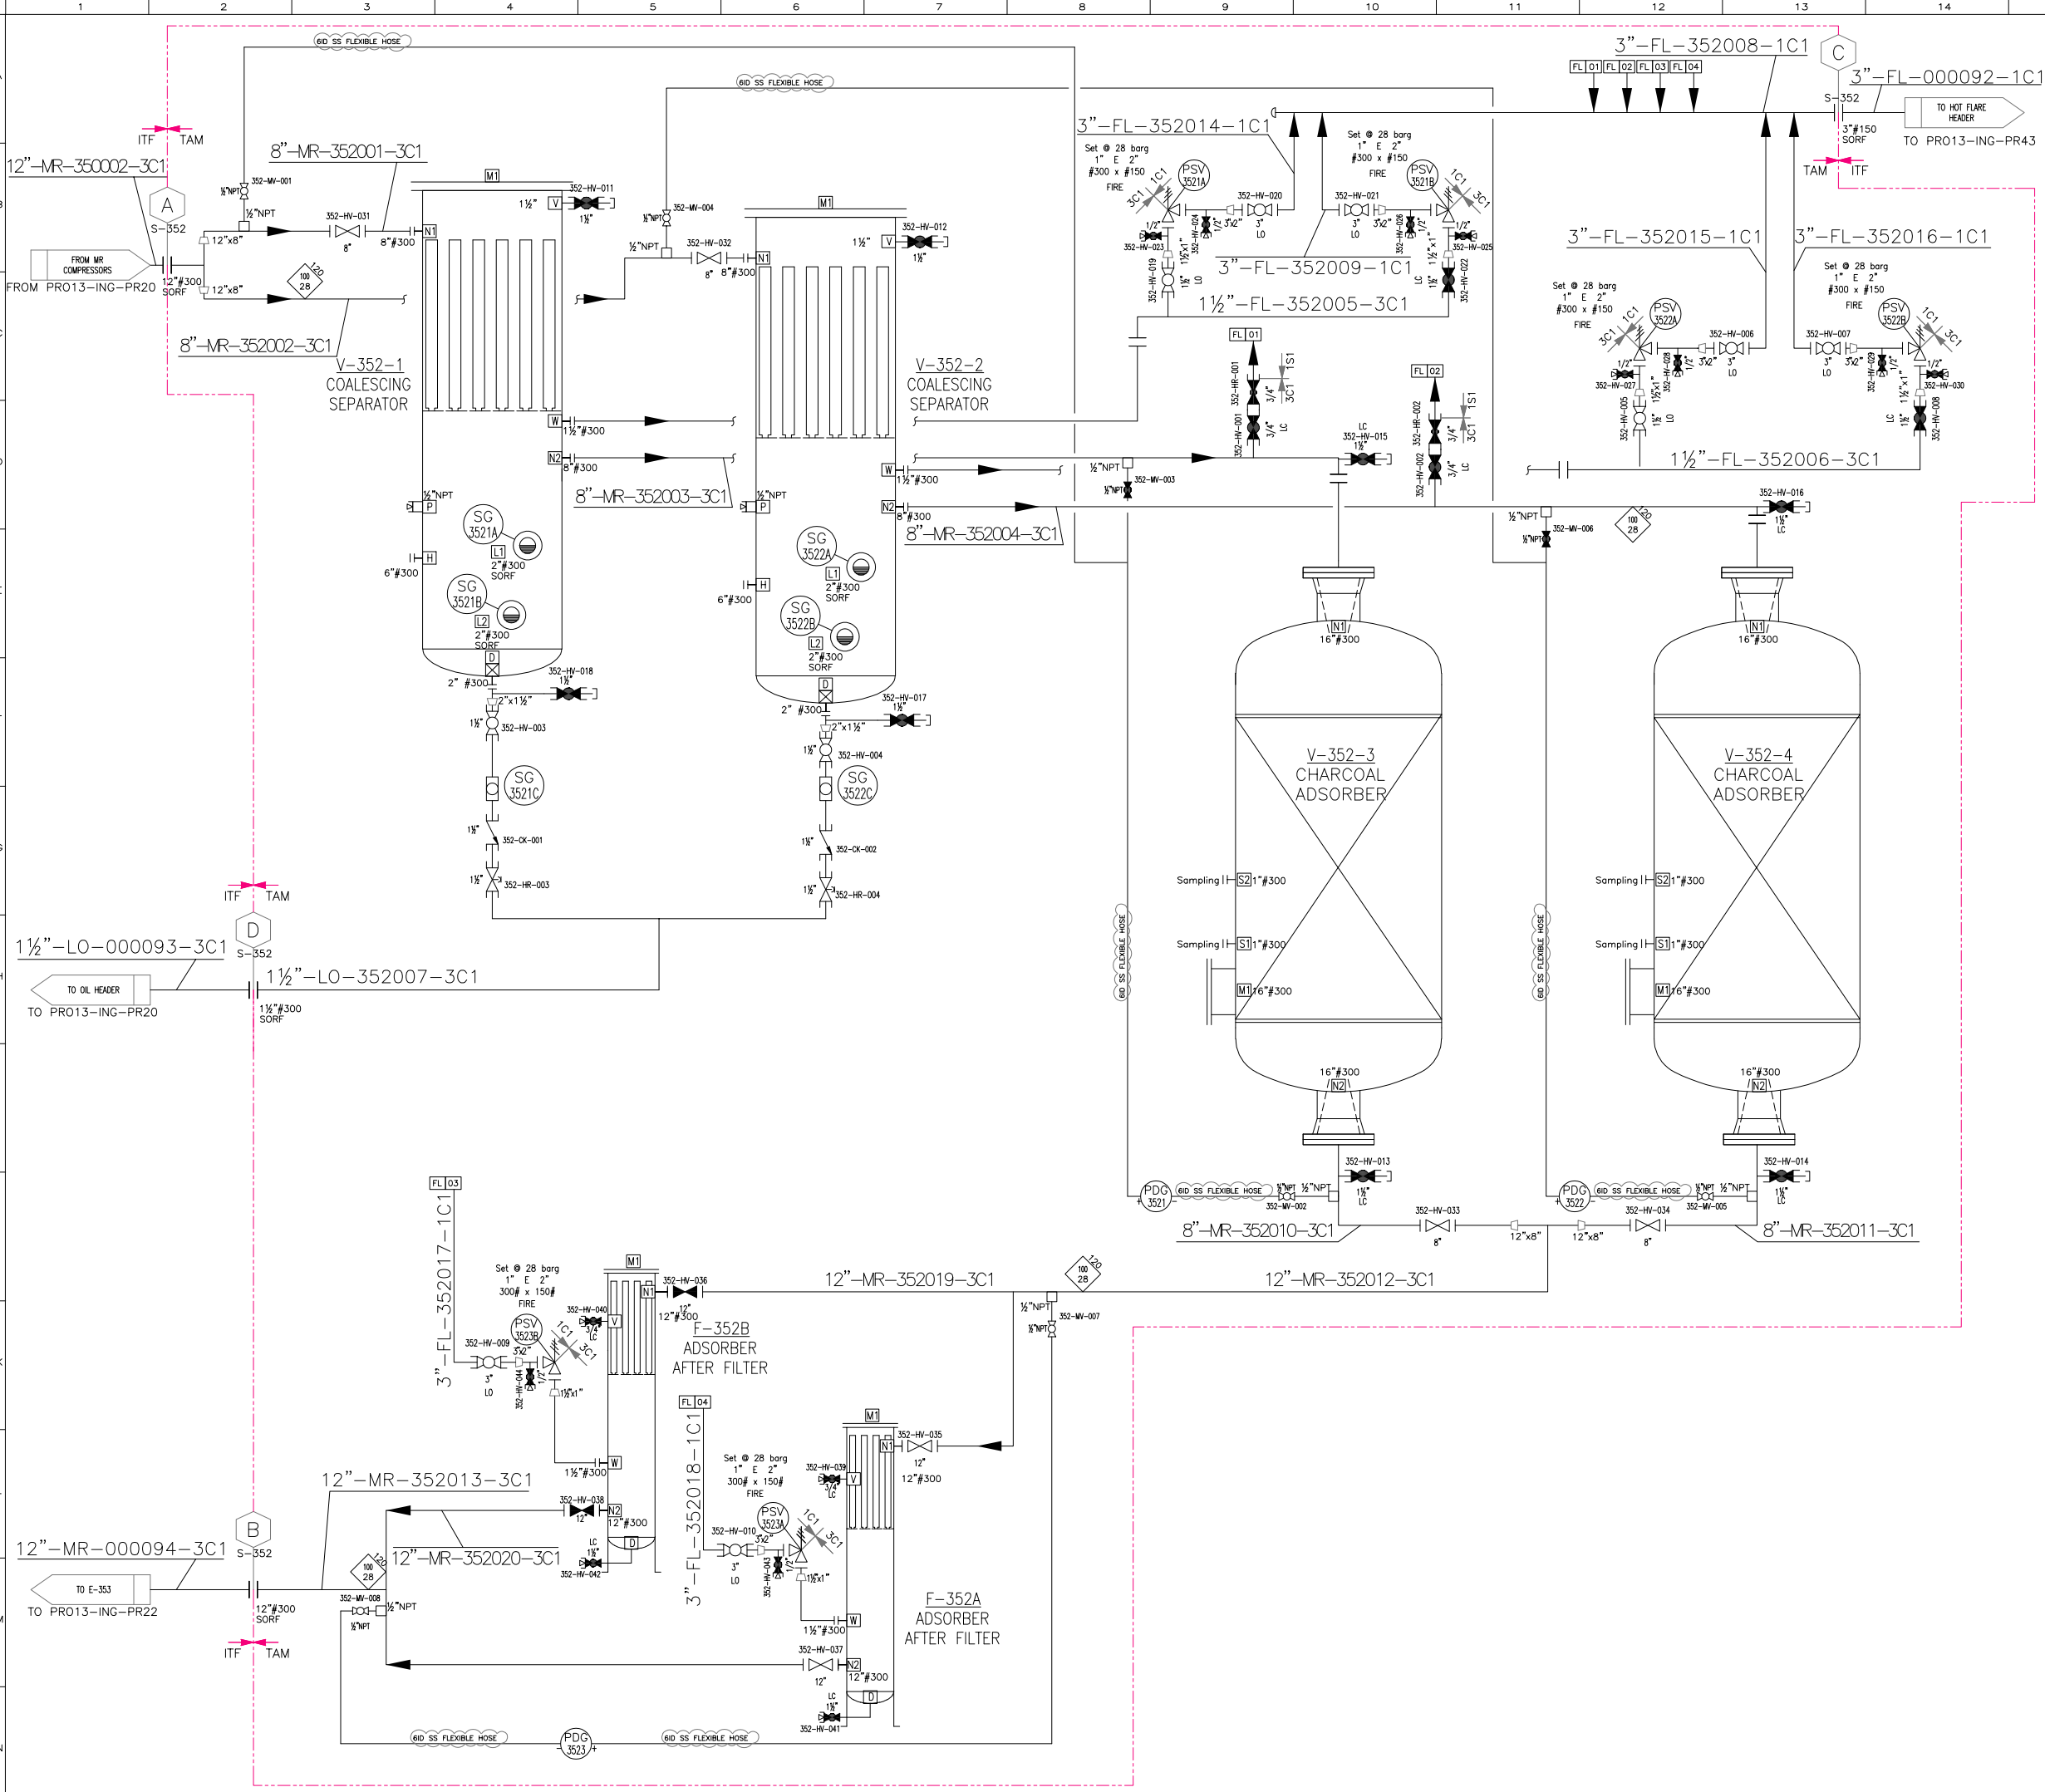

15		16		17		18	
REFERENCE DOCUMENTS	
P&ID LEGEND				PRO13-ING-PROO	
PROCESS FLOW DIAGRAM				21044-PR-PID-00000	
UTILITY FLOW DIAGRAM				PRO10-ING-PRO6	
MATERIAL SELECTION DIAGRAM				21044-PR-UFD-00001	
				PRO08-ING-FR01	
				21044-PR-MSD-00001	
V-352-1/2 COALESCING SEPARATOR DESIGN PRESSURE28 bar g DESIGN TEMPERATURE-15/120 °C DIAMETER1200 ID mm SM TO SM1500 mm CORROSION ALLOWANCE0 mm INSULATIONNo LINING/CLADDINGN.A. MATERIALCS INTERNAL VOLUME2.3 m3 INTERNAL ELEMENTS(15) Cartridge 6" 00	
F-352A/B ADSORBER AFTER FILTER DESIGN PRESSURE28 bar g DESIGN TEMPERATURE-15/120 °C DIAMETER900 ID mm SM TO SM1500 mm CORROSION ALLOWANCE0 mm INSULATIONNo LINING/CLADDINGN.A. MATERIALCS INTERNAL VOLUME1.2 m3 INTERNAL ELEMENTS(10) Cartridge 7" 00	
V-352-3/4 CHARCOAL ADSORBER DESIGN PRESSURE28 bar g DESIGN TEMPERATURE-15/120 °C DIAMETER2000 ID mm SM TO SM4000 mm CORROSION ALLOWANCE0 mm INSULATIONNo LINING/CLADDINGN.A. MATERIALCS INTERNAL VOLUME15 m3 INTERNAL ELEMENTSCharcoal	
FL 0X VENT TO FLARE HEADER	
----- TAM SUPPLY LIMIT	
<table><tr><td>5</td><td>03 Apr 2026</td><td>APPROVED FOR CONSTRUCTION</td><td>TAM (JB)</td><td>TAM (UM)</td><td>L.CAMPLONE</td></tr><tr><td>4</td><td>15 Feb 2024</td><td>APPROVED FOR CONSTRUCTION</td><td>TAM (LD)</td><td>L.CAMPLONE</td><td>W.BOUALAI</td></tr><tr><td>3</td><td>26 Jul 2023</td><td>ISSUED FOR APPROVAL</td><td>TAM (LD)</td><td>L.CAMPLONE</td><td>W.BOUALAI</td></tr><tr><td>2</td><td>02 Nov 2022</td><td>ISSUED FOR APPROVAL</td><td>TAM (LD)</td><td>L.CAMPLONE</td><td>W.BOUALAI</td></tr><tr><td>1</td><td>25 Jul 2022</td><td>ISSUED FOR APPROVAL</td><td>TAM (ES)</td><td>L.CAMPLONE</td><td>W.BOUALAI</td></tr><tr><td>0</td><td>30 Jun 2022</td><td>ISSUED FOR APPROVAL</td><td>TAM (ES)</td><td>L.CAMPLONE</td><td>W.BOUALAI</td></tr><tr><td>Rev.</td><td>Date</td><td>Description</td><td>Draft</td><td>Check'd</td><td>Approved</td></tr></table> Customer:MANAENERGY Contractor:ITALFLUID Engineering:ITALFLUID Technology Vendor:TECHNICAL AMERICA INC Offices: Mahaj Riad Center, Batiment 6, 3eme etage, Avenue Al Az, Hay Ryad, 10100 Rabat, Morocco Offices: VIA VVALDI,4 Tel.+39 085 4224374 fax+39 085 4220742 Offices: VIA VVALDI,4 Tel.+39 085 4224374 fax+39 085 4220742 Offices: 301 N Smith Avenue, 92880 Corona, California (USA) Ph.+1 951 272 9540 TITLE: LNG TENDRARA PLANT OBJECT: P&ID UNIT 350 - SKID S-352 - ORS TYPE A1 SCALE N/A DOCUMENTS ID: PRO13-ING-PR21 VENDOR DOC. CODE 21044-PR-PID-35009 SHEET/OF 1/1								5	03 Apr 2026	APPROVED FOR CONSTRUCTION	TAM (JB)	TAM (UM)	L.CAMPLONE	4	15 Feb 2024	APPROVED FOR CONSTRUCTION	TAM (LD)	L.CAMPLONE	W.BOUALAI	3	26 Jul 2023	ISSUED FOR APPROVAL	TAM (LD)	L.CAMPLONE	W.BOUALAI	2	02 Nov 2022	ISSUED FOR APPROVAL	TAM (LD)	L.CAMPLONE	W.BOUALAI	1	25 Jul 2022	ISSUED FOR APPROVAL	TAM (ES)	L.CAMPLONE	W.BOUALAI	0	30 Jun 2022	ISSUED FOR APPROVAL	TAM (ES)	L.CAMPLONE	W.BOUALAI	Rev.	Date	Description	Draft	Check'd	Approved
5	03 Apr 2026	APPROVED FOR CONSTRUCTION	TAM (JB)	TAM (UM)	L.CAMPLONE	
4	15 Feb 2024	APPROVED FOR CONSTRUCTION	TAM (LD)	L.CAMPLONE	W.BOUALAI	
3	26 Jul 2023	ISSUED FOR APPROVAL	TAM (LD)	L.CAMPLONE	W.BOUALAI	
2	02 Nov 2022	ISSUED FOR APPROVAL	TAM (LD)	L.CAMPLONE	W.BOUALAI	
1	25 Jul 2022	ISSUED FOR APPROVAL	TAM (ES)	L.CAMPLONE	W.BOUALAI	
0	30 Jun 2022	ISSUED FOR APPROVAL	TAM (ES)	L.CAMPLONE	W.BOUALAI	
Rev.	Date	Description	Draft	Check'd	Approved	