


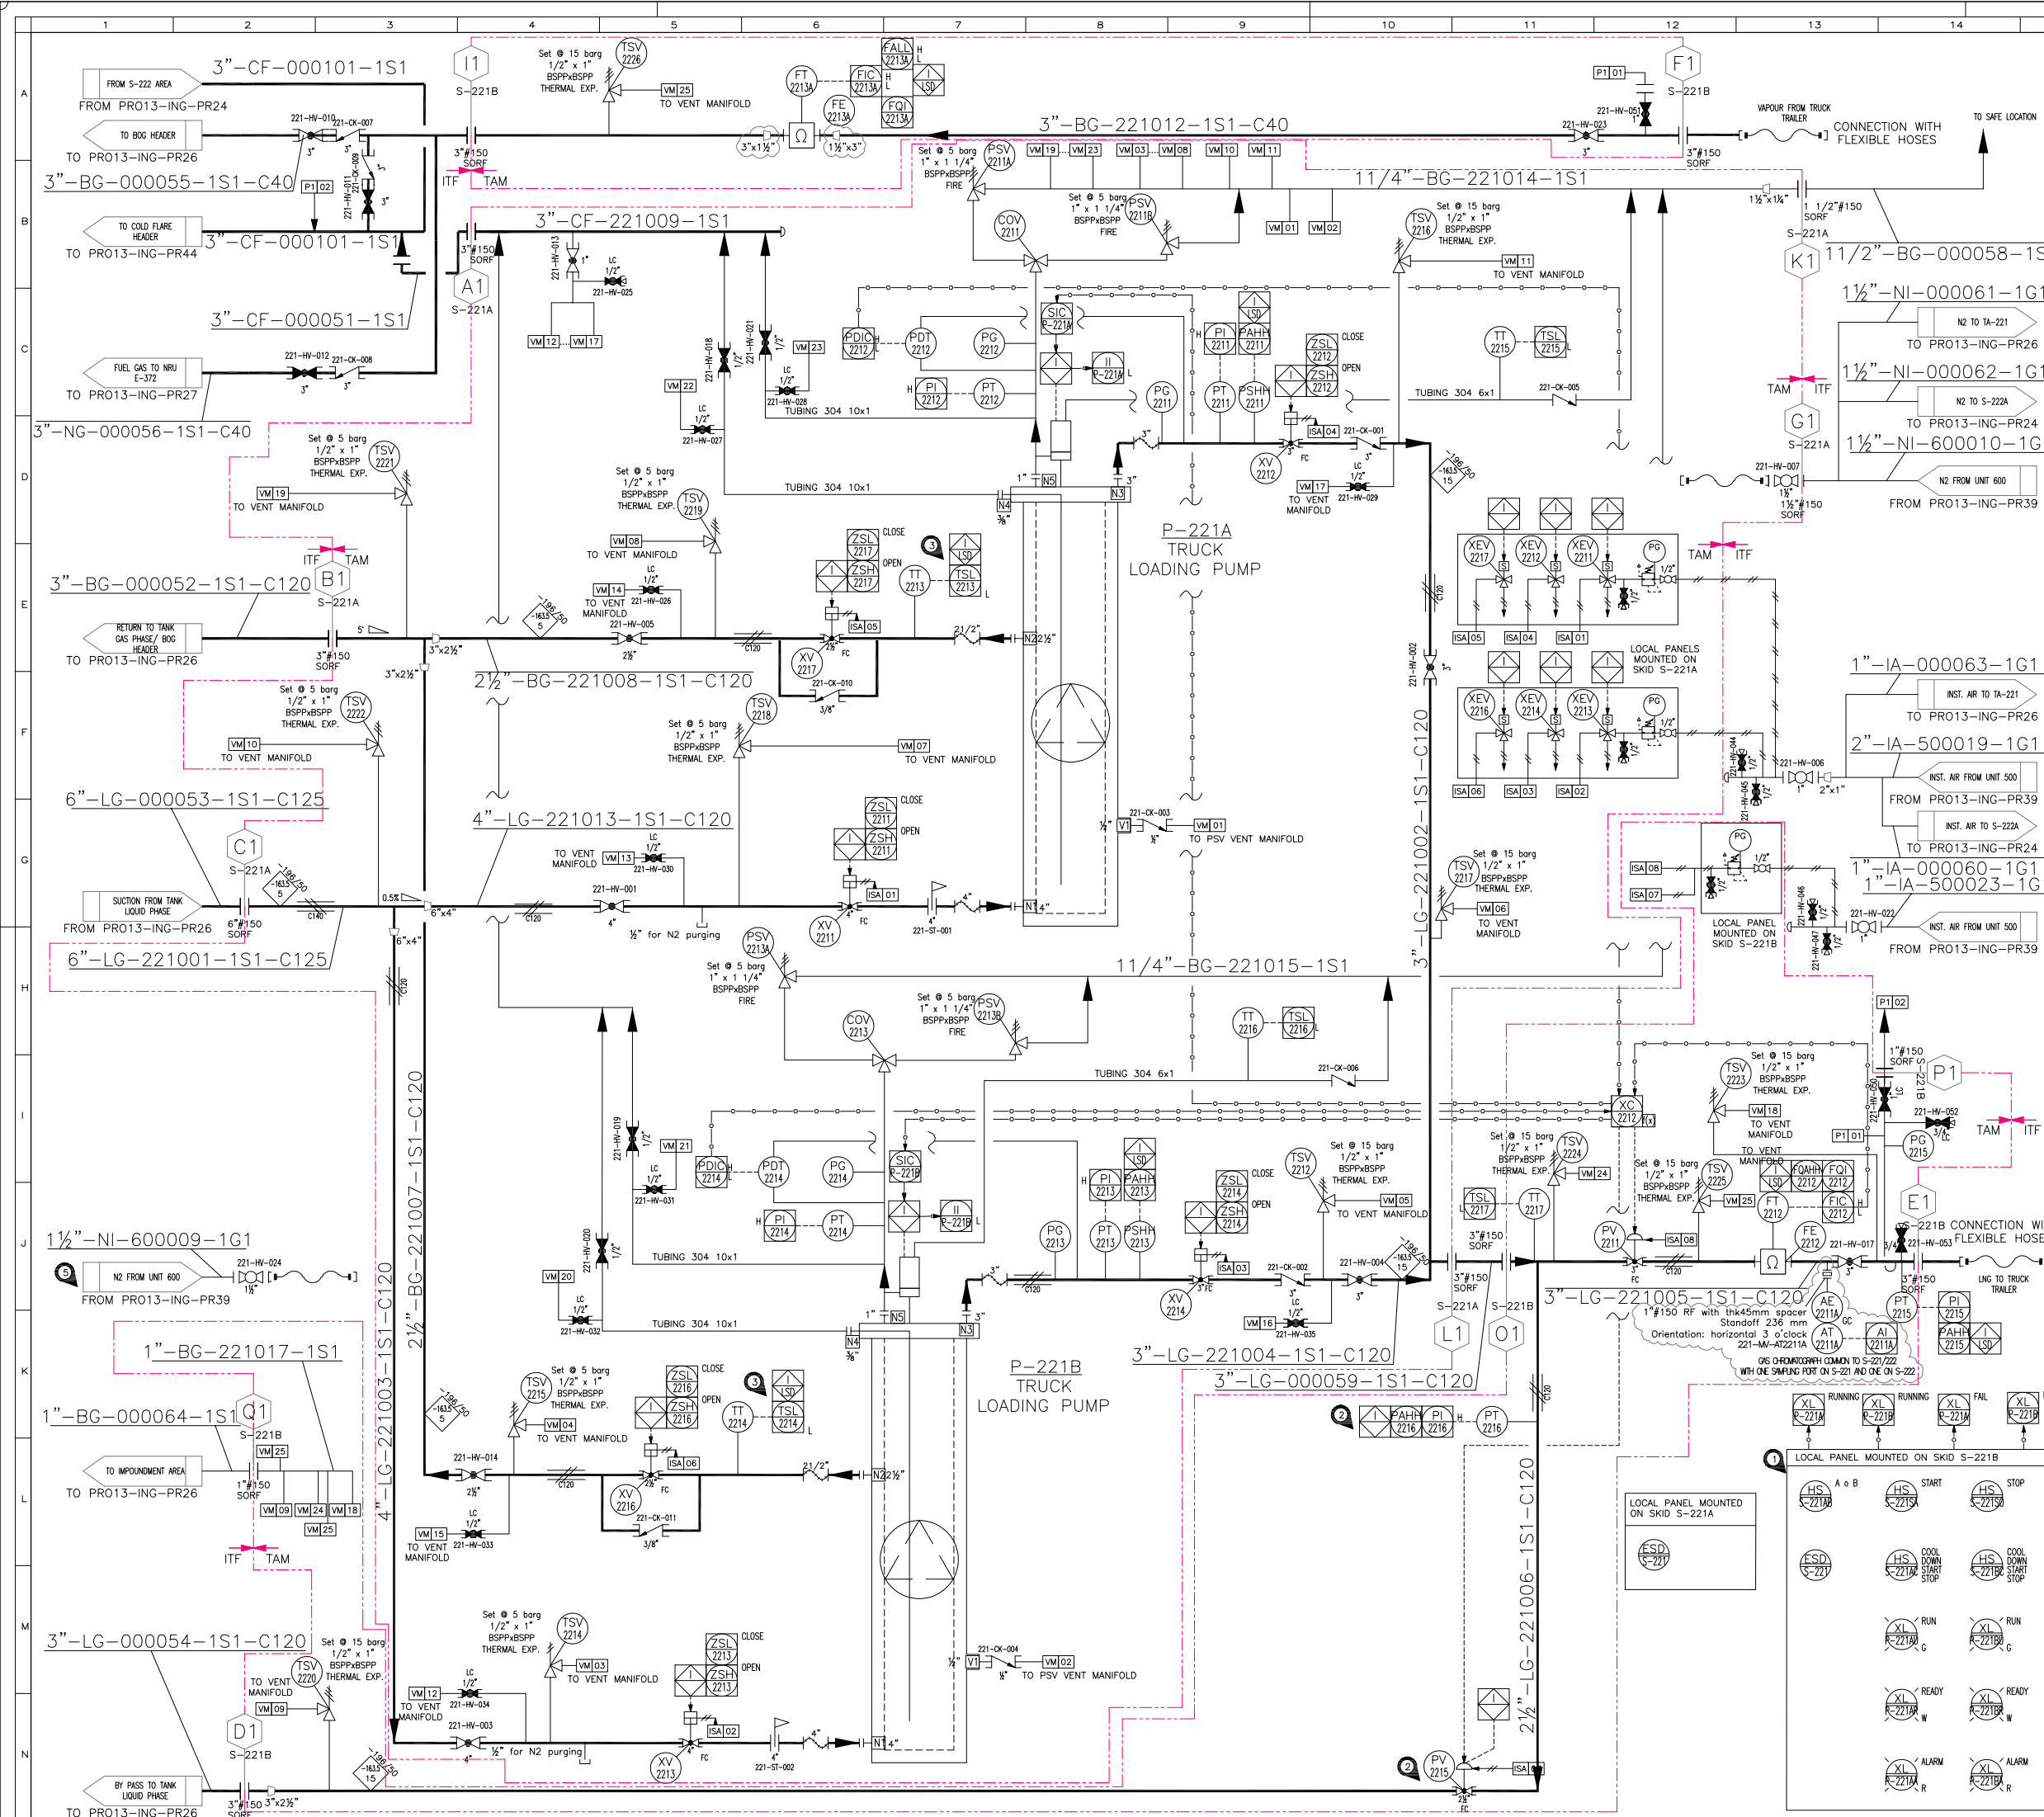

REFERENCE DOCUMENTS			
P&ID LEGEND	PRO13-ING-PR00		
PROCESS FLOW DIAGRAM	21044-PR-PID-00000		
UTILITY FLOW DIAGRAM	PRO10-ING-PR11		
MATERIAL SELECTION DIAGRAM	21044-PR-MSD-00001		

INSTRUMENT SUPPLY AIR			
P-221A/B TRUCK LOADING PUMPS			
SPEED	0-3650 rpm		
RATED CAPACITY	80 m ³ /h		
HEAD	170 m		
TYPE	CENTRIFUGAL / CRYO SUBMERGED		
MANUFACTURER	WANZETI		
CASING DESIGN PRESSURE	15 barg		
CASING DESIGN TEMP.	-196/40 °C		
MODEL	ARTIKA 230-2S		
ABS POWER	75 kW		
CASING MATERIAL	STAINLESS STEEL		

MP-221A/B TRUCK LOADING PUMPS ELECTRIC MOTORS			
SPEED	0-3650 rpm		
RATED POWER	30 kW		
VOLTAGE	400 V ac		
FREQUENCY	50 Hz		
STARTING	VFD		
ENCLOSURE PROTECTION	IP54		
STD	Manuf. std		
FRAME SIZE	N/A		

- NOTES
- 1 EACH SKID INCLUDES A LOCAL PANEL FOR START/STOP AND SIGNALING.
 - 2 PV-2215 CLOSED IN NORMAL OPERATION. IT WILL BE FORCED TO OPEN BY A PAHH SIGNAL FROM PT-2216.
 - 3 PUMP STOPS WITH SIGNAL FROM LOSS OF PERMISSIVE OF TSL.
 - 4 AT THE BEGINNING OF THE LOADING PROCESS THE OPERATOR SHALL SEND THE BOG FROM THE TRUCKS TO FLARE BECAUSE CONTAMINANTS MAY BE PRESENT INSIDE THE TRUCKS.
 - 5 NITROGEN SUPPLY ON S-221B AREA
 - 6 TRAILER P&IDs REFERENCES:
 - INDOX 900-16953DIAG-1
 - KARBONSAN K180455
 - TECHNOIMPIANTI OFF229/22-PID

Rev.	Date	Description	Draft	Check'd	Approved
8	03 Apr 2026	APPROVED FOR CONSTRUCTION	TAM (JB)	TAM (MM)	LOAMPLONE
7	19 Mar 2025	APPROVED FOR CONSTRUCTION	TAM (SS)	TAM (MM)	LOAMPLONE
6	15 Jul 2024	APPROVED FOR CONSTRUCTION	TAM (SS)	TAM (MM)	LOAMPLONE
5	05 Jul 2024	APPROVED FOR CONSTRUCTION	TAM (SS)	TAM (MM)	LOAMPLONE
4	28 May 2024	APPROVED FOR CONSTRUCTION	TAM (SS)	TAM (MM)	LOAMPLONE
3	25 Jul 2023	ISSUED FOR APPROVAL	TAM (MT)	LOAMPLONE	W.BOUALAI
2	12 Dec 2022	ISSUED FOR APPROVAL	TAM (MT)	LOAMPLONE	W.BOUALAI
1	26 Jun 2022	ISSUED FOR APPROVAL	TAM (ES)	LOAMPLONE	W.BOUALAI
0	06 Jun 2022	ISSUED FOR APPROVAL	TAM (ES)	LOAMPLONE	W.BOUALAI

Customer:	MANAENERGY	Offices:	Mahaj Riad Center, Batiment 6, Jeme etage, Avenue Al Az, Hay Ryad, 10100 Rabat, Morocco
Contractor:	ITALFLUID	Offices:	VIA VALDIL4, MONTESSILVANO (ITALY) Tel.+39 085 4224374 fax+39 085 4220742
Engineering:	ITALFLUID	Offices:	VIA VALDIL4, MONTESSILVANO (ITALY) Tel.+39 085 4224374 fax+39 085 4220742
Technology Vendor:	TECHNICAL AMERICA INC	Offices:	301 N Smith Avenue, 92880 Corona, California (USA) Ph.+1 951 272 3540

TITLE:	LNG TENDRARA PLANT	OBJECT:	LNG PUMPING STATION
TYPE	SCALE	DOCUMENTS ID:	VENDOR DOC. C/ME
A1	N/A	PRO13-ING-PR23	21044-PR-PID-22001
			1/1