


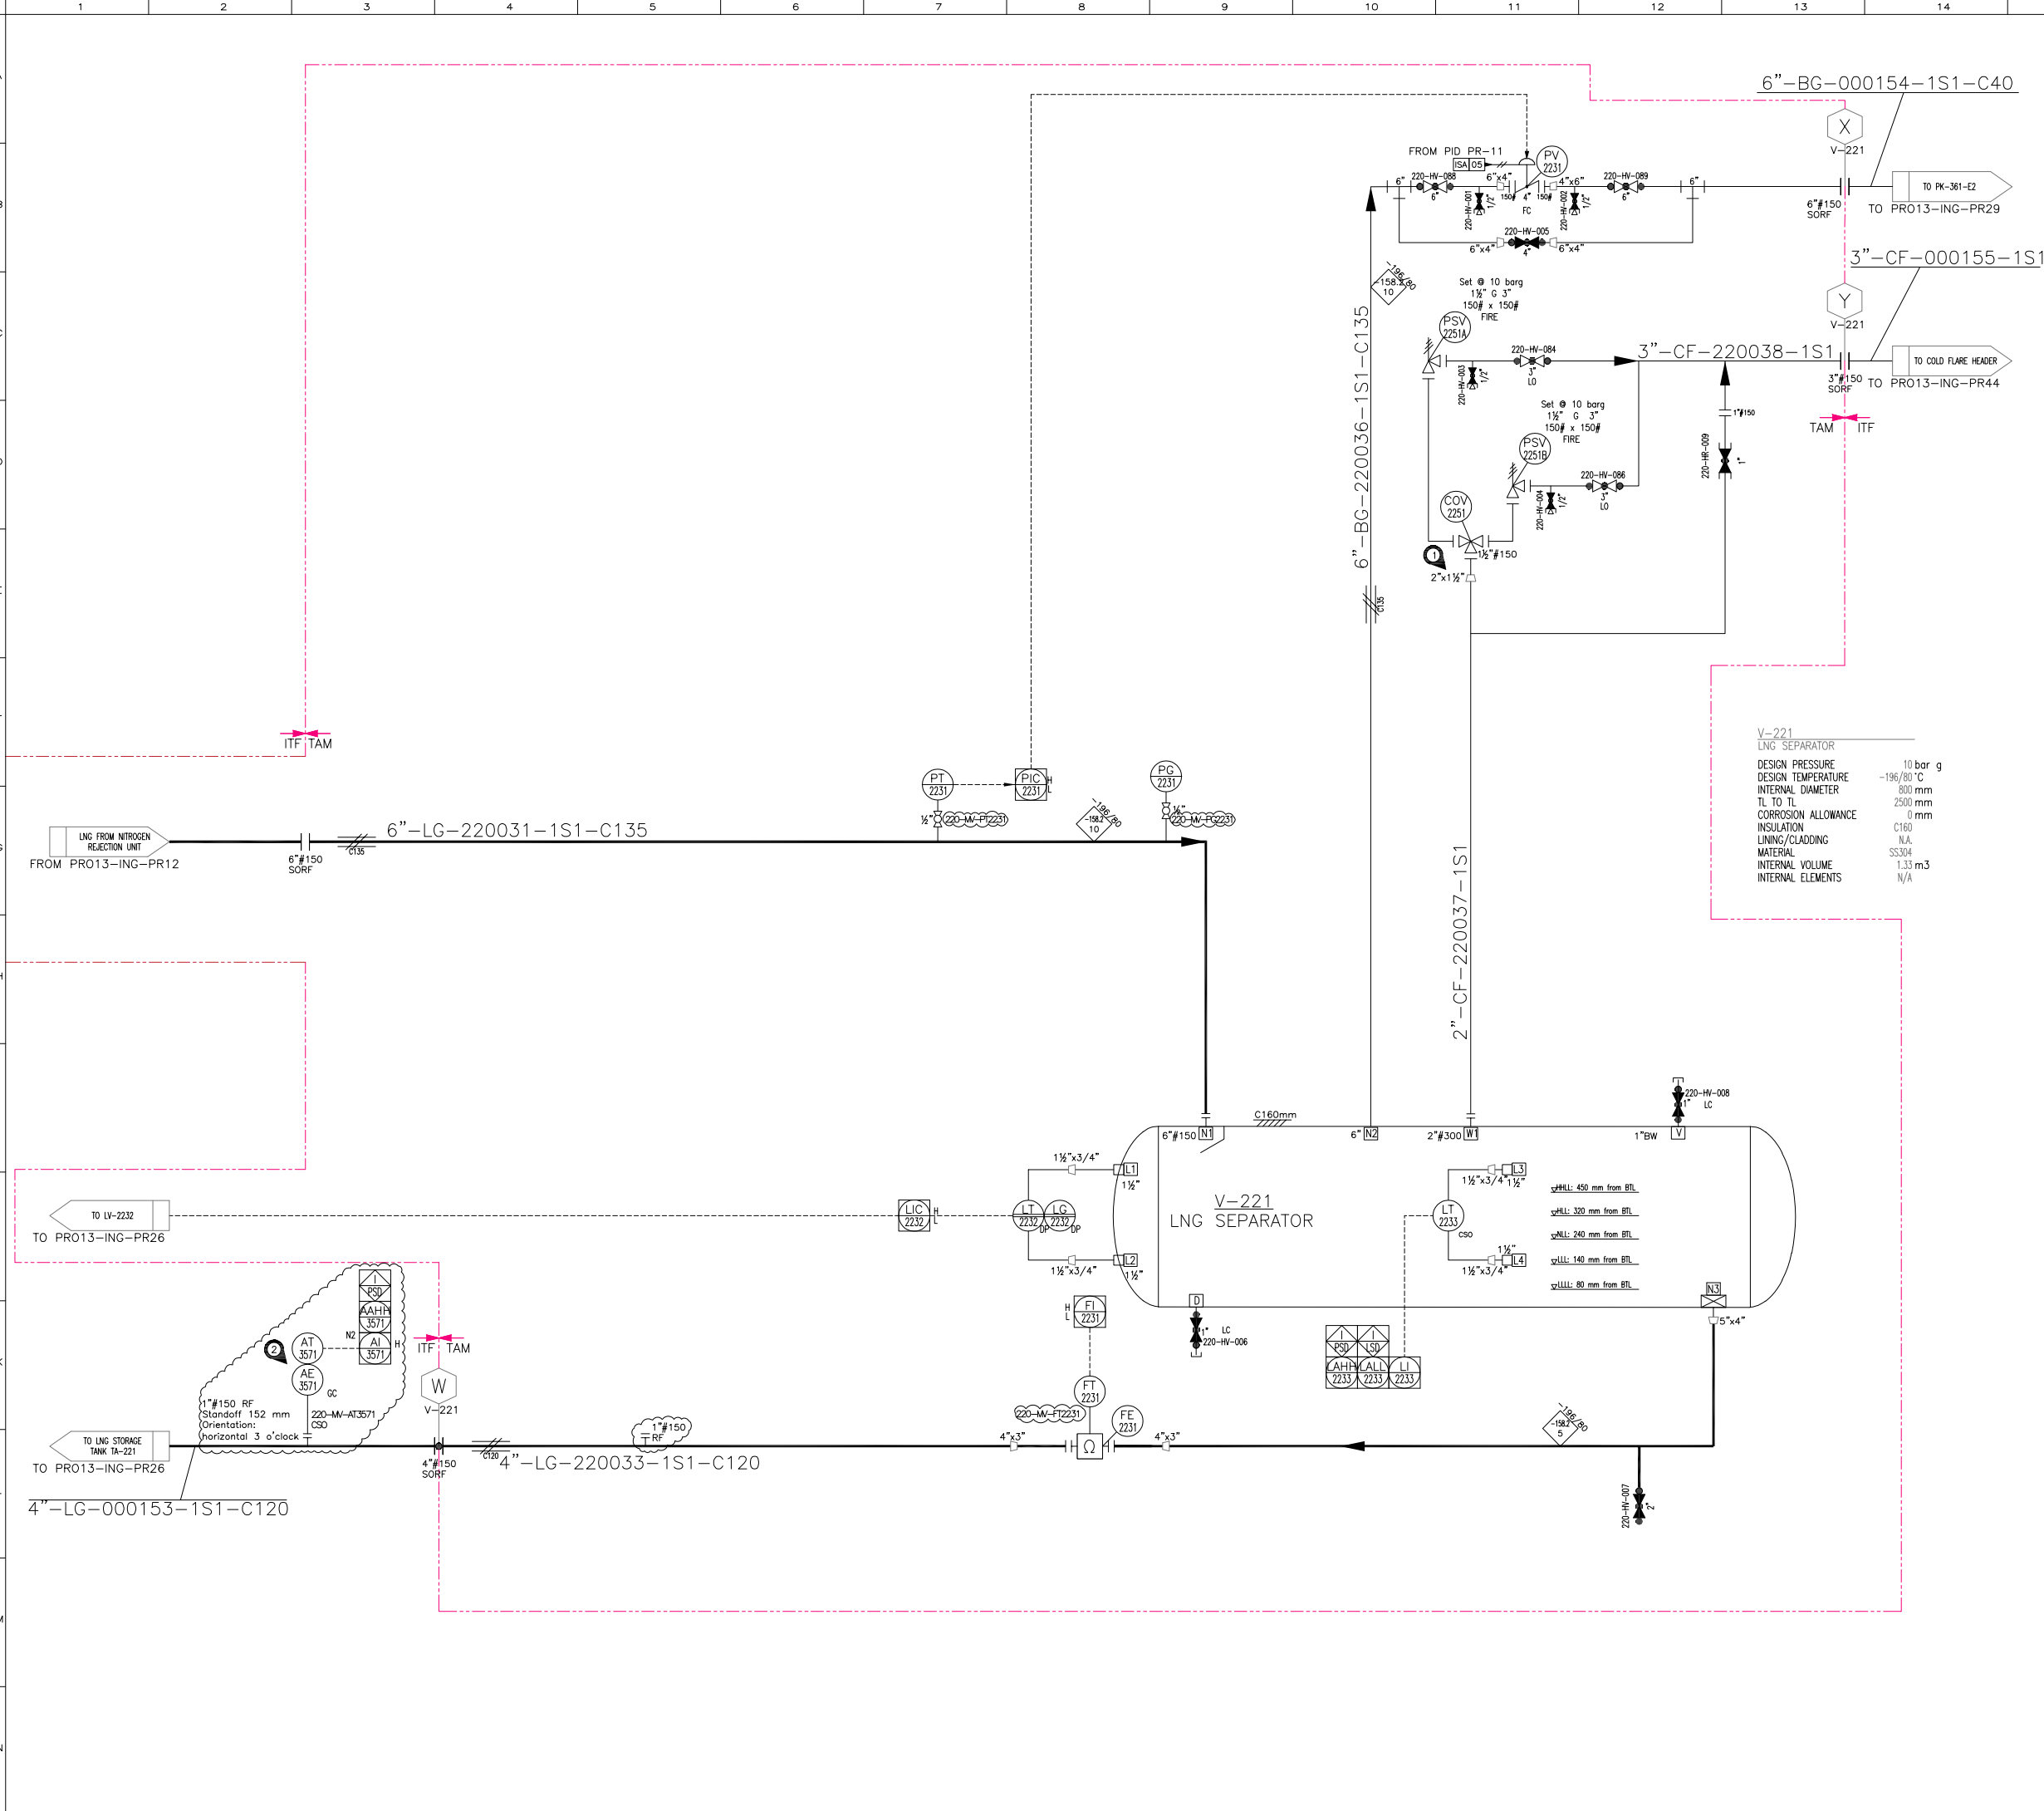

REFERENCE DOCUMENTS

P&ID LEGEND	PRO13-ING-PRO0
PROCESS FLOW DIAGRAM	21044-PR-PID-00000
UTILITY FLOW DIAGRAM	PRO10-ING-PRO1/02/03/04
MATERIAL SELECTION DIAGRAM	21044-PR-PFD-00001
NOTES	PRO10-ING-PR11
	21044-PR-UFD-00001
	PRO08-ING-FR01
	21044-PR-MSD-00001

1

CHANGE OVER VALVE WITH LOCK DEVICE

2

SAME ANALYZER AS AT-3581

TAM SUPPLY LIMIT

7	25 Mar 2026	ISSUE FOR COMMISSIONING	TAM (JB)	TAM (MM)	LOAMPLONE
6	19 Jan 2026	AS BUILT	TAM (JB)	LOAMPLONE	W.BOUALAI
5	20 Mar 2025	REVISED WHERE INDICATED	TAM (LD)	LOAMPLONE	W.BOUALAI
4	24 Jun 2024	APPROVED FOR CONSTRUCTION	TAM (LD)	LOAMPLONE	W.BOUALAI
3	25 Jul 2023	ISSUED FOR APPROVAL	TAM (LD)	LOAMPLONE	W.BOUALAI
2	02 Nov 2022	ISSUED FOR APPROVAL	TAM (LD)	LOAMPLONE	W.BOUALAI
1	25 Jul 2022	ISSUED FOR APPROVAL	TAM (LD)	LOAMPLONE	W.BOUALAI
0	06 Jun 2022	ISSUED FOR APPROVAL	TAM (MT)	LOAMPLONE	W.BOUALAI

Customer:

MANAENERGY

Contractor:

ITALFLUID

Engineering:

ITALFLUID

Technology Vendor:

TECHNICAL AMERICA INC

OFFICES:

Mahaj Riad Center, Batiment 6, 3eme etage, Avenue Al Az, Hay Ryad, 10100 Rabat, Morocco

OFFICES:

VIA VVALDI,4 MONTESILVANO (ITALY)

Tel.+39 085 4224374 fax+39 085 4220742

OFFICES:

VIA VVALDI,4 MONTESILVANO (ITALY)

Tel.+39 085 4224374 fax+39 085 4220742

OFFICES:

301 N Smith Avenue, 92880 Corona, California (USA)

Ph.+1 951 272 9540

TITLE:

LNG TENDRARA PLANT

OBJECT:

UNIT 220

LNG SEPARATOR V-221

TYPE	SCALE	DOCUMENTS ID:	VENDOR DOC CODE:	SHEET/OF
A1	N/A	PRO13-ING-PR25	21044-PR-PID-22003	1/1

Documento di proprieta' aziendale. La Societa' tutelera' i propri diritti a termine di legge. This document is Company property. The Company lawfully reserves all rights.