


TA-221
LNG STORAGE TANK

DESIGN PRESSURE IN -0.005/0.2 / OUT -0.005/0.005 barg
DESIGN TEMPERATURE IN -196°C / OUT -15/47°C
INTERNAL DIAMETER int19500/ex121800 mm
TOTAL HEIGHT int23242/ex25342 mm
CORROSION ALLOWANCE 0 mm
INSULATION PERLITE
LINING/CLADDING N.A.
MATERIAL S3304
INTERNAL VOLUME 6200 m3
TYPE FIXED ROOF DOUBLE WALLED LNG TANK

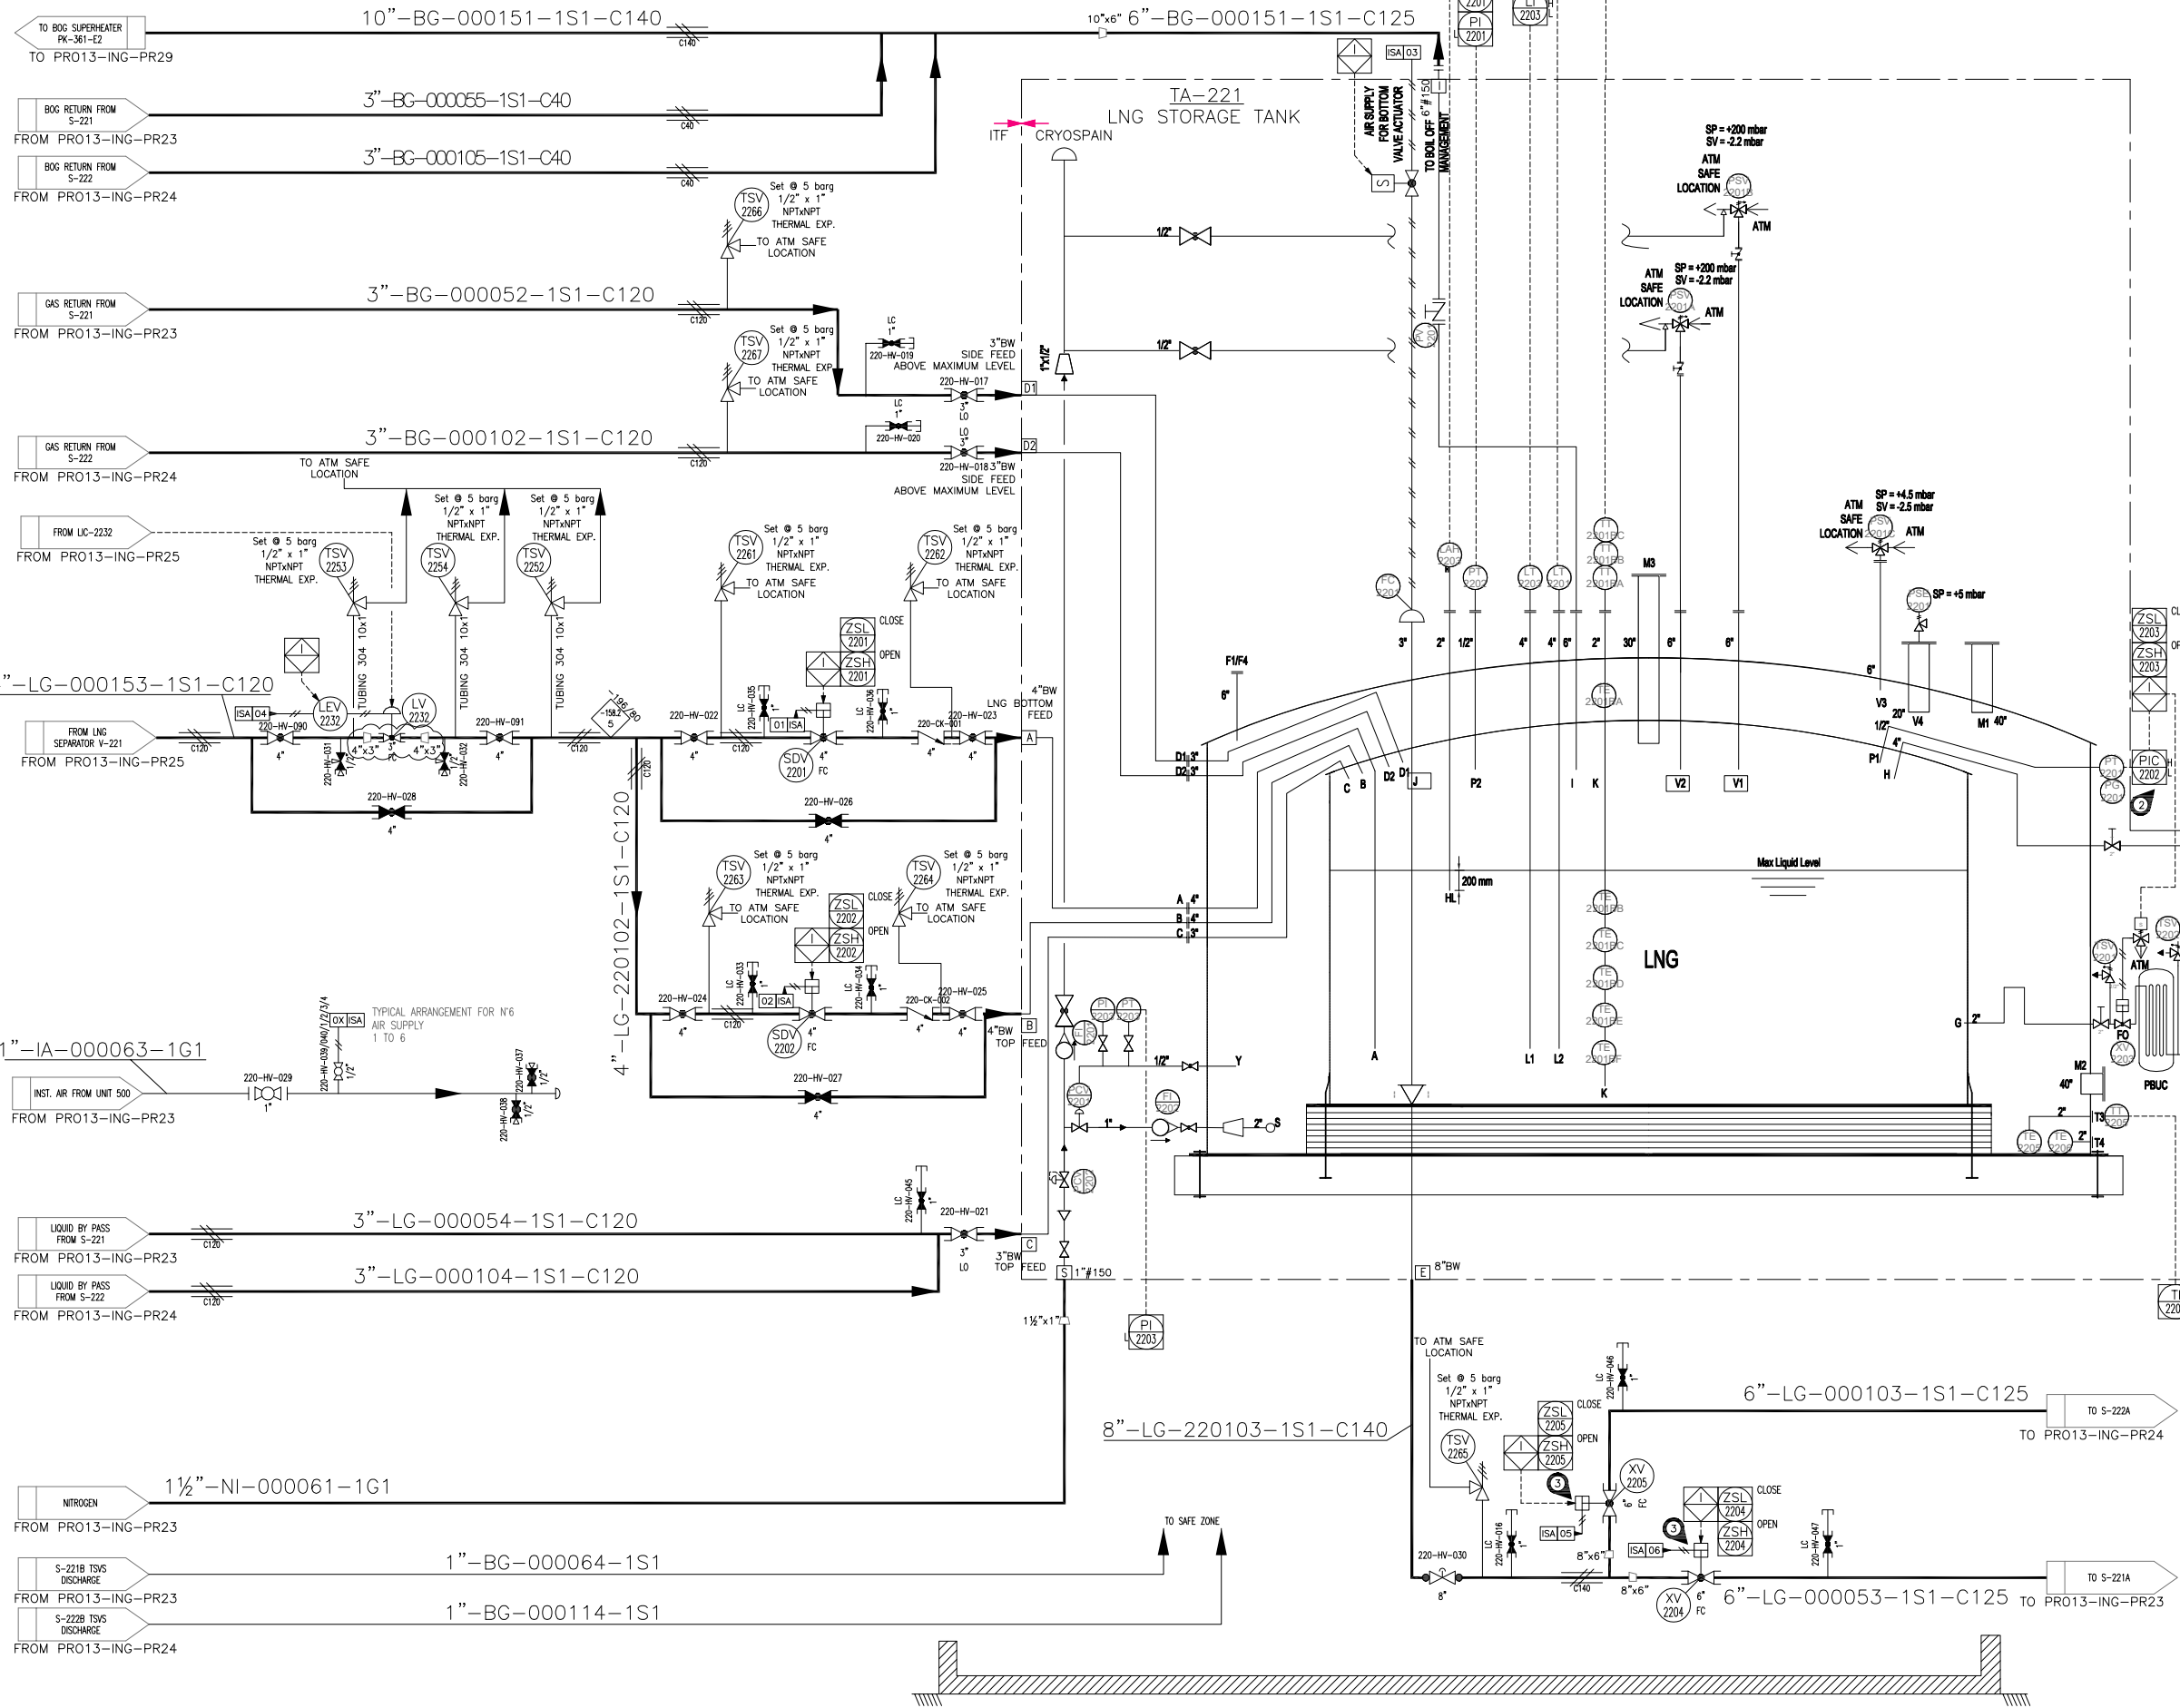

REFERENCE DOCUMENTS

P&ID LEGEND	PRO13-ING-PRO0
PROCESS FLOW DIAGRAM	21044-PR-PID-00000
UTILITY FLOW DIAGRAM	PRO10-ING-PR01/02/03/04
MATERIAL SELECTION DIAGRAM	21044-PR-PFD-00001
	PRO10-ING-PR11
	21044-PR-UFD-00001
	PRO08-ING-PR01
	21044-PR-MSD-00001

ISA 03 INSTRUMENT SUPPLY AIR

V 03 VENT

NOTES

- DELETED
- LOW PRESSURE CONTROL WITH VAPORIZER BY VENDOR.
- XV-2204 AND XV-2205 SHALL BE AS CLOSE AS POSSIBLE TO THE MAIN 8" COLLECTOR TEE.

6	03 Apr 2026	APPROVED FOR CONSTRUCTION	TAM (JB)	TAM (MM)	LOAMPLONE
5	15 Oct 2025	APPROVED FOR CONSTRUCTION	TAM (LD)	LOAMPLONE	W.BOUALAI
4	08 Feb 2024	APPROVED FOR CONSTRUCTION	TAM (LD)	LOAMPLONE	W.BOUALAI
3	18 Aug 2023	ISSUED FOR APPROVAL	TAM (ES)	LOAMPLONE	W.BOUALAI
2	02 Nov 2022	ISSUED FOR APPROVAL	TAM (ES)	LOAMPLONE	W.BOUALAI
1	25 Jul 2022	ISSUED FOR APPROVAL	TAM (ES)	LOAMPLONE	W.BOUALAI
0	06 Jun 2022	ISSUED FOR APPROVAL	TAM (ES)	LOAMPLONE	W.BOUALAI
Rev.	Date	Description	Draft	Check'd	Approved
Customer: MANAENERGY			OFFICES: Mahaj Riad Center, Batiment 6, 3eme etage, Avenue Al Arz, Hay Riad, 10100 Rabat, Morocco		
Contractor: ITALFLUID			OFFICES: VIA VIVALDI,4 MONTESILVANO (ITALY) Tel.+39 085 4224374 fax+39 085 4220742		
Engineering: ITALFLUID			OFFICES: VIA VIVALDI,4 MONTESILVANO (ITALY) Tel.+39 085 4224374 fax+39 085 4220742		
Technology Vendor: TECHNICAL AMERICA INC			OFFICES: 301 N Smith Avenue, 92880 Corona, California (USA) Ph.+1 951 272 9540		
TITLE: LNG TENDRARA PLANT			OBJECT: UNIT 220 LNG STORAGE TANK TA-221		
TYPE	SCALE	DOCUMENTS ID:	VENDOR DOC. CODE		SHEET/OF
A1	N/A	PRO13-ING-PR26	21044-PR-PID-22004		1/1