


PK-361-E2
BOG SUPERHEATER - BEU TYPE

DESIGN DUTY 74.9 kW
DESIGN PRES. SHELL PV / 10 bar g
DESIGN TEMP. SHELL -196/60 °C
DESIGN PRES. TUBE PV / 15 bar g
DESIGN TEMP. TUBE -196/120 °C
SHELL DIAMETER 14" NPS
TUBE LENGTH 3000 mm
CORR. ALL. SHELL/TUBE 0 mm
INSULATION C150 (on shell only)
MATERIAL SHELL SIDE SS304
MATERIAL TUBE SIDE SS304
SURFACE AREA 13.5 m2

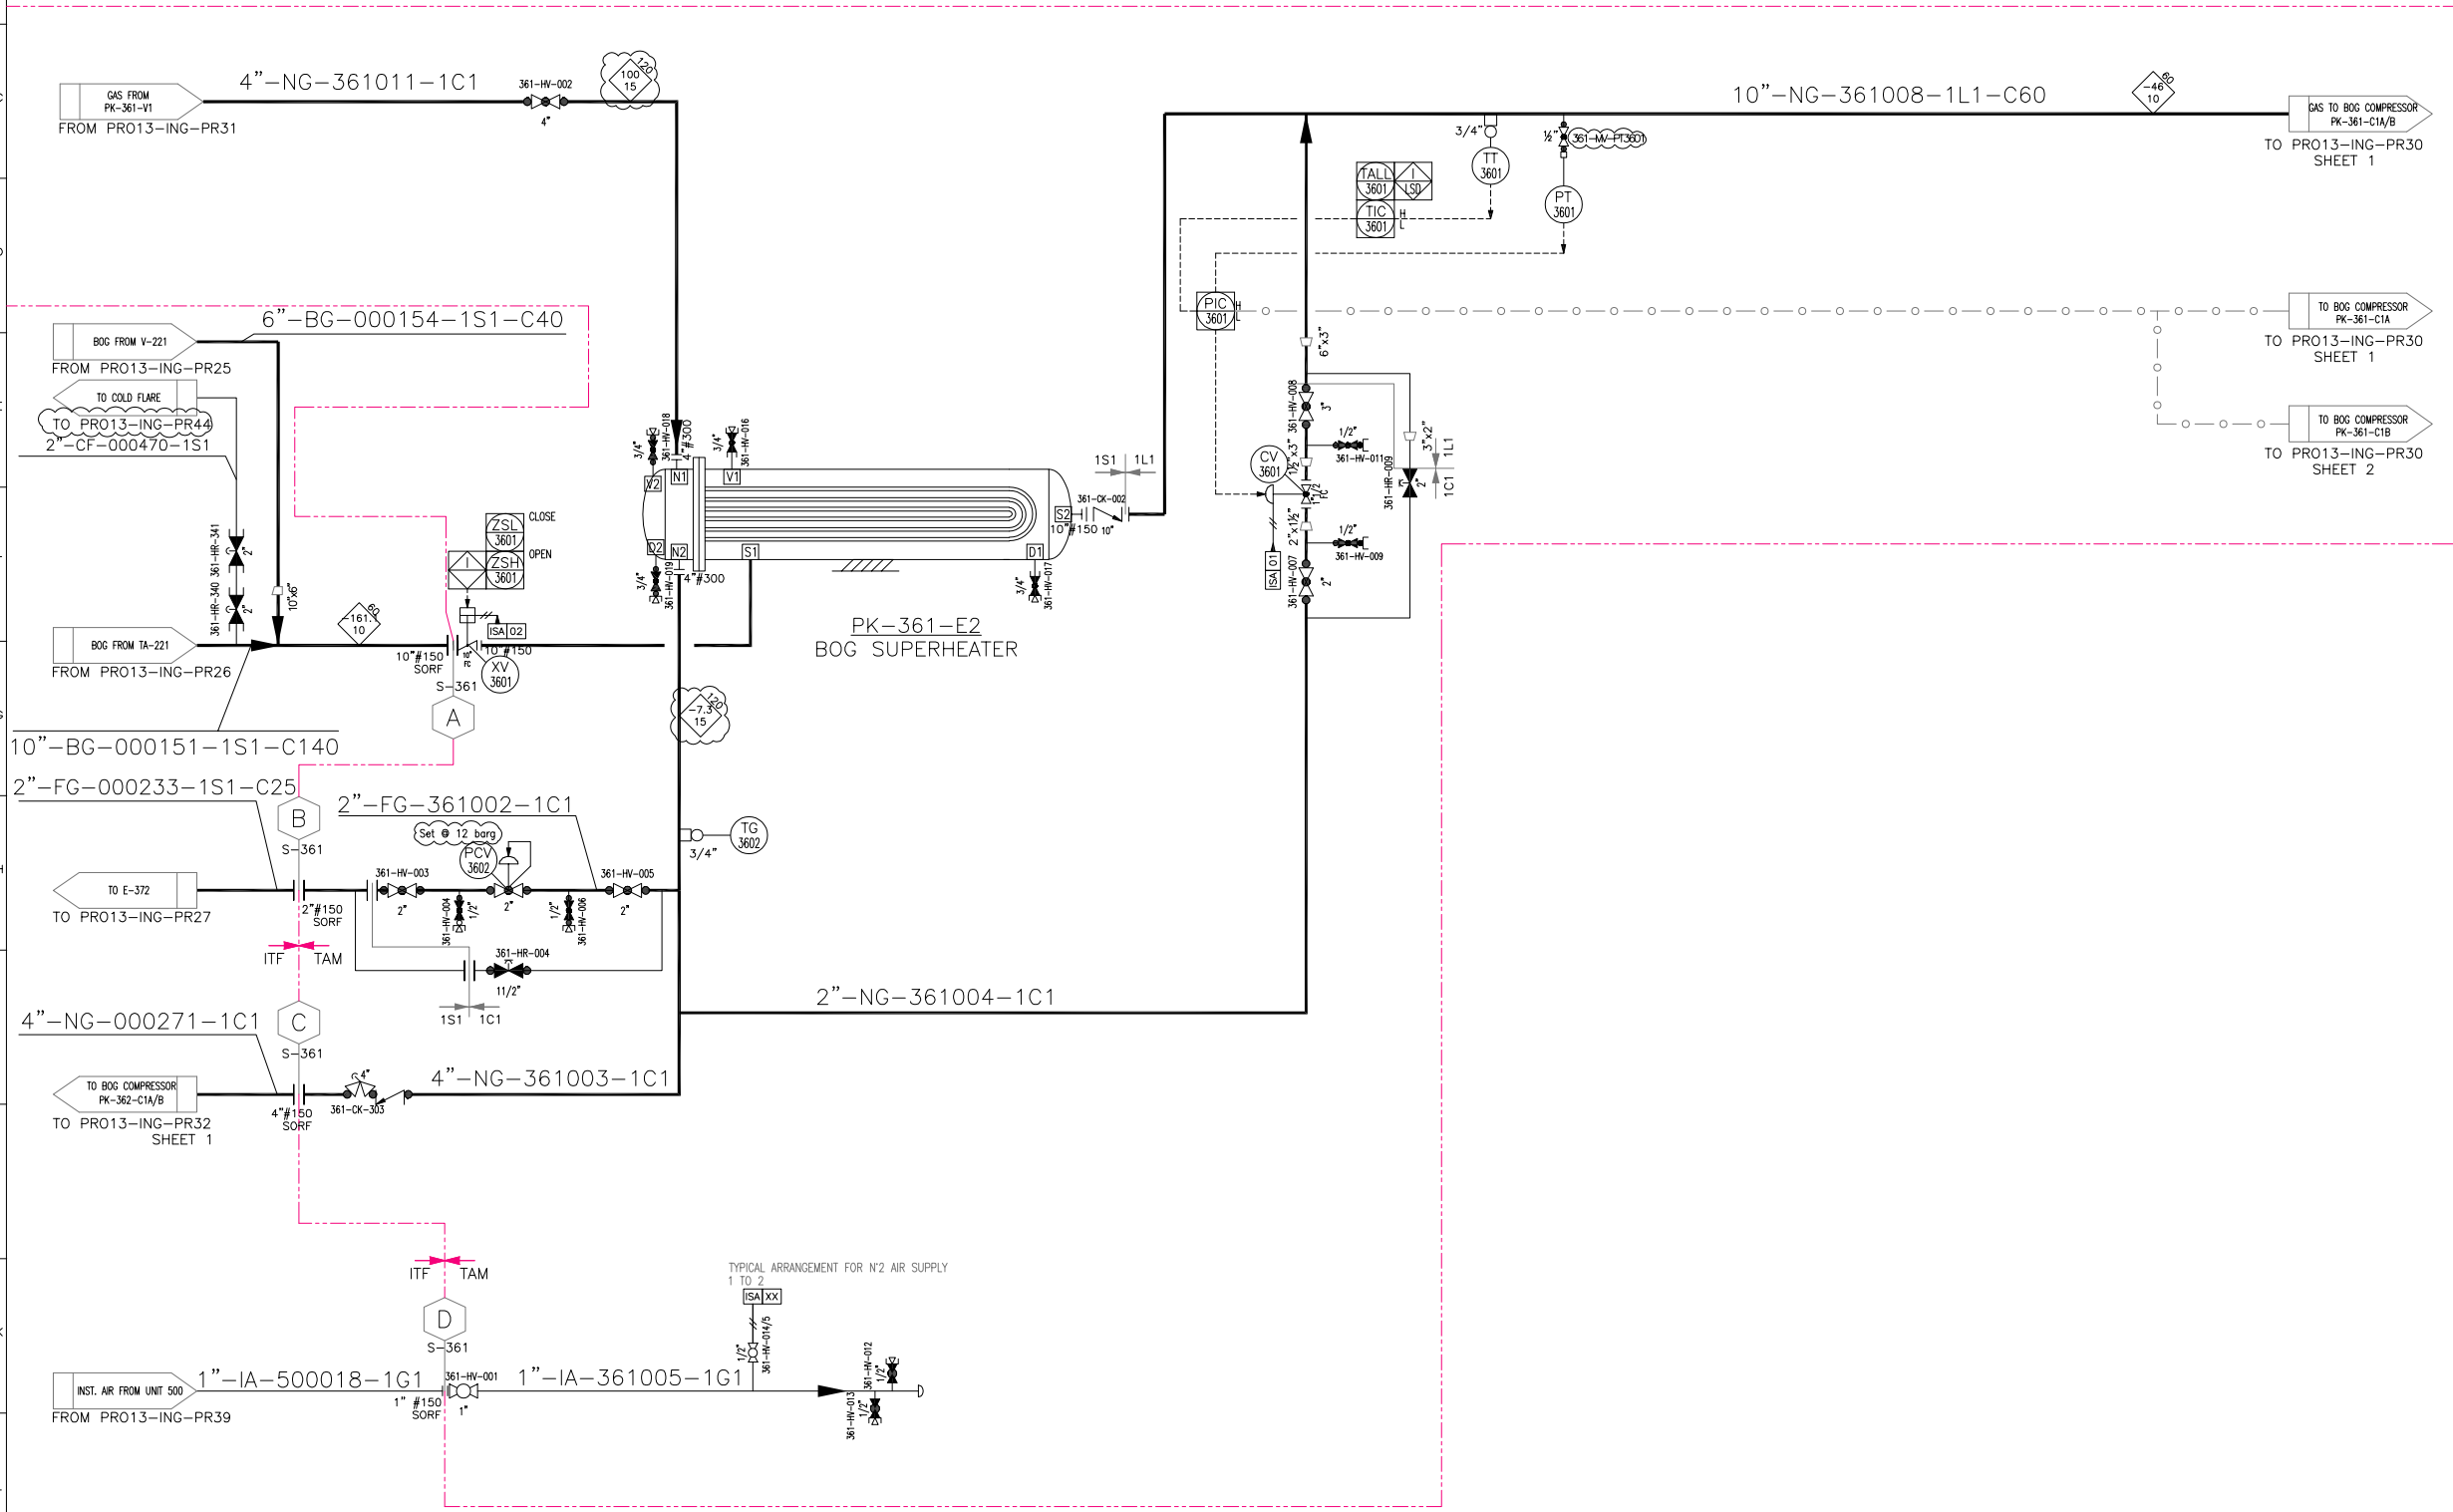

REFERENCE DOCUMENTS

P&ID LEGEND	PRO13-ING-PRO0 21044-PR-PID-00000
PROCESS FLOW DIAGRAM	PRO10-ING-PRO1/02/03/04 21044-PR-PFD-00001
UTILITY FLOW DIAGRAM	PRO10-ING-PR11 21044-PR-UFD-00001
MATERIAL SELECTION DIAGRAM	PRO08-ING-FR01 21044-PR-MSD-00001

ISA 0X INSTRUMENT SUPPLY AIR

4	25 Mar 2025	AS BUILT	TAM (JB)	TAM (MM)	LCAMPLONE
3	04 Apr 2025	ISSUED FOR APPROVAL	TAM (JB)	LCAMPLONE	W.BOUJALI
2	25 Jan 2024	ISSUED FOR APPROVAL	TAM (ES)	LCAMPLONE	W.BOUJALI
1	08 Nov 2022	ISSUED FOR APPROVAL	TAM (ES)	LCAMPLONE	W.BOUJALI
0	20 Jul 2022	ISSUED FOR APPROVAL	TAM (ES)	LCAMPLONE	W.BOUJALI

Rev.	Date	Description	Draft	Check'd	Approved
------	------	-------------	-------	---------	----------

Customer:	MANAENERGY	OFFICES:	Mahaj Riad Center, Batiment 6, 3eme etage, Avenue Al Arz, Hay Ryad, 10100 Rabat, Morocco
Contractor:	ITALFLUID	OFFICES:	VIA VIVALDI,4 MONTESILVANO (ITALY) Tel.+39 085 4224374 fax+39 085 4220742
Engineering:	ITALFLUID	OFFICES:	VIA VIVALDI,4 MONTESILVANO (ITALY) Tel.+39 085 4224374 fax+39 085 4220742
Technology Vendor:	TECHNICAL AMERICA INC	OFFICES:	301 N Smith Avenue, 92880 Corona, California (USA) Ph.+1 951 272 9540

TITLE: LNG TENDRARA PLANT			OBJECT: P&ID PK-361-E2 (UNIT 360)	
TYPE	SCALE	DOCUMENTS ID:	VENDOR DOC. CODE	SHEET
A1	N/A	PRO13-ING-PR29	21044-PR-PID-36001	1/