


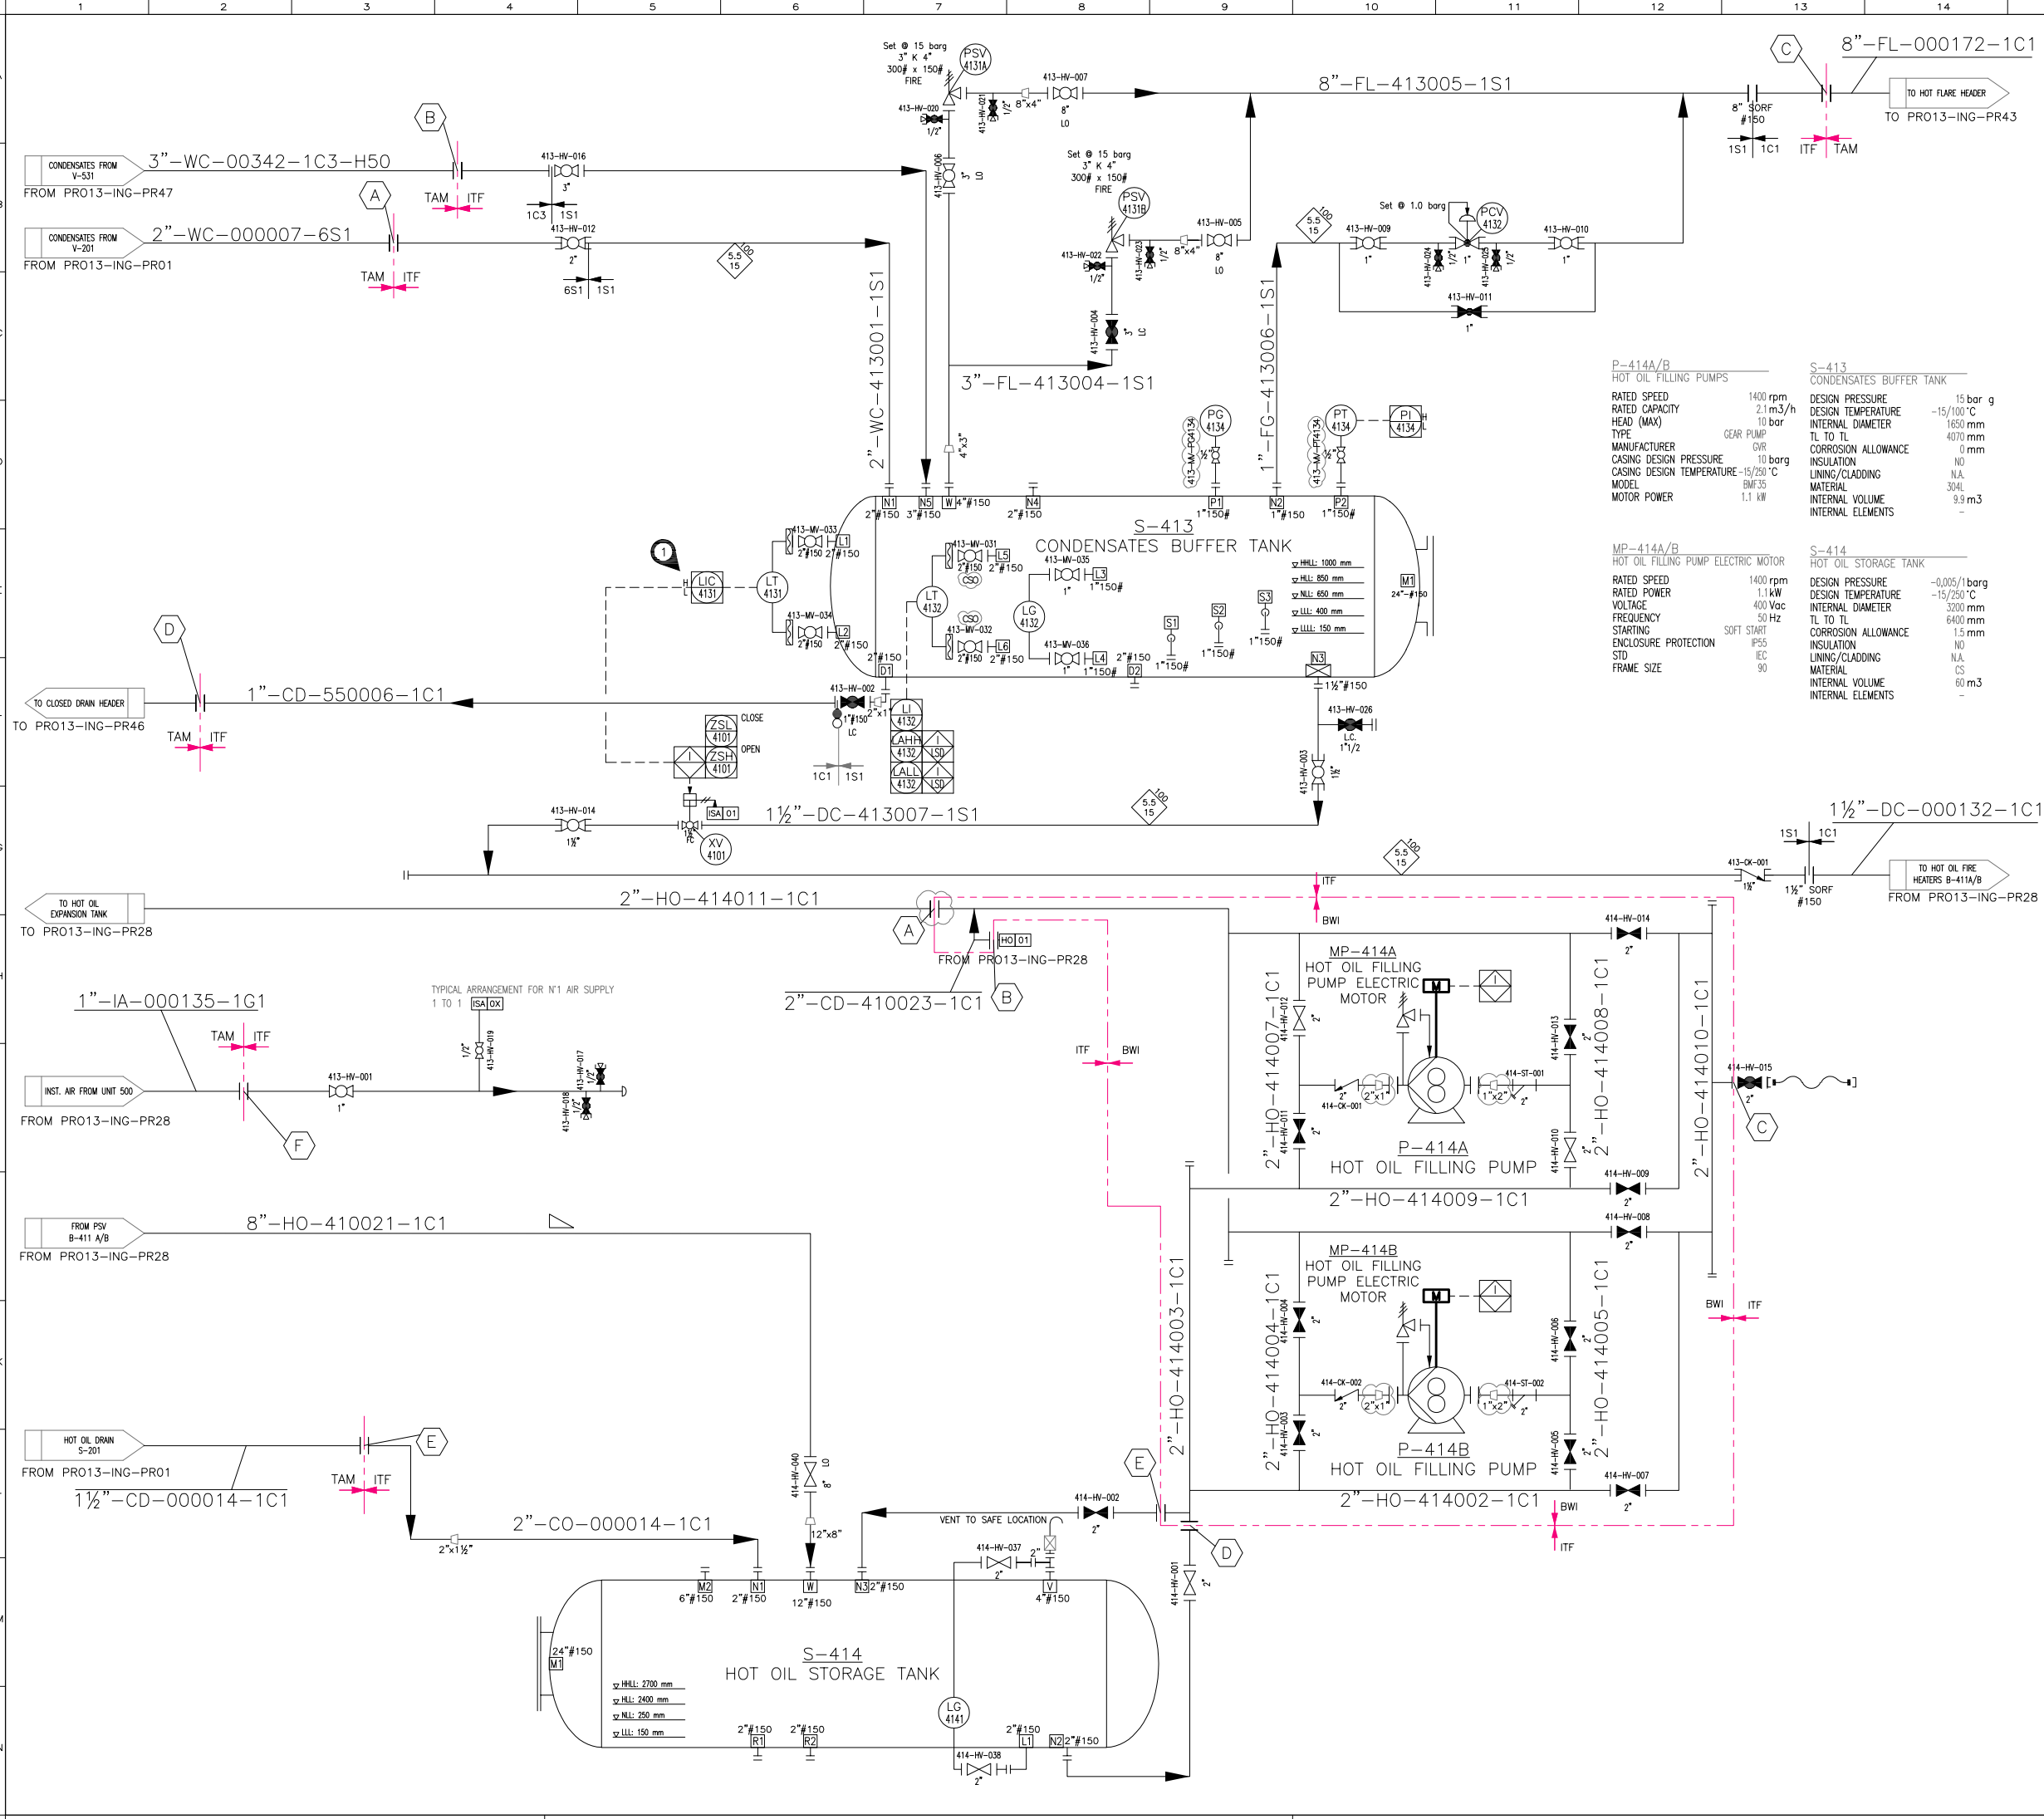

REFERENCE DOCUMENTS	
P&ID LEGEND	PRO13-ING-PR00 21044-PR-PID-00000
PROCESS FLOW DIAGRAM	PRO10-ING-PR01/02/03/04 21044-PR-PFD-00001
UTILITY FLOW DIAGRAM	PRO10-ING-PR05 21044-PR-UFD-00001
MATERIAL SELECTION DIAGRAM	PRO08-ING-FR01 21044-PR-MSD-00001

INSTRUMENT SUPPLY AIR	
NOTES:	
LIC WILL PROVIDE SIGNAL TO HOT OIL BOILERS IN ORDER TO CHECK AVAILABILITY OF CONDENSATE AND START FUEL GAS TO MAINTAIN REQUIRED BOILER RATE IN CASE OF LOW CONDENSATE LEVEL.	

Customer: MANAENERGY		Offices: Mahaj Riad Center, Batiment 6, 3eme etage, Avenue Al Az, Hay Ryad, 10100 Rabat, Morocco	
Contractor: ITALFLUID		Offices: VIA VIVALDI,4 MONTESILVANO (ITALY) Tel.+39 085 4224374 fax+39 085 4220742	
Engineering: ITALFLUID		Offices: VIA VIVALDI,4 MONTESILVANO (ITALY) Tel.+39 085 4224374 fax+39 085 4220742	
Technology Vendor: TECHNICAL AMERICA INC		Offices: 301 N Smith Avenue, 92880 Corona, California (USA) Ph.+1 951 272 9540	
TITLE: LNG TENDRARA PLANT		OBJECT: HOT OIL UNIT UNIT 410	
TYPE	SCALE	DOCUMENTS ID:	VENDOR DOC. CODE
A1	N/A	PRO13-ING-PR40	21044-PR-PID-41002
			SHEET/OF 1/1