


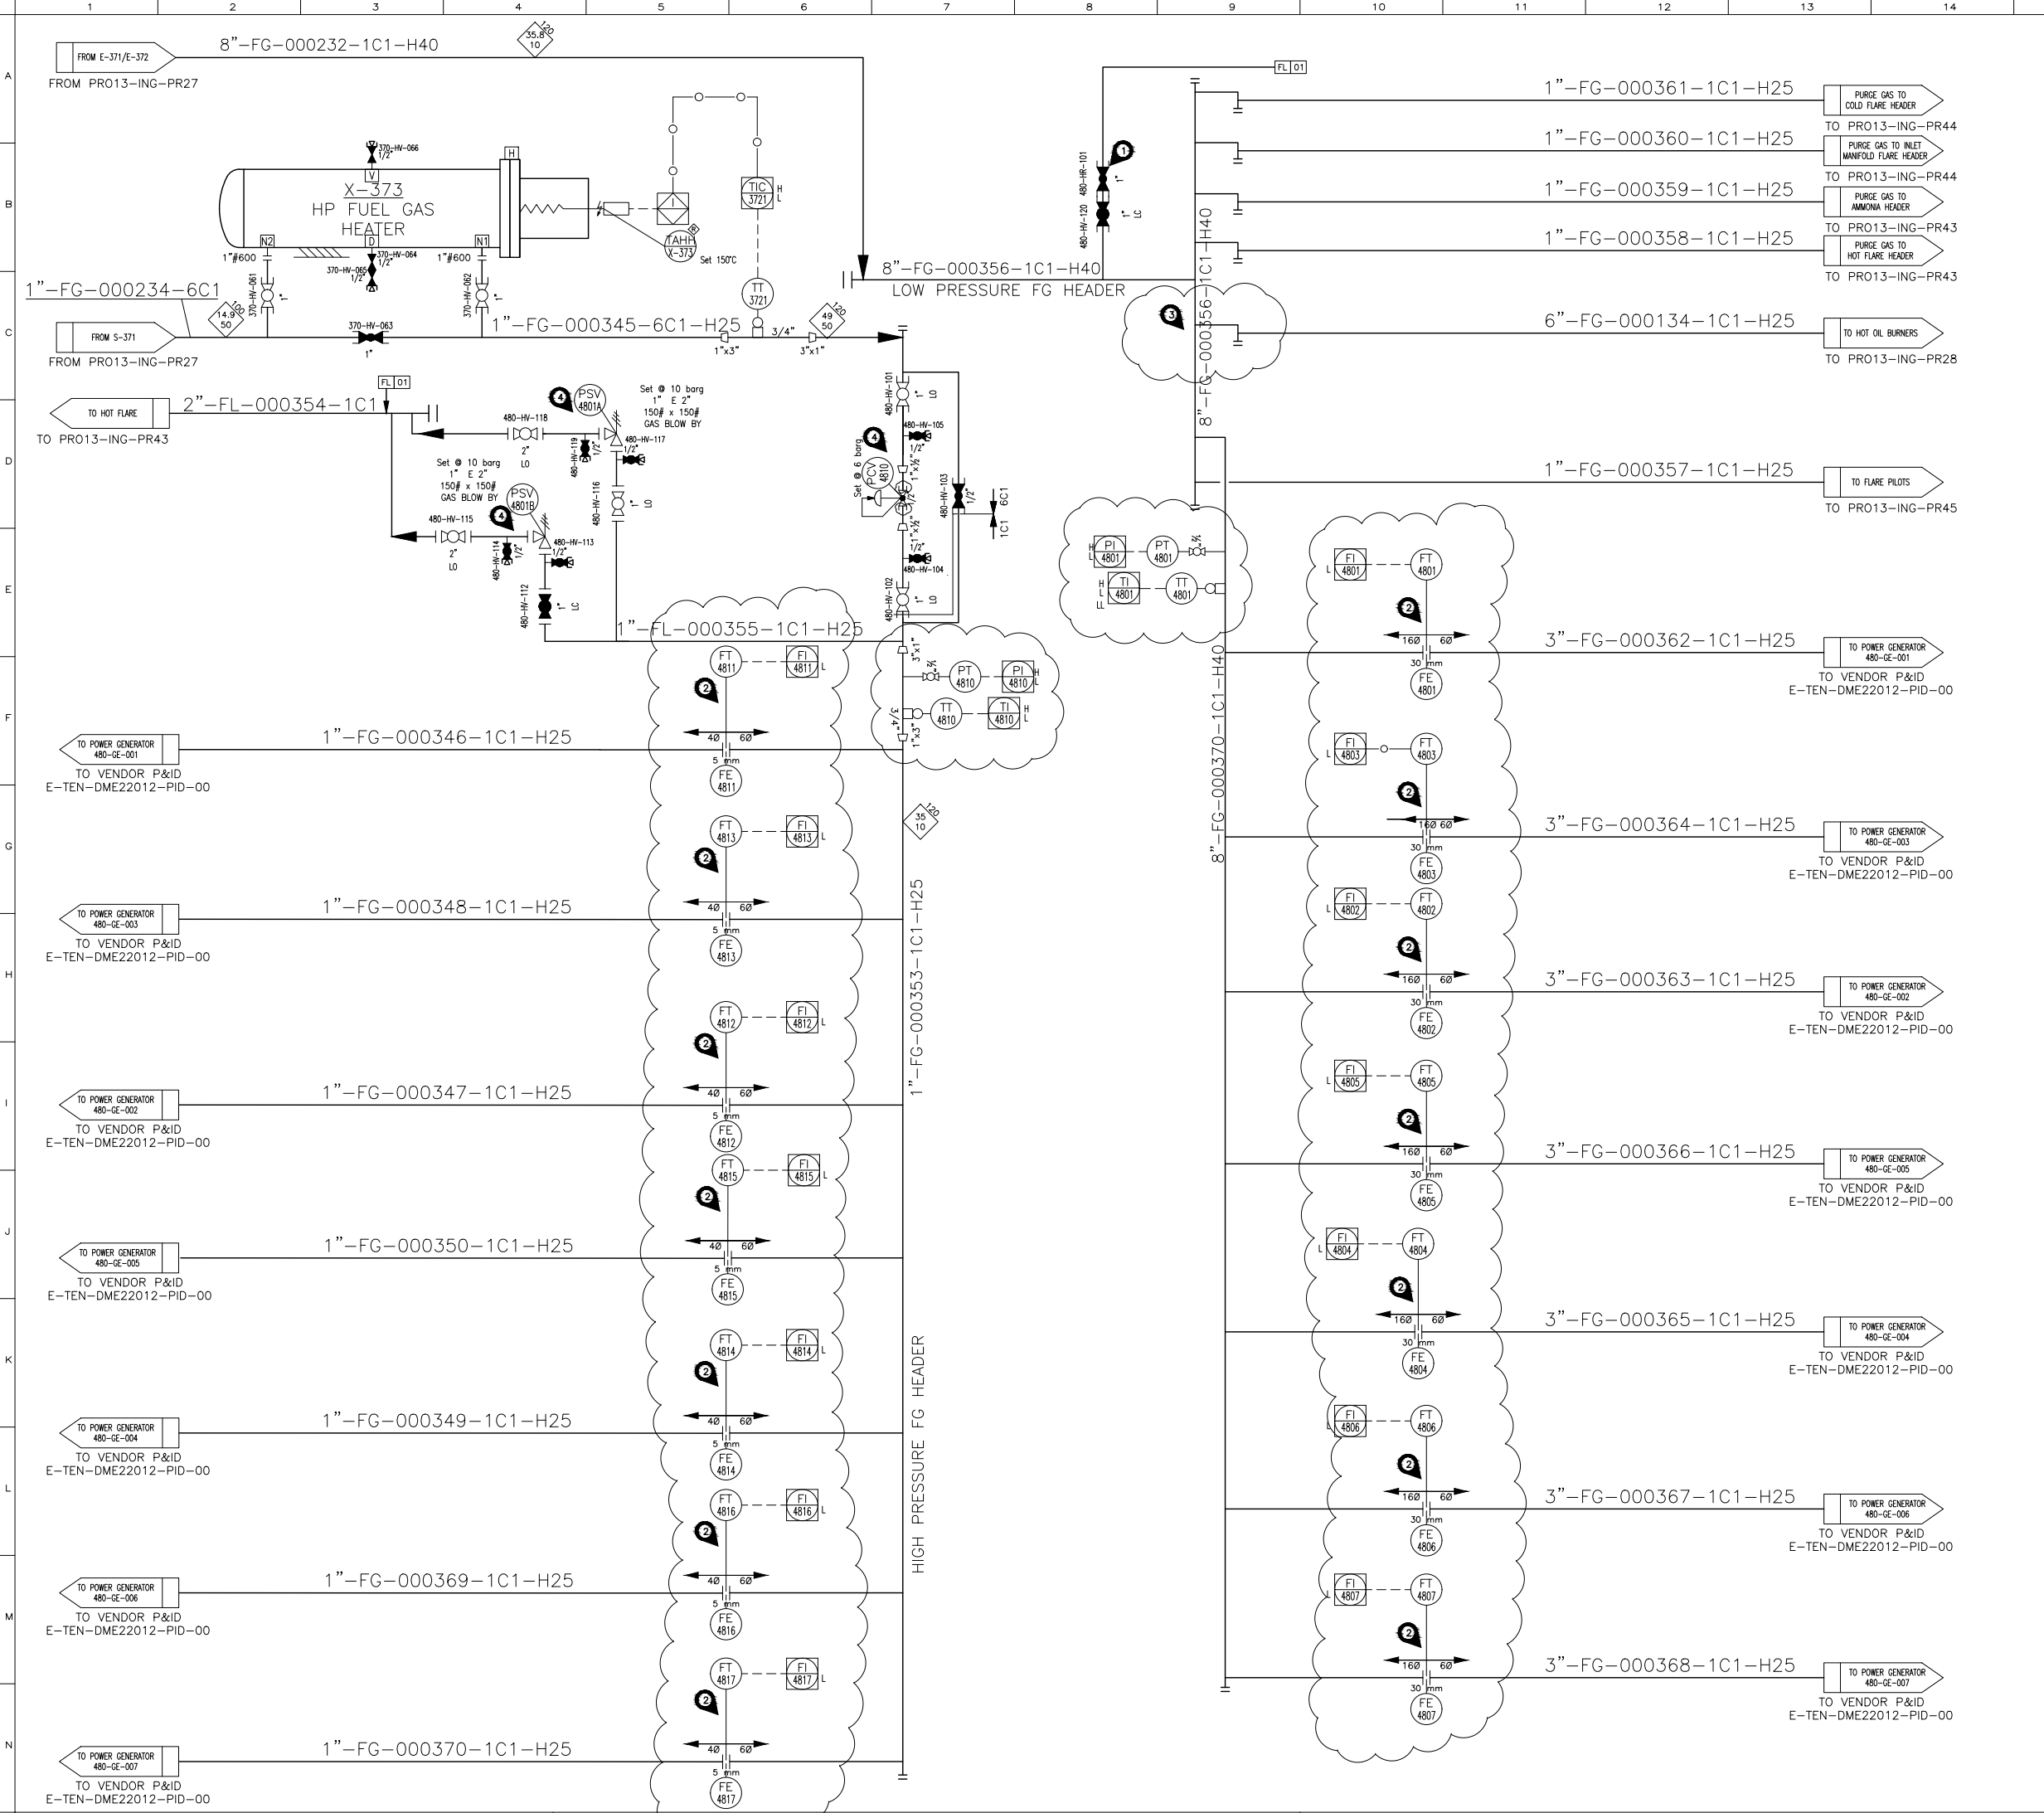

15		16		17		18									
REFERENCE DOCUMENTS															
P&ID LEGEND				PRO13-ING-PRO0 21044-PR-PID-00000											
PROCESS FLOW DIAGRAM				PRO10-ING-PRO1/02/03/04 21044-PR-PFD-00001											
MATERIAL SELECTION DIAGRAM				PRO08-ING-FR01 21044-PR-MSD-00001											
NOTES 1 OPERATOR SHALL SEND GAS TO FLARE FOR AFTER PLANT SHUT DOWN IN WINTER SEASON. 2 COMPACT CONDITIONING ORIFICE PLATE FLOW METER 3 METHANE SAMPLING POINT 4 PSVs TO BE RECALCULATED IF PCV CV IS HIGHER THAN 1. X-373 HP FUEL GAS HEATER DESIGN PRESSURE50 bar g DESIGN TEMPERATURE-15/120 °C DIAMETER4" NPS TOTAL1300 mm CORROSION ALLOWANCE1.5 mm INSULATIONH (60 mm) LINING/CLADDINGN/A MATERIAL (BODY)CS RATED POWER3 kW SUPPLY VOLTAGE690Vac-50Hz-3															
								725 Mar 2025APPROVED FOR CONSTRUCTIONITFLCAMPLONEW. BOULALI							
								614 Oct 2024APPROVED FOR CONSTRUCTIONTAM (LD)LCAMPLONEW. BOULALI							
								524 June 2024APPROVED FOR CONSTRUCTIONTAM (LD)LCAMPLONEW. BOULALI							
								418 Aug 2023ISSUED FOR APPROVALTAM (LD)LCAMPLONEW. BOULALI							
								32 Nov 2022ISSUED FOR APPROVALTAM (LD)LCAMPLONEW. BOULALI							
								226 July 2022ISSUED FOR APPROVALTAM (ES)LCAMPLONEW. BOULALI							
								18 July 2022ISSUED FOR APPROVALTAM (ES)LCAMPLONEW. BOULALI							
								015 June 2022ISSUED FOR APPROVALTAM (ES)LCAMPLONEW. BOULALI							
								Rev.		Date		Description		DraftCheck'd (ITF)App'r's (MSP)SOUND ENERGY	
										Customer:		SOUND ENERGY		OFFICES: Espace les Patios 1st floor, Avenue Annakhil Hay Riad, Rabat 10100	
										Contractor:		ITALFLUID		OFFICES: Regus Maroc Twin Center, Tour Ouest, Casablanca Tel: +213/ 29 73 31 91 Fax: +213/ 29 73 18 92	
										Engineering:		ITALFLUID		OFFICES: VIA VIVALDI,4 MONTESILVANO (ITALY) Tel: +39 085 4224374 fax: +39 085 4220742	
										Technology Vendor:		TECHNICAL AMERICA INC		OFFICES: Ph: +1 951 272 9540 Corona, California (USA)	
								TITLE: LNG TENDRARA PLANT				OBJECT: P&ID FUEL GAS DISTRIBUTION			
								TYPE		SCALE		DOCUMENTS ID:		VENDOR DOC. CODE	
								A1		N/A		PRO13-ING-PR41		21044-PR-PID-42001	
						SHEET/OF 1/1									