


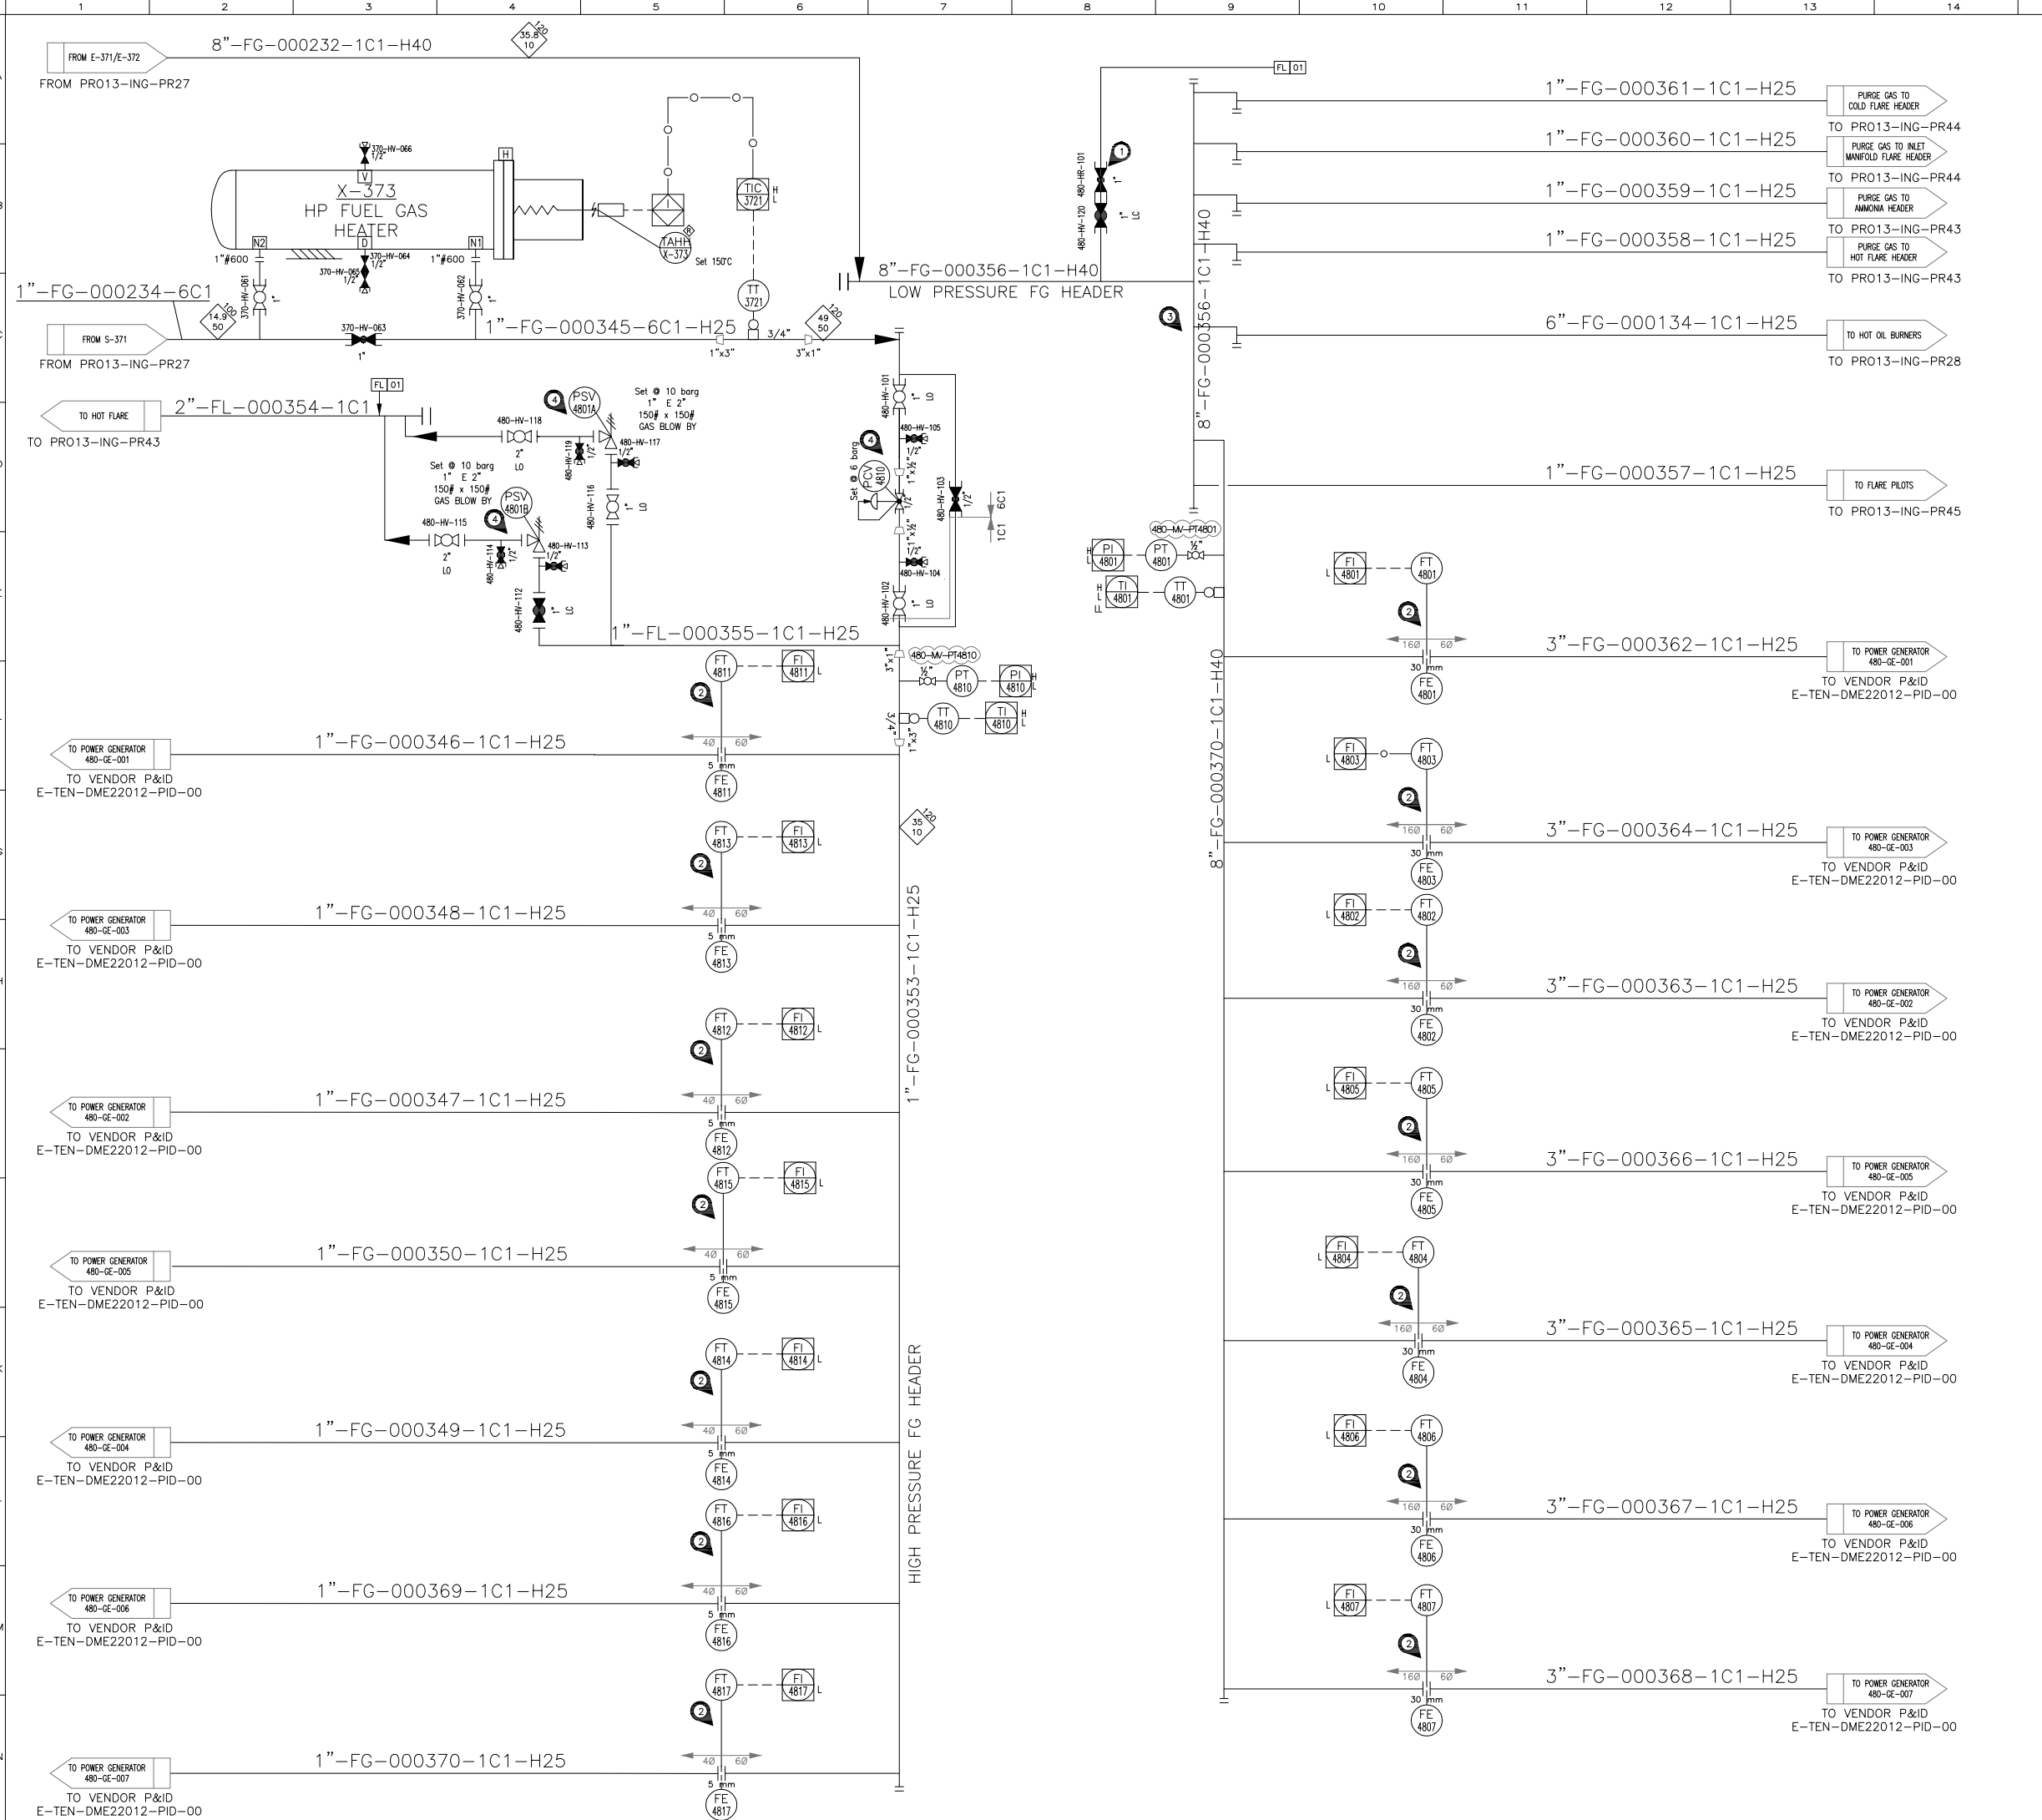

REFERENCE DOCUMENTS

P&ID LEGEND	PRO13-ING-PR00 21044-PR-PID-00000
PROCESS FLOW DIAGRAM	PRO10-ING-PR01/02/03/04 21044-PR-PFD-00001
MATERIAL SELECTION DIAGRAM	PRO08-ING-FR01 21044-PR-MSD-00001

NOTES

1

OPERATOR SHALL SEND GAS TO FLARE FOR AFTER PLANT SHUT DOWN IN WINTER SEASON.

2

COMPACT CONDITIONING ORIFICE PLATE FLOW METER

3

METHANE SAMPLING POINT

4

PSVs TO BE RECALCULATED IF PCV CV IS HIGHER THAN 1.

X-373
HP FUEL GAS HEATER

DESIGN PRESSURE50 bar g
DESIGN TEMPERATURE-15/120 °C
DIAMETER4" NPS
TOTAL1300 mm
CORROSION ALLOWANCE1.5 mm
INSULATIONH (60 mm)
LINING/CLADDINGN.A.
MATERIAL (BODY)CS
RATED POWER3 kW
SUPPLY VOLTAGE690Vac-50Hz-3

8	03 Apr 2026	APPROVED FOR CONSTRUCTION	TAM (JB)	TAM (MM)	LOAMPLONE
7	25 Mar 2025	APPROVED FOR CONSTRUCTION	MASSOGNA	LOAMPLONE	W.BOUJALI
6	14 Oct 2024	APPROVED FOR CONSTRUCTION	TAM (LD)	LOAMPLONE	W.BOUJALI
5	24 Jun 2024	APPROVED FOR CONSTRUCTION	TAM (LD)	LOAMPLONE	W.BOUJALI
4	18 Aug 2023	ISSUED FOR APPROVAL	TAM (LD)	LOAMPLONE	W.BOUJALI
3	02 Nov 2022	ISSUED FOR APPROVAL	TAM (LD)	LOAMPLONE	W.BOUJALI
2	26 Jul 2022	ISSUED FOR APPROVAL	TAM (ES)	LOAMPLONE	W.BOUJALI
1	08 Jul 2022	ISSUED FOR APPROVAL	TAM (ES)	LOAMPLONE	W.BOUJALI
0	15 Jun 2022	ISSUED FOR APPROVAL	TAM (ES)	LOAMPLONE	W.BOUJALI

Customer:
MANAENERGY

Contractor:
ITALFLUID

Engineering:
ITALFLUID

Technology Vendor:
TECHNICAL AMERICA INC

Customer:
Mahaj Riad Center, Batiment 6, 3eme etage,
Avenue Al Az, Hay Ryad, 10100 Rabat, Morocco

Offices:
VIA VIVALDI,4
Tel.+39 085 4224374 fax+39 085 4220742

Offices:
VIA VIVALDI,4
Tel.+39 085 4224374 fax+39 085 4220742

Offices:
301 N Smith Avenue, 92880 Corona, California (USA)
Ph.+1 951 272 9540

TITLE:
LNG TENDRARA PLANT

OBJECT:
P&ID
FUEL GAS DISTRIBUTION

TYPE	SCALE	DOCUMENTS ID:	VENDOR DOC. CODE	SHEET/OF
A1	N/A	PRO13-ING-PR41	21044-PR-PID-42001	1/1