


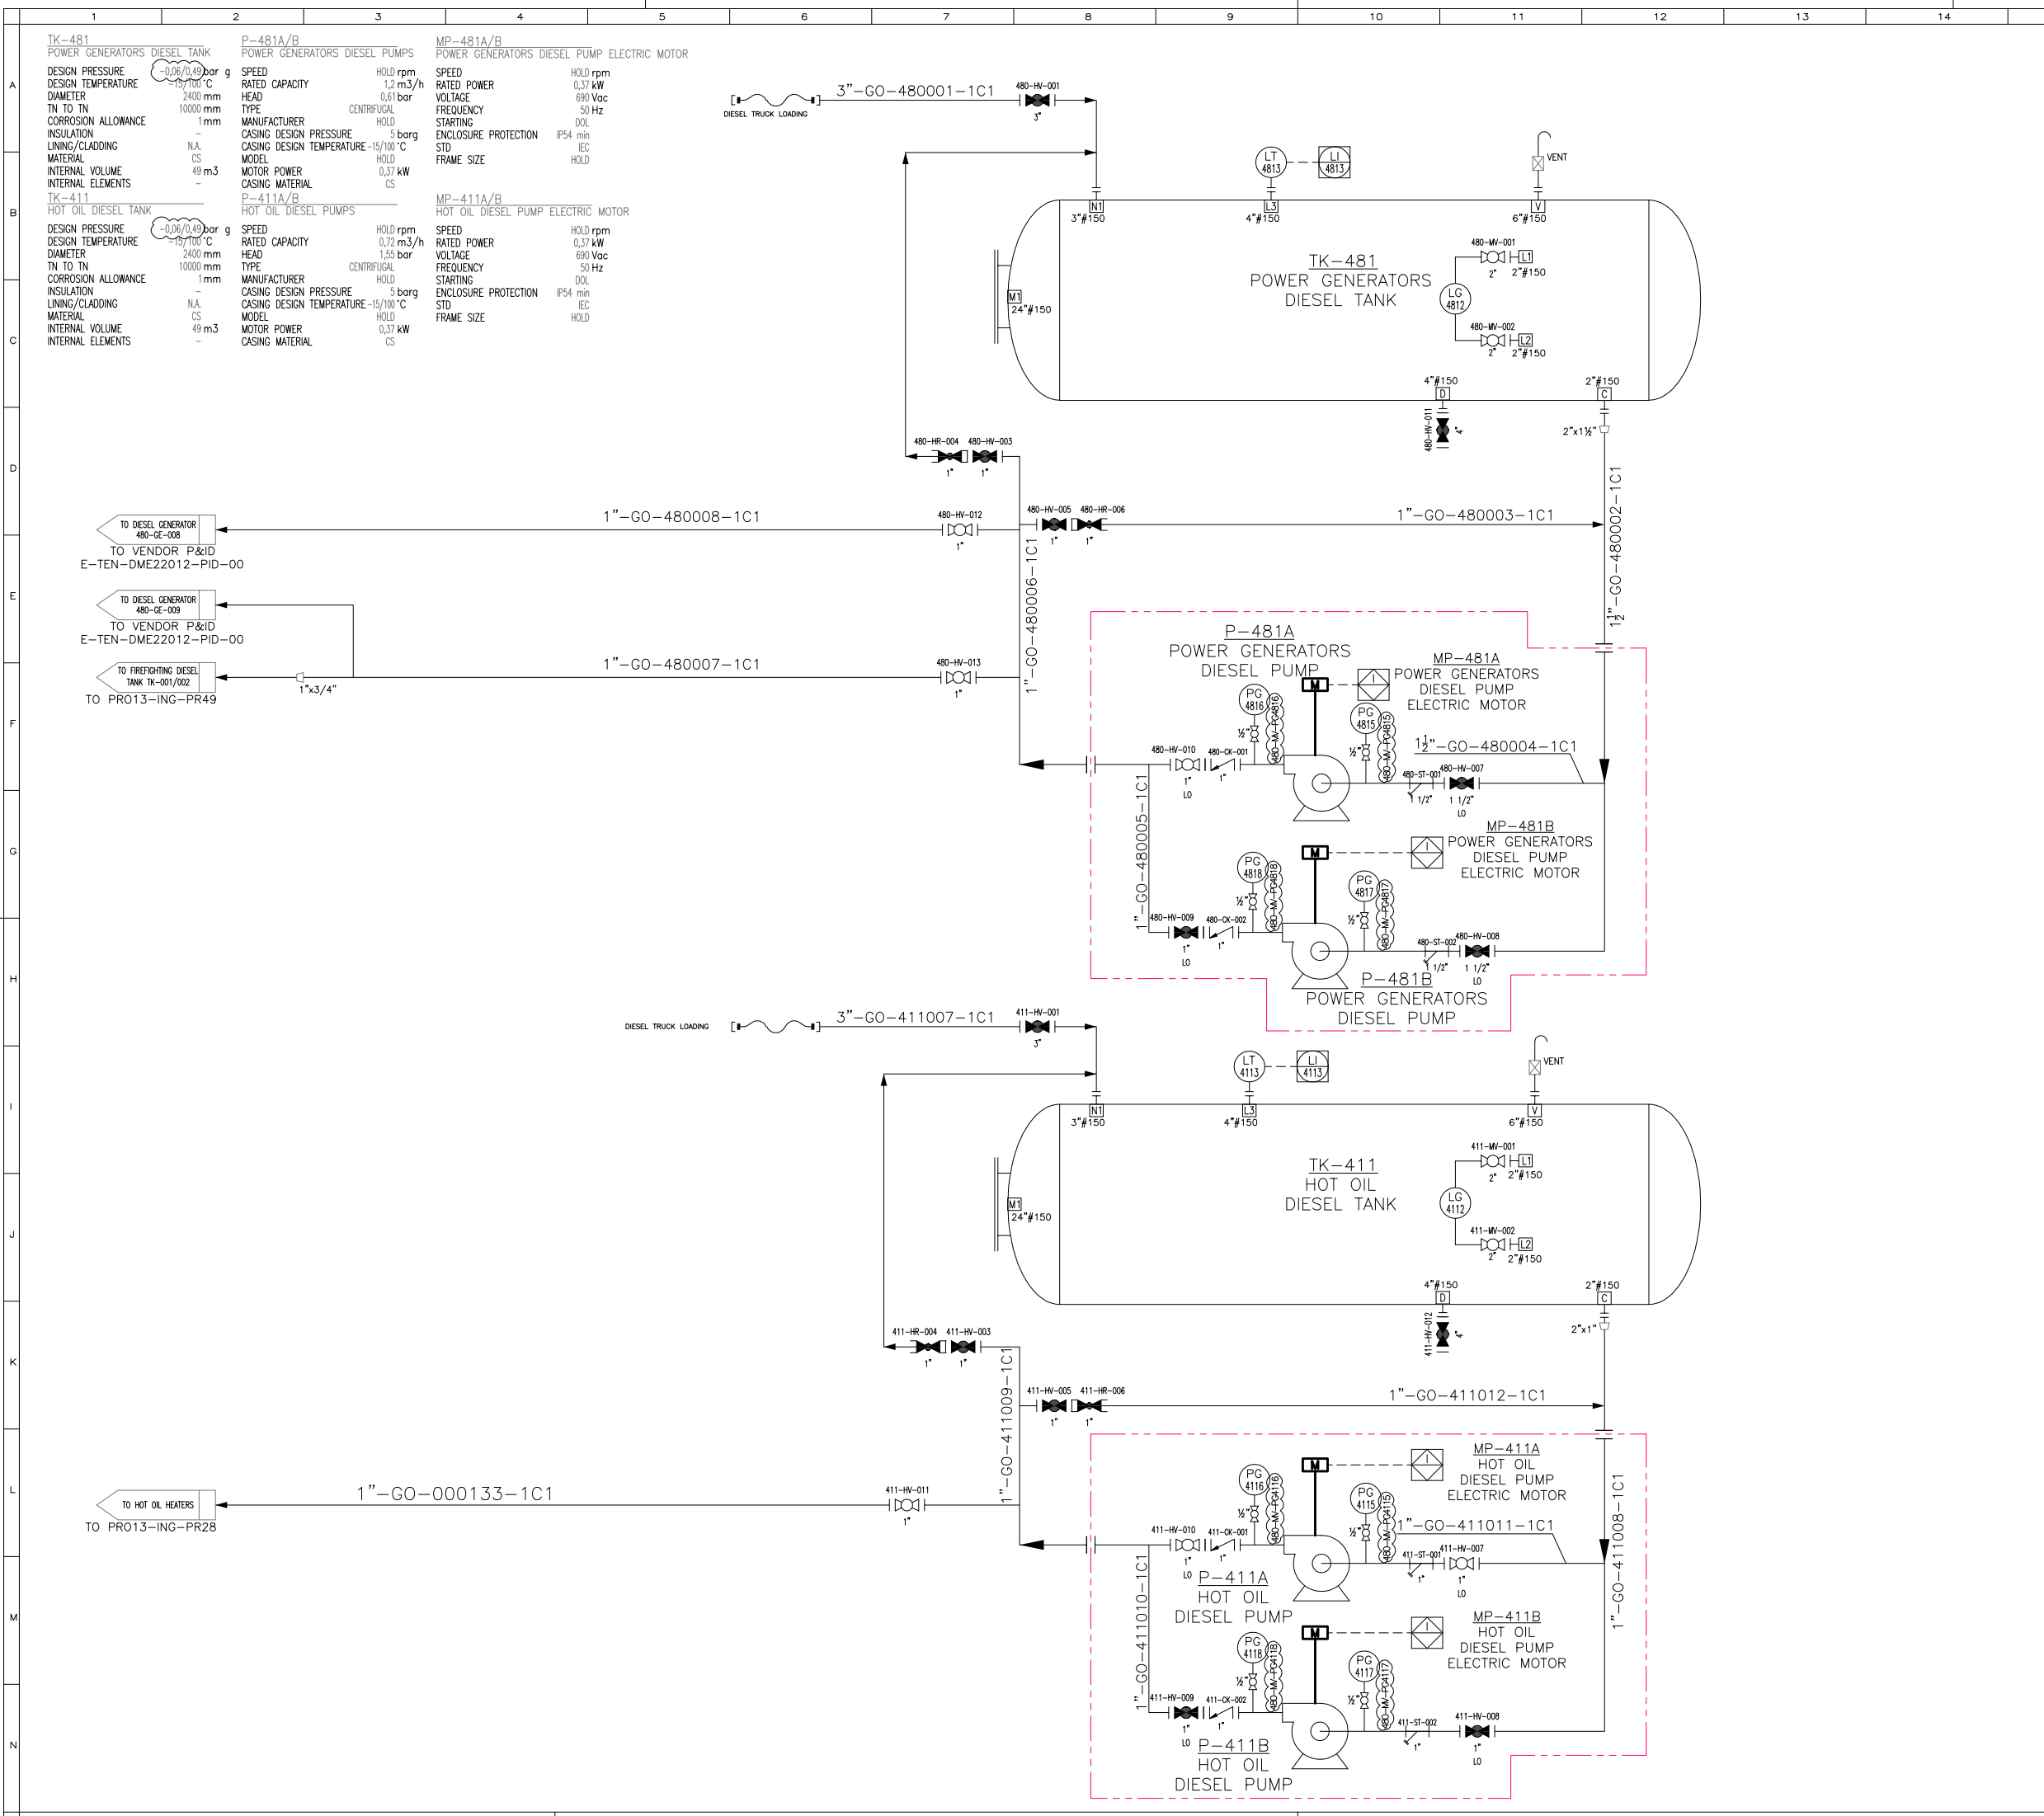

REFERENCE DOCUMENTS

P&ID LEGEND	PRO13-ING-PRO0 21044-PR-PID-00000
UTILITY FLOW DIAGRAM	PRO10-ING-PRO5/09 21044-PR-UFD-00001
MATERIAL SELECTION DIAGRAM	PRO08-ING-FR01 21044-PR-MSD-00001

8	03 Apr 2026	APPROVED FOR CONSTRUCTION	TAM (JB)	TAM (MM)	LOAMPLONE
7	14 Oct 2024	APPROVED FOR CONSTRUCTION	P.MARZIAN	A.ZAPPONE	W.BOULLALI
6	13 Jul 2024	ISSUED FOR APPROVAL	P.MARZIAN	A.ZAPPONE	W.BOULLALI
5	29 May 2024	ISSUED FOR APPROVAL	P.MARZIAN	A.ZAPPONE	W.BOULLALI
4	26 Mar 2024	ISSUED FOR APPROVAL	P.MARZIAN	A.ZAPPONE	W.BOULLALI
3	02 Nov 2022	ISSUED FOR APPROVAL	TAM (LD)	LOAMPLONE	W.BOULLALI
2	26 Jul 2022	ISSUED FOR APPROVAL	TAM (ES)	LOAMPLONE	W.BOULLALI
1	08 Jul 2022	ISSUED FOR APPROVAL	TAM (ES)	LOAMPLONE	W.BOULLALI
0	21 Jun 2022	ISSUED FOR APPROVAL	TAM (ES)	LOAMPLONE	W.BOULLALI
Rev.	Date	Description	Draft	Check'd	Approved

Customer: MANAENERGY

Contractor: ITALFLUID

Engineering: ITALFLUID

Technology Vendor: TECHNICAL AMERICA INC

OFFICES: Mahaj Riad Center, Batiment 6, 3eme etage, Avenue Al Az, Hay Ryad, 10100 Rabat, Morocco

OFFICES: VIA VVALDI,4 MONTESILVANO (ITALY) Tel.+39 085 4224374 fax+39 085 4220742

OFFICES: VIA VVALDI,4 MONTESILVANO (ITALY) Tel.+39 085 4224374 fax+39 085 4220742

OFFICES: 301 N Smith Avenue, 92880 Corona, California (USA) Ph.+1 951 272 9540

TITLE: LNG TENDRARA PLANT

OBJECT: P&ID DIESEL UNIT

TYPE	SCALE	DOCUMENTS ID:	VENDOR DOC. CODE	SHEET/OF
A1	N/A	PRO13-ING-PR42	21044-PR-PID-43001	1/1