


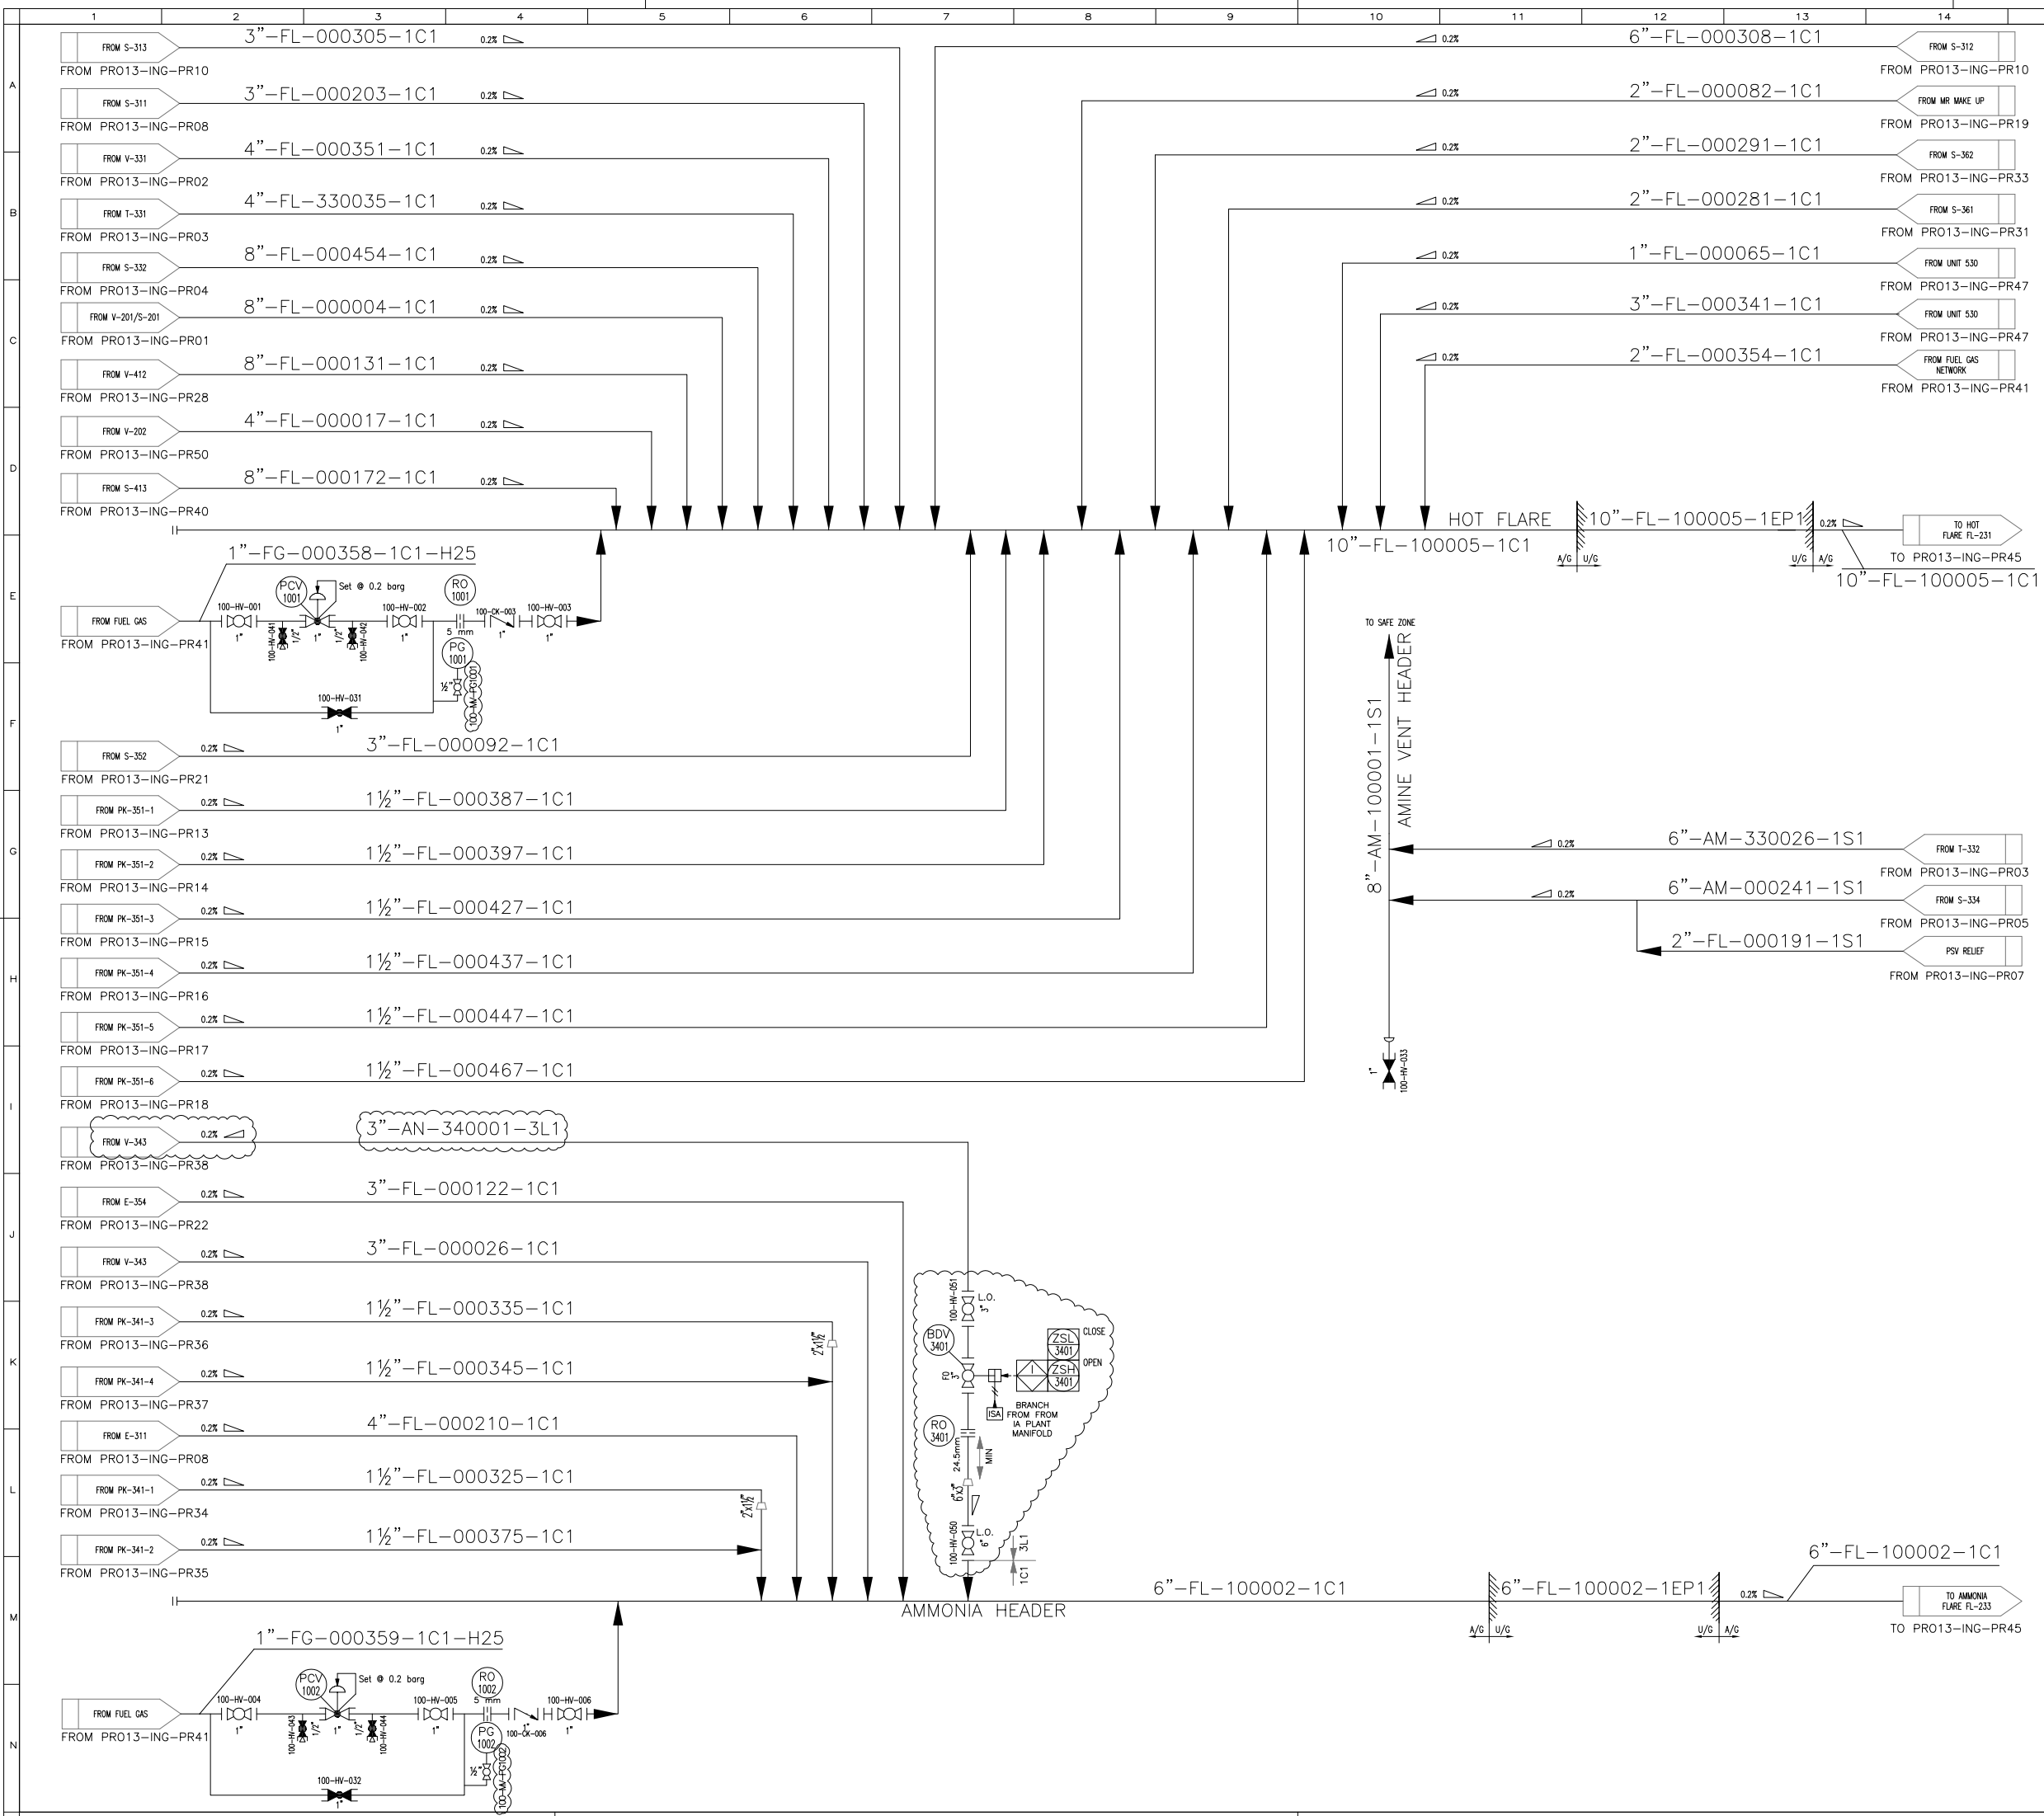

REFERENCE DOCUMENTS			
P&ID LEGEND		PRO13-ING-PRO0	
PROCESS FLOW DIAGRAM		21044-PR-PID-00000	
UTILITY FLOW DIAGRAM		PRO10-ING-PR01/02/03/04	
MATERIAL SELECTION DIAGRAM		21044-PR-PFD-00001	
		PRO10-ING-PR10	
		21044-PR-UFD-00001	
		PRO08-ING-FR01	
		21044-PR-MSD-00001	

7	03 Apr 2026	APPROVED FOR CONSTRUCTION	TAM (JB)	TAM (UM)	L.CAMPLONE
6	24 Mar 2025	APPROVED FOR CONSTRUCTION (ADD CV/BDV/RO)	TAM (LD)	TAM (UM)	L.CAMPLONE
5	24 Jun 2024	APPROVED FOR CONSTRUCTION	TAM (LD)	L.CAMPLONE	W.BOUJALU
4	25 Jul 2023	ISSUED FOR APPROVAL	TAM (ES)	L.CAMPLONE	W.BOUJALU
3	02 Nov 2022	ISSUED FOR APPROVAL	TAM (ES)	L.CAMPLONE	W.BOUJALU
2	26 Jul 2022	ISSUED FOR APPROVAL	TAM (ES)	L.CAMPLONE	W.BOUJALU
1	08 Jul 2022	ISSUED FOR APPROVAL	TAM (ES)	L.CAMPLONE	W.BOUJALU
0	07 Apr 2022	ISSUED FOR APPROVAL	TAM (ES)	L.CAMPLONE	W.BOUJALU
Rev.	Date	Description	Draft	Check'd	Approved
Customer: MANAENERGY			OFFICES: Mahaj Riad Center, Batiment 6, 3eme etage, Avenue Al Az, Hay Ryad, 10100 Rabat, Morocco		
Contractor: ITALFLUID			OFFICES: VIA VIVALDI,4 MONTESILVANO (ITALY) Tel.+39 085 4224374 fax+39 085 4220742		
Engineering: ITALFLUID			OFFICES: VIA VIVALDI,4 MONTESILVANO (ITALY) Tel.+39 085 4224374 fax+39 085 4220742		
Technology Vendor: TECHNICAL AMERICA INC			OFFICES: 301 N Smith Avenue, 92880 Corona, California (USA) Ph.+1 951 272 9540		
TITLE: LNG TENDRARA PLANT			OBJET: P&ID FLARE HEADER		
TYPE	SCALE	DOCUMENTS ID:	VENDOR DOC. CODE		SHEET/OF
A1	N/A	PRO13-ING-PR43	21044-PR-PID-23001		1/1