


S-551		P-551A/B	
CLOSED DRAIN TANK		CLOSED DRAIN PUMPS	
DESIGN PRESSURE	3.5 bar g	SPEED	145 to 485 rpm
DESIGN TEMPERATURE	-15/100 °C	RATED CAPACITY	22 m3/h
INTERNAL DIAMETER	1700 mm	HEAD	9.5 bar
TL TO TL	7000 mm	TYPE	PROGRESSING CAVITY
CORROSION ALLOWANCE	3 mm	MANUFACTURER	FCM
INSULATION	N.A.	CASING DESIGN PRESSURE	15 barg
LINING/CLADDING	N.A.	CASING DESIGN TEMPERATURE	-15/100 °C
MATERIAL	CS	MODEL	40M12S
INTERNAL VOLUME	17.2 m3	MOTOR POWER	12.75 kW
INTERNAL ELEMENTS	N.A.	CASING MATERIAL	CAST IRON

MP-551A/B	
CLOSED DRAIN PUMP ELECTRIC MOTOR	
SPEED	rpm
RATED POWER	HOLD kW
VOLTAGE	690 Vac
FREQUENCY	50 Hz
STARTING	SOFT START
ENCLOSURE PROTECTION	IP54 min
STD	IEC
FRAME SIZE	HOLD

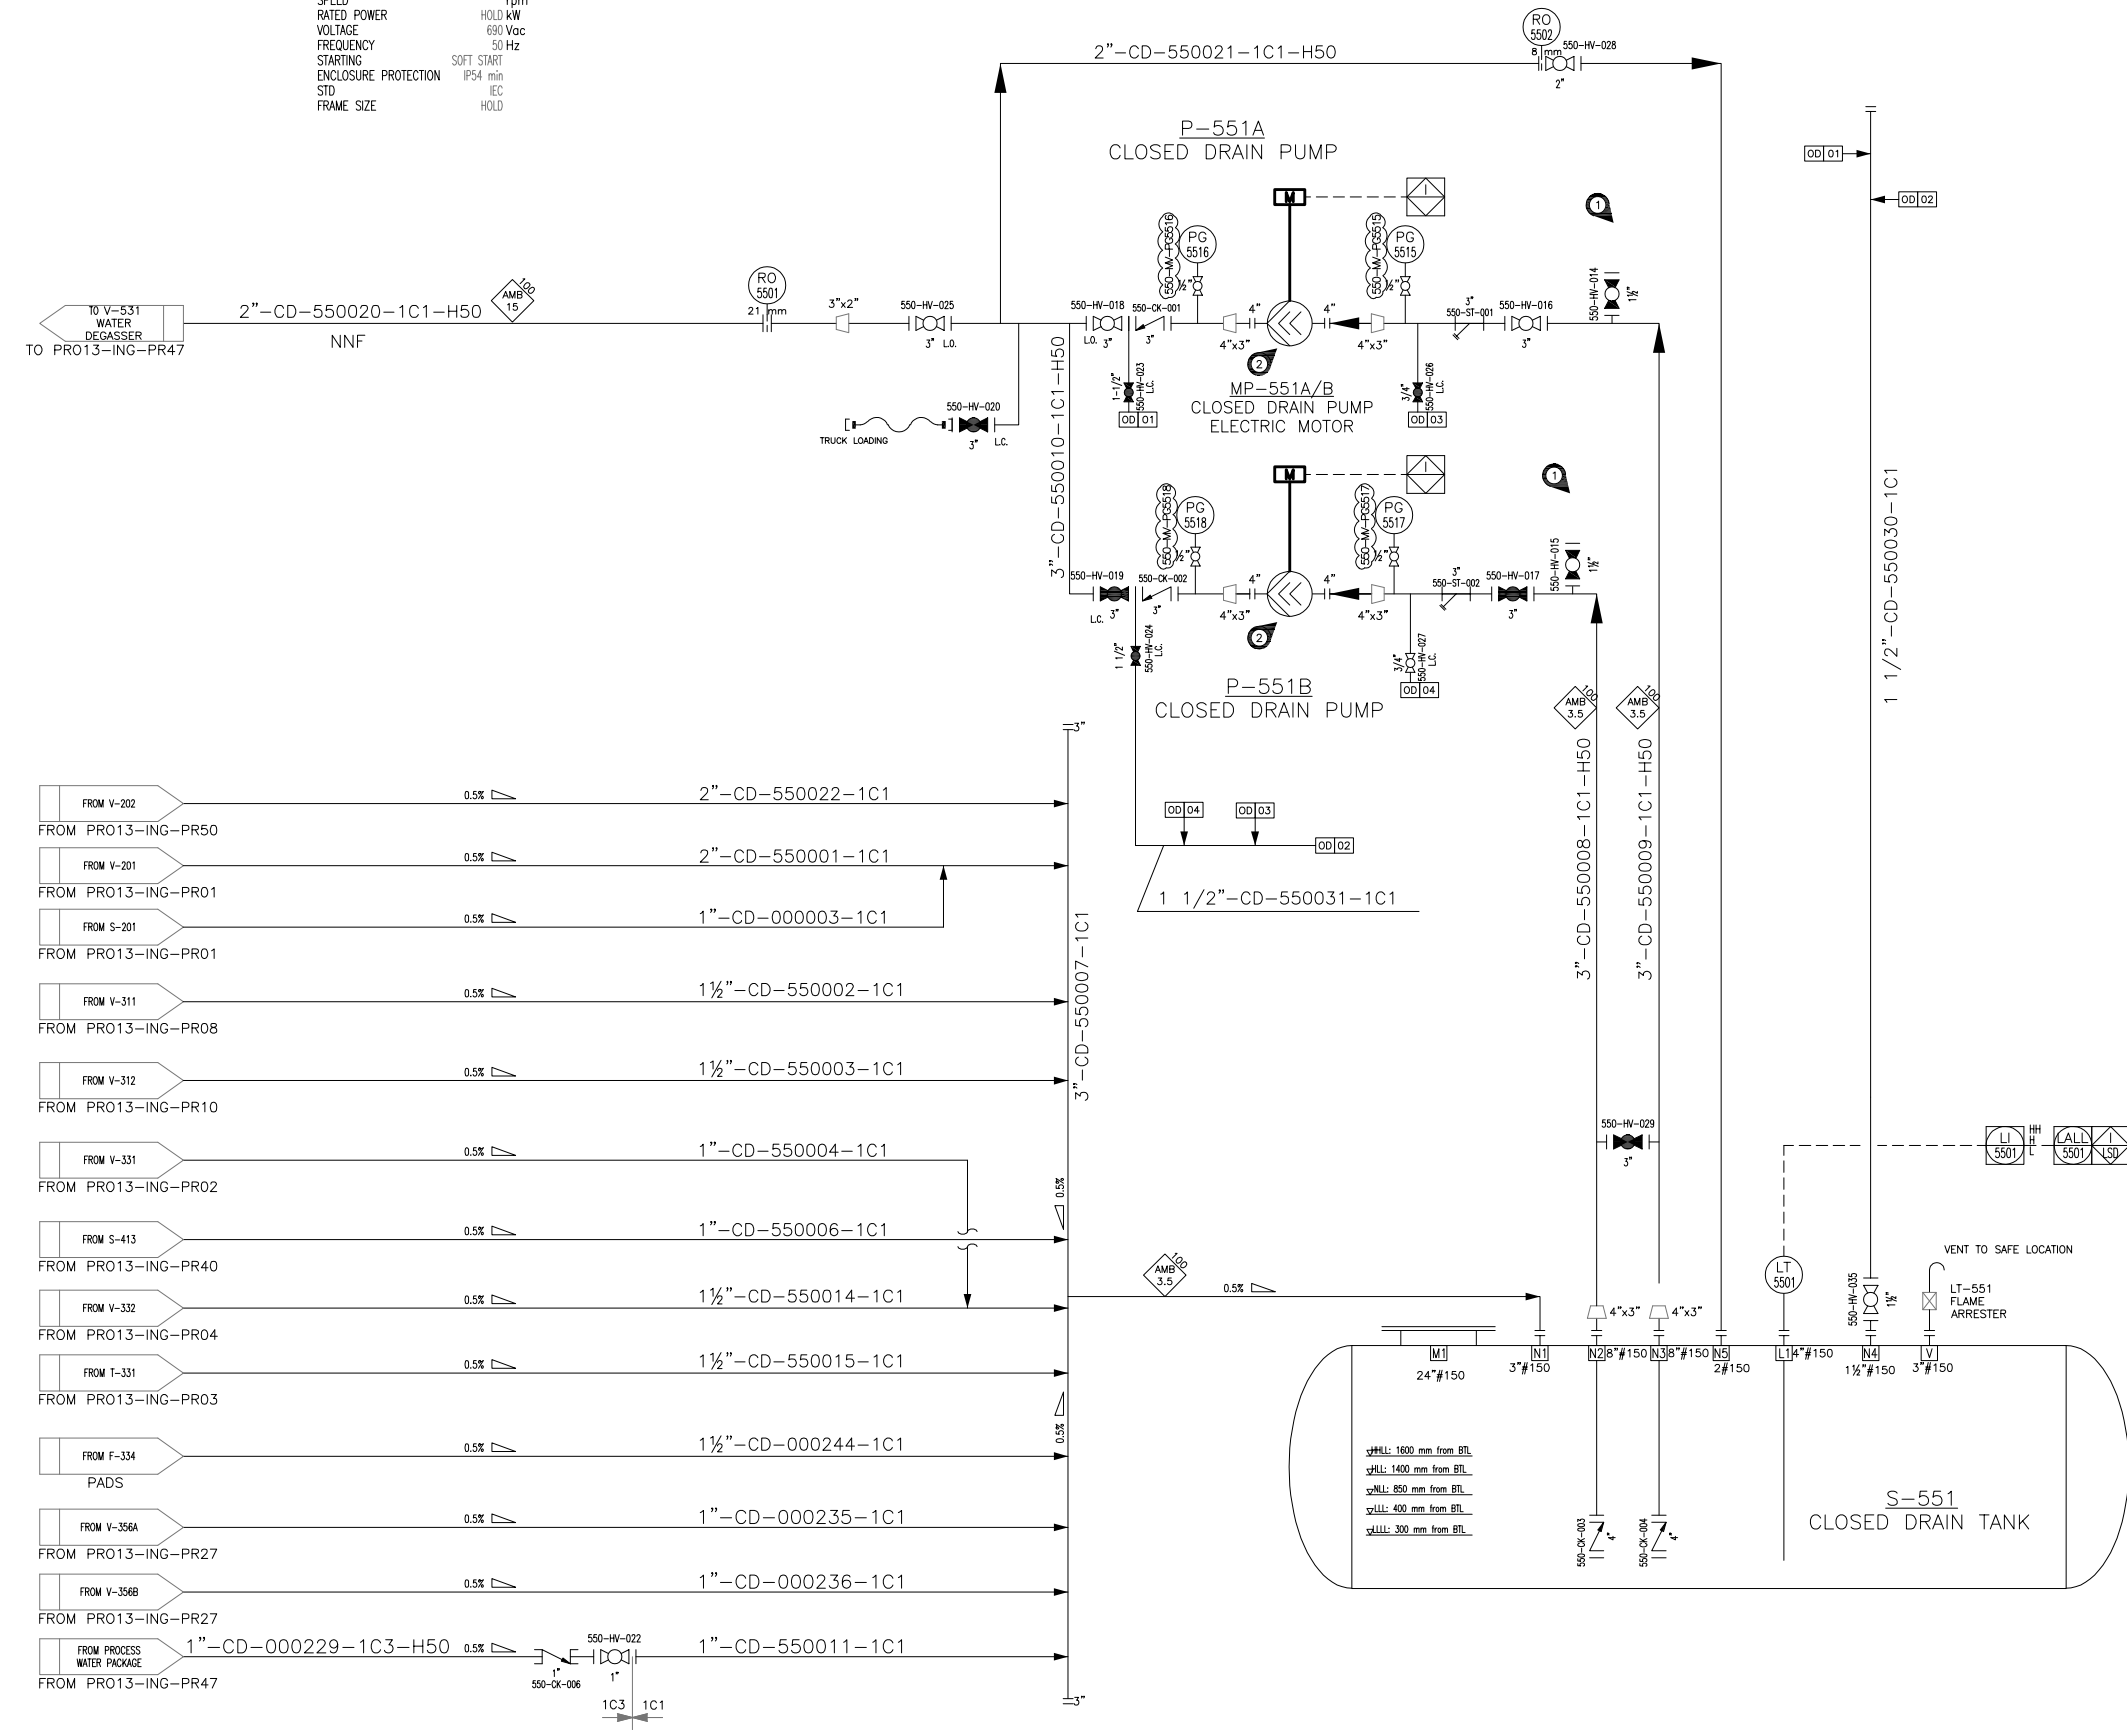

REFERENCE DOCUMENTS

P&ID LEGEND	PRO13-ING-PRO0 21044-PR-PID-00000
PROCESS FLOW DIAGRAM	PRO10-ING-PRO1/02/03/04 21044-PR-PFD-00001
UTILITY FLOW DIAGRAM	PRO10-ING-PR12
MATERIAL SELECTION DIAGRAM	21044-PR-UFD-00001 PRO08-ING-FR01 21044-PR-MSD-00001

NNF NORMALLY NO FLOW

NOTES

- 1 SUCTION LINE EXTERNAL FILLING FOR PUMP PRIMING
- 2 PUMP BODY EQUIPPED WITH ELECTRICAL TRACING AND INSULATION

8	03 Apr 2026	APPROVED FOR CONSTRUCTION	TAM (JB)	TAM (MM)	LOAMPLONE
7	26 Sep 2024	APPROVED FOR CONSTRUCTION	TAM (LD)	LOAMPLONE	W.BOUJALI
6	24 Jun 2024	APPROVED FOR CONSTRUCTION	TAM (LD)	LOAMPLONE	W.BOUJALI
5	22 Aug 2023	ISSUED FOR APPROVAL	TAM (LD)	LOAMPLONE	W.BOUJALI
4	13 Feb 2023	ISSUED FOR APPROVAL	TAM (LD)	LOAMPLONE	W.BOUJALI
3	02 Nov 2022	ISSUED FOR APPROVAL	TAM (LD)	LOAMPLONE	W.BOUJALI
2	26 Jul 2022	ISSUED FOR APPROVAL	TAM (LD)	LOAMPLONE	W.BOUJALI
1	08 Jul 2022	ISSUED FOR APPROVAL	TAM (ES)	LOAMPLONE	W.BOUJALI
0	21 Jun 2022	ISSUED FOR APPROVAL	TAM (ES)	LOAMPLONE	W.BOUJALI

Customer: MANAENERGY		Offices: Mahaj Riad Center, Batiment 6, 3eme etage, Avenue Al Az, Hay Ryad, 10100 Rabat, Morocco	
Contractor: ITALFLUID		Offices: VIA VIVALDI,4 MONTESILVANO (ITALY) Tel.+39 085 4224374 fax+39 085 4220742	
Engineering: ITALFLUID		Offices: VIA VIVALDI,4 MONTESILVANO (ITALY) Tel.+39 085 4224374 fax+39 085 4220742	
Technology Vendor: TECHNICAL AMERICA INC		Offices: 301 N Smith Avenue, 92880 Corona, California (USA) Ph.+1 951 272 9540	
TITLE: LNG TENDRARA PLANT		OBJECT: P&ID CLOSED DRAIN UNIT	
TYPE	SCALE	DOCUMENTS ID:	VENDOR DOC. CODE
A1	N/A	PRO13-ING-PR46	21044-PR-PID-55001
			SHEET/OF 1/1