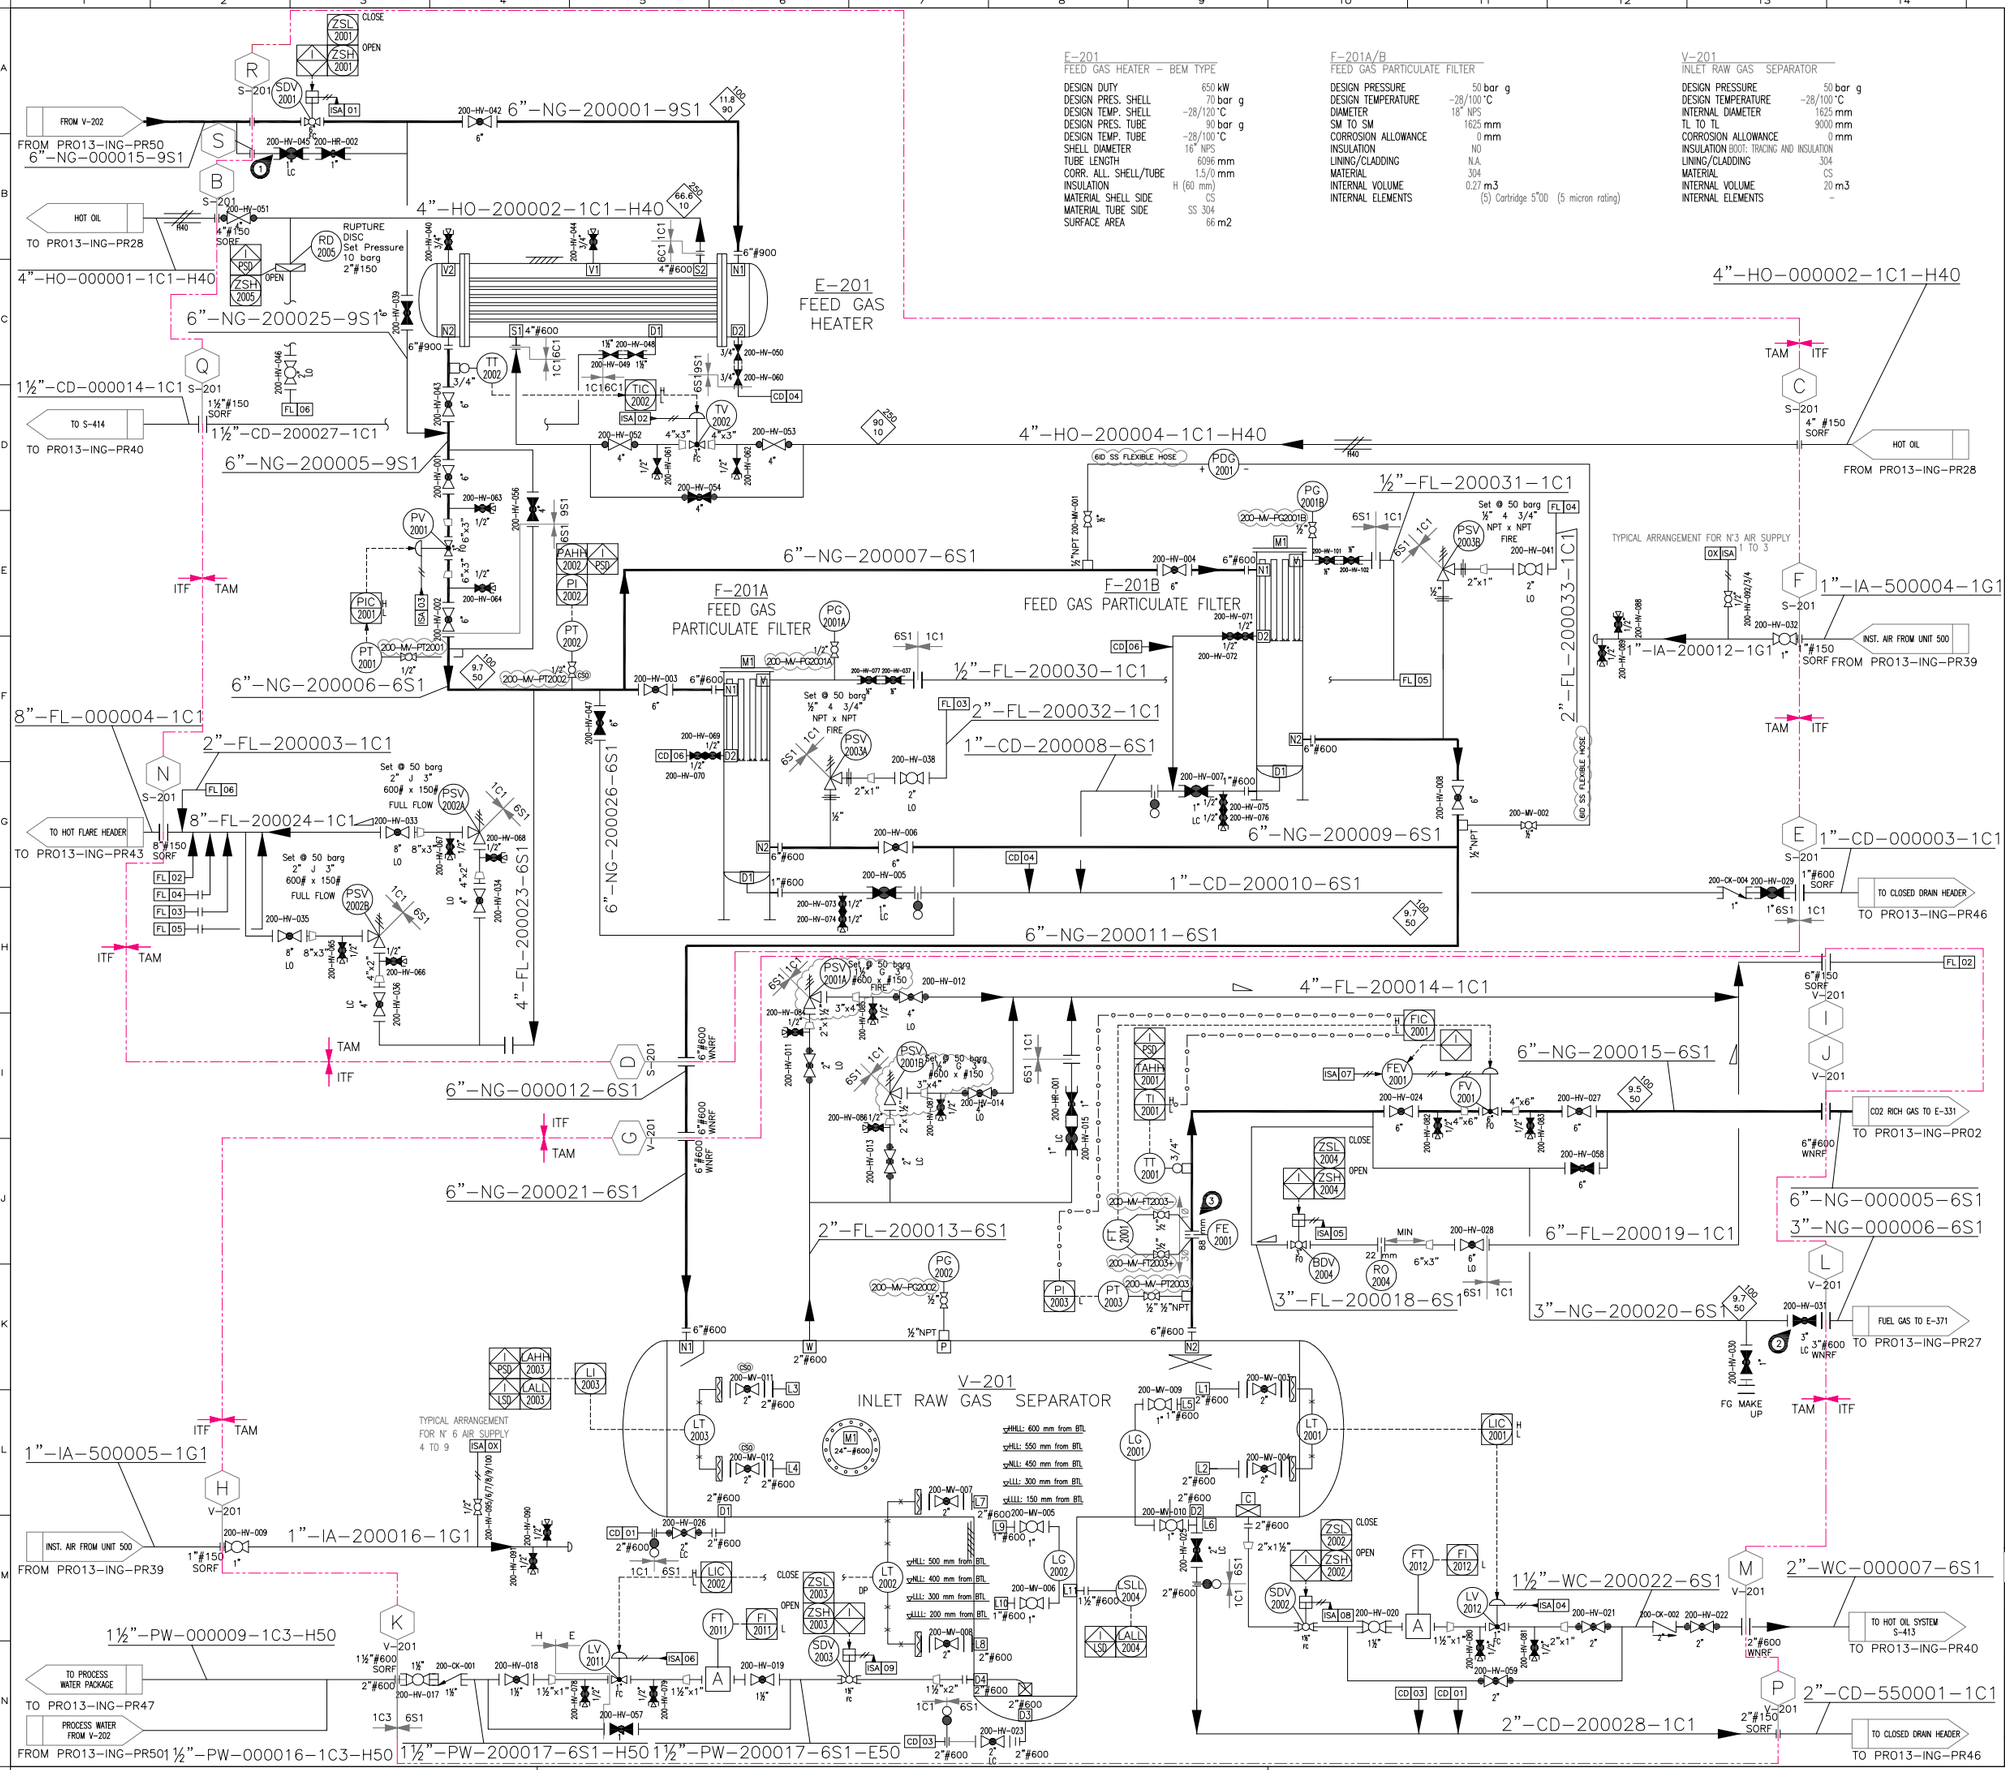

REFERENCE DOCUMENTS

P&ID LEGEND	PR013-ING-PR00 21044-PR-PID-00000
PROCESS FLOW DIAGRAM	PRO10-ING-PR01/02/03/04 21044-PR-PFD-00001
UTILITY FLOW DIAGRAM	PRO10-ING-PR05/11/12 21044-PR-UFD-00001
MATERIAL SELECTION DIAGRAM	PRO08-ING-FR01 21044-PR-MSD-00001

ISA 0X INSTRUMENT SUPPLY AIR

FL 0X VENT TO FLARE HEADER

CD 0X CLOSED DRAIN TO DRAIN HEADER

NOTES

1. BYPASS OF SDV-2001 INSTALLED FOR START UP.
2. RAW GAS TO FUEL GAS SYSTEM FOR START UP.
3. CONDITIONING 4 HOLES ORIFICE PLATE.
4. ALL INSTRUMENTS AND MANUAL VALVES ON THIS P&ID AND OUT OF SKID LIMITS WILL BE SUPPLIED BY TAM AS LOOSE ITEMS.
5. DESIGN AND EXECUTION OF ELECTRICAL TRACING BY ITF.

---------- TAM SUPPLY LIMIT

Rev.	Date	Description	Draft	Check'd	Approved
6	27 Mar 2026	APPROVED FOR CONSTRUCTION	TAM (JB)	TAM (MM)	I.CAMPLONE
5	15 Oct 2025	APPROVED FOR CONSTRUCTION	TAM (RK)	I.CAMPLONE	W.BOULALI
4	08 Feb 2024	APPROVED FOR CONSTRUCTION	TAM (LD)	I.CAMPLONE	W.BOULALI
3	25 Jan 2024	ISSUED FOR APPROVAL	TAM (LD)	I.CAMPLONE	W.BOULALI
2	02 Nov 2022	ISSUED FOR APPROVAL	TAM (LD)	I.CAMPLONE	W.BOULALI
1	21 Jul 2022	ISSUED FOR APPROVAL	TAM (ES)	I.CAMPLONE	W.BOULALI
0	24 Jun 2022	ISSUED FOR APPROVAL	TAM (ES)	I.CAMPLONE	W.BOULALI

Customer: MANAENERGY
OFFICES: Mahaj Riad Center, Batiment 6, 3eme etage, Avenue Al Arz, Hay Ryad, 10100 Rabat, Morocco

Contractor: ITALFLUID
OFFICES: VIA VIVALDI,4 MONTESILVANO (ITALY) Tel.+39 085 4224374 fax+39 085 4220742

Engineering: ITALFLUID
OFFICES: VIA VIVALDI,4 MONTESILVANO (ITALY) Tel.+39 085 4224374 fax+39 085 4220742

Technology Vendor: TECHNICAL AMERICA INC
OFFICES: 301 N Smith Avenue, 92880 Corona, California (USA) Ph.+1 951 272 9540

TITLE: LNG TENDRARA PLANT

OBJECT: P&ID PLANT INLET – UNIT 200 – SKID S-201/V-201

TYPE	SCALE	DOCUMENTS ID:	VENDOR DOC. CODE	SHEET/OF
A1	N/A	PRO13-ING-PR01	21044-PR-PID-20001	1/1

Documento di proprieta' aziendale. La Societa' tutelera' i propri diritti a termine di legge. This document is Company property. The Company lawfully reserves all rights.