


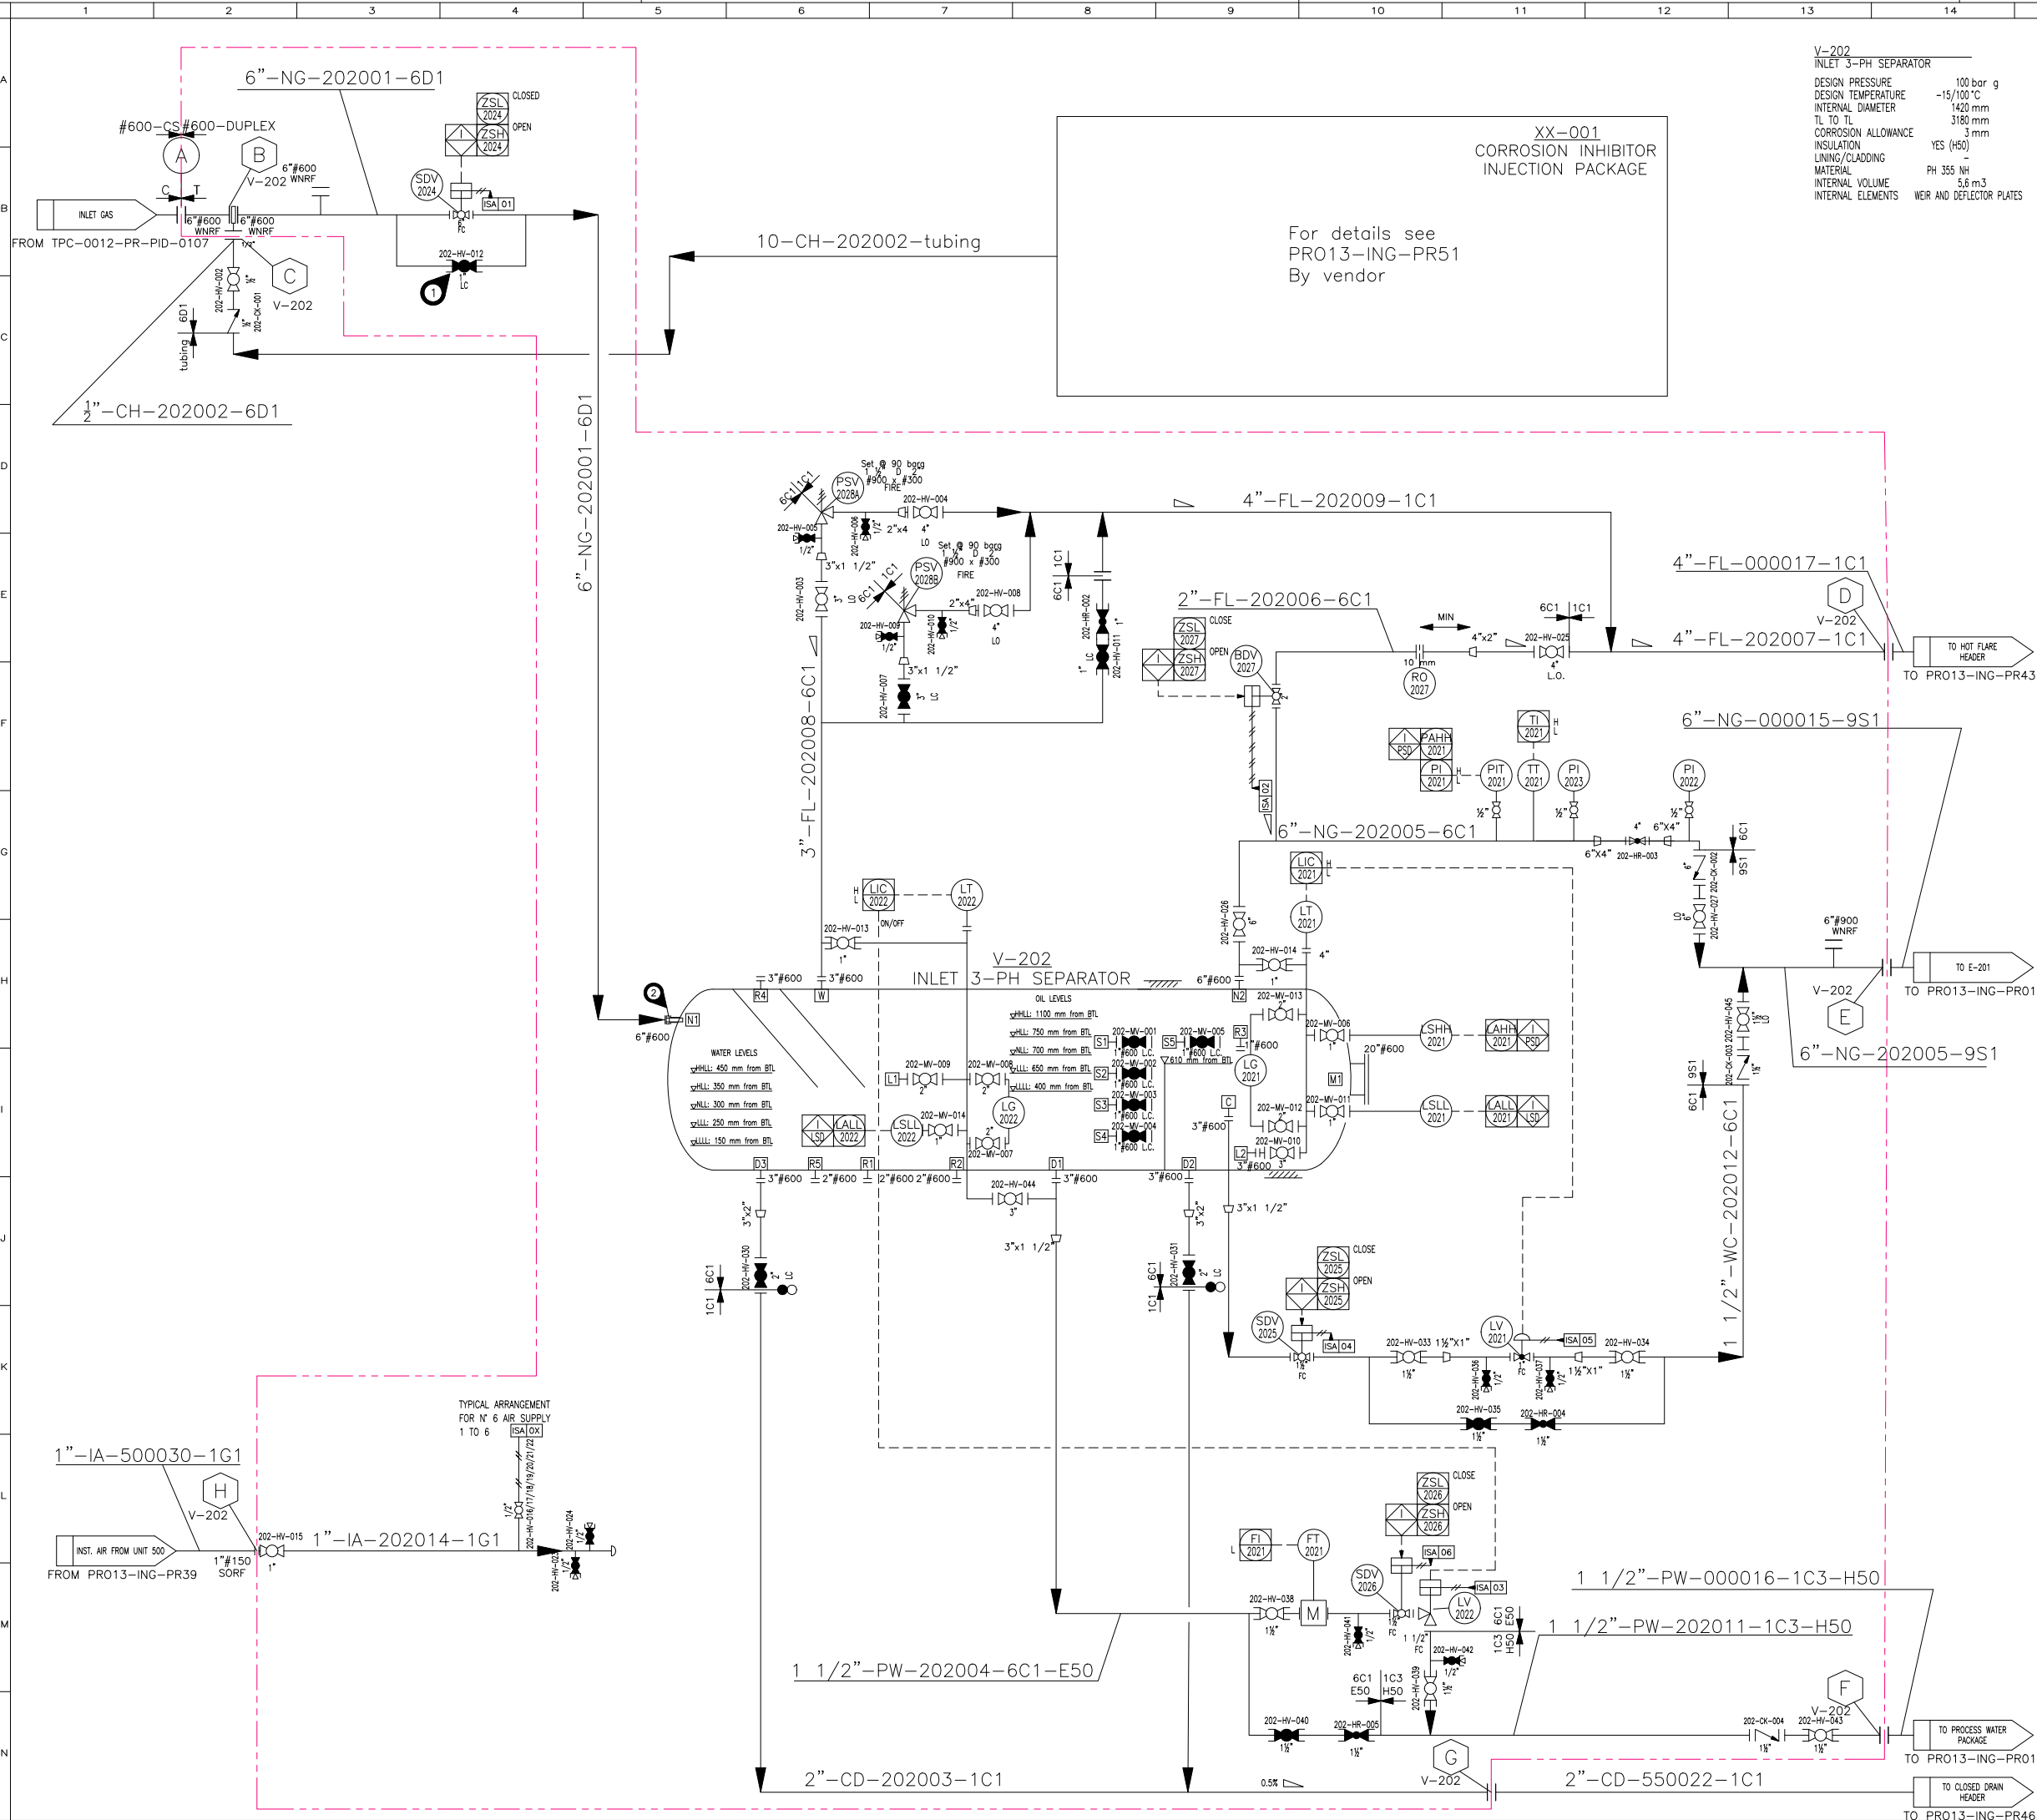

V-202
INLET 3-PH SEPARATOR
DESIGN PRESSURE 100 bar g
DESIGN TEMPERATURE -15/100 °C
INTERNAL DIAMETER 1420 mm
TL TO TL 3180 mm
CORROSION ALLOWANCE 3 mm
INSULATION YES (H50)
LINING/CLADDING -
MATERIAL PH 355 NH
INTERNAL VOLUME 5,6 m3
INTERNAL ELEMENTS WEIR AND DEFLECTOR PLATES

XX-001
CORROSION INHIBITOR
INJECTION PACKAGE

For details see
PRO13-ING-PR51
By vendor

REFERENCE DOCUMENTS

P&ID LEGEND	PRO13-ING-PR00 21044-PR-PID-00000
PROCESS FLOW DIAGRAM	PRO10-ING-PRO1/02/03/04 21044-PR-PFD-00001
UTILITY FLOW DIAGRAM	PRO10-ING-PR11 21044-PR-UFD-00001
MATERIAL SELECTION DIAGRAM	PRO08-ING-FR01 21044-PR-MSD-00001

- ISA0X INSTRUMENT SUPPLY AIR
FL0X VENT TO FLARE HEADER
CD0X CLOSED DRAIN TO DRAIN HEADER

NOTES

- 1 BYPASS OF SDV-2024 INSTALLED FOR START UP.
2 INNER DUPLEX PIPE WELDED TO A DRIP RING

4	24-06-2024	REVISED WHERE INDICATED	P.MARZIANI	A.ZAPPONE	L.COMPLONE	
3	24-08-2023	REVISED WHERE INDICATED	P.MARZIANI	A.ZAPPONE	L.COMPLONE	
2	23-06-2023	REVISED WHERE INDICATED	P.MARZIANI	A.ZAPPONE	L.COMPLONE	
1	22-05-2023	ISSUED FOR APPROVAL	P.MARZIANI	A.ZAPPONE	L.COMPLONE	
0	04-05-2023	ISSUED FOR APPROVAL	M.FERRARINI	A.ZAPPONE	L.COMPLONE	
Rev.	Date	Description	Draft	Check'd (ITF)	App'd (ITF)	SOUND ENERGY

Customer:	SOUND ENERGY	OFFICES:	Espace les Patios 1st floor, Avenue Annakhil Hay Riad, Rabat 10100
Contractor:	ITALFLUID	OFFICES:	VIA VIVALDI,4 Tel.+39 085 4224374 fax+39 085 4220742
Engineering:	ITALFLUID	OFFICES:	VIA VIVALDI,4 Tel.+39 085 4224374 fax+39 085 4220742
Technology Vendor:	TECHNICAL AMERICA INC.	OFFICES:	Ph.+1 951 272 9540 Corona, California (USA)

TITLE:	LNG TENDRARA PLANT	OBJECT:	P&ID PLANT INLET - UNIT 200 - V-202
TYPE	SCALE	DOCUMENTS ID:	VENDOR DOC. CODE
A1	N/A	PRO13-ING-PR50	1/1