

EQUIPMENT


SERVICE	CORROSION INHIBITOR STORAGE TANK
OUTSIDE DIAMETER	mm 958
HEIGHT (to TL)	mm 1350
VOLUME	mc 1,1
DESIGN PRESSURE	barg 0,3
DESIGN TEMPERATURE	°C -15 / +80
SERIAL NUMBER n°	HOLD
MATERIAL	316 L
CORROSION ALLOWANCE	mm 0

EQUIPMENT

SERVICE	VOLUM. PUMP
FLOWRATE (OP / RATED)/h	1 / 5
HEAD (OP / RATED)	m 465 / 1020
POWER	kw 0,18
VOLTAGE	V 400
SERIAL n°	180355/180356
MODEL	1K15N01AB7ML4BO0

REFERENCE DOCUMENTS

P&ID LEGEND	PRO13-ING-PR00
PROCESS FLOW DIAGRAM	21044-PR-PID-00000
UTILITY FLOW DIAGRAM	PRO10-ING-PR12
MATERIAL SELECTION DIAGRAM	21044-PR-UFD-00001
	PRO08-ING-FR01
	21044-PR-MSD-00001

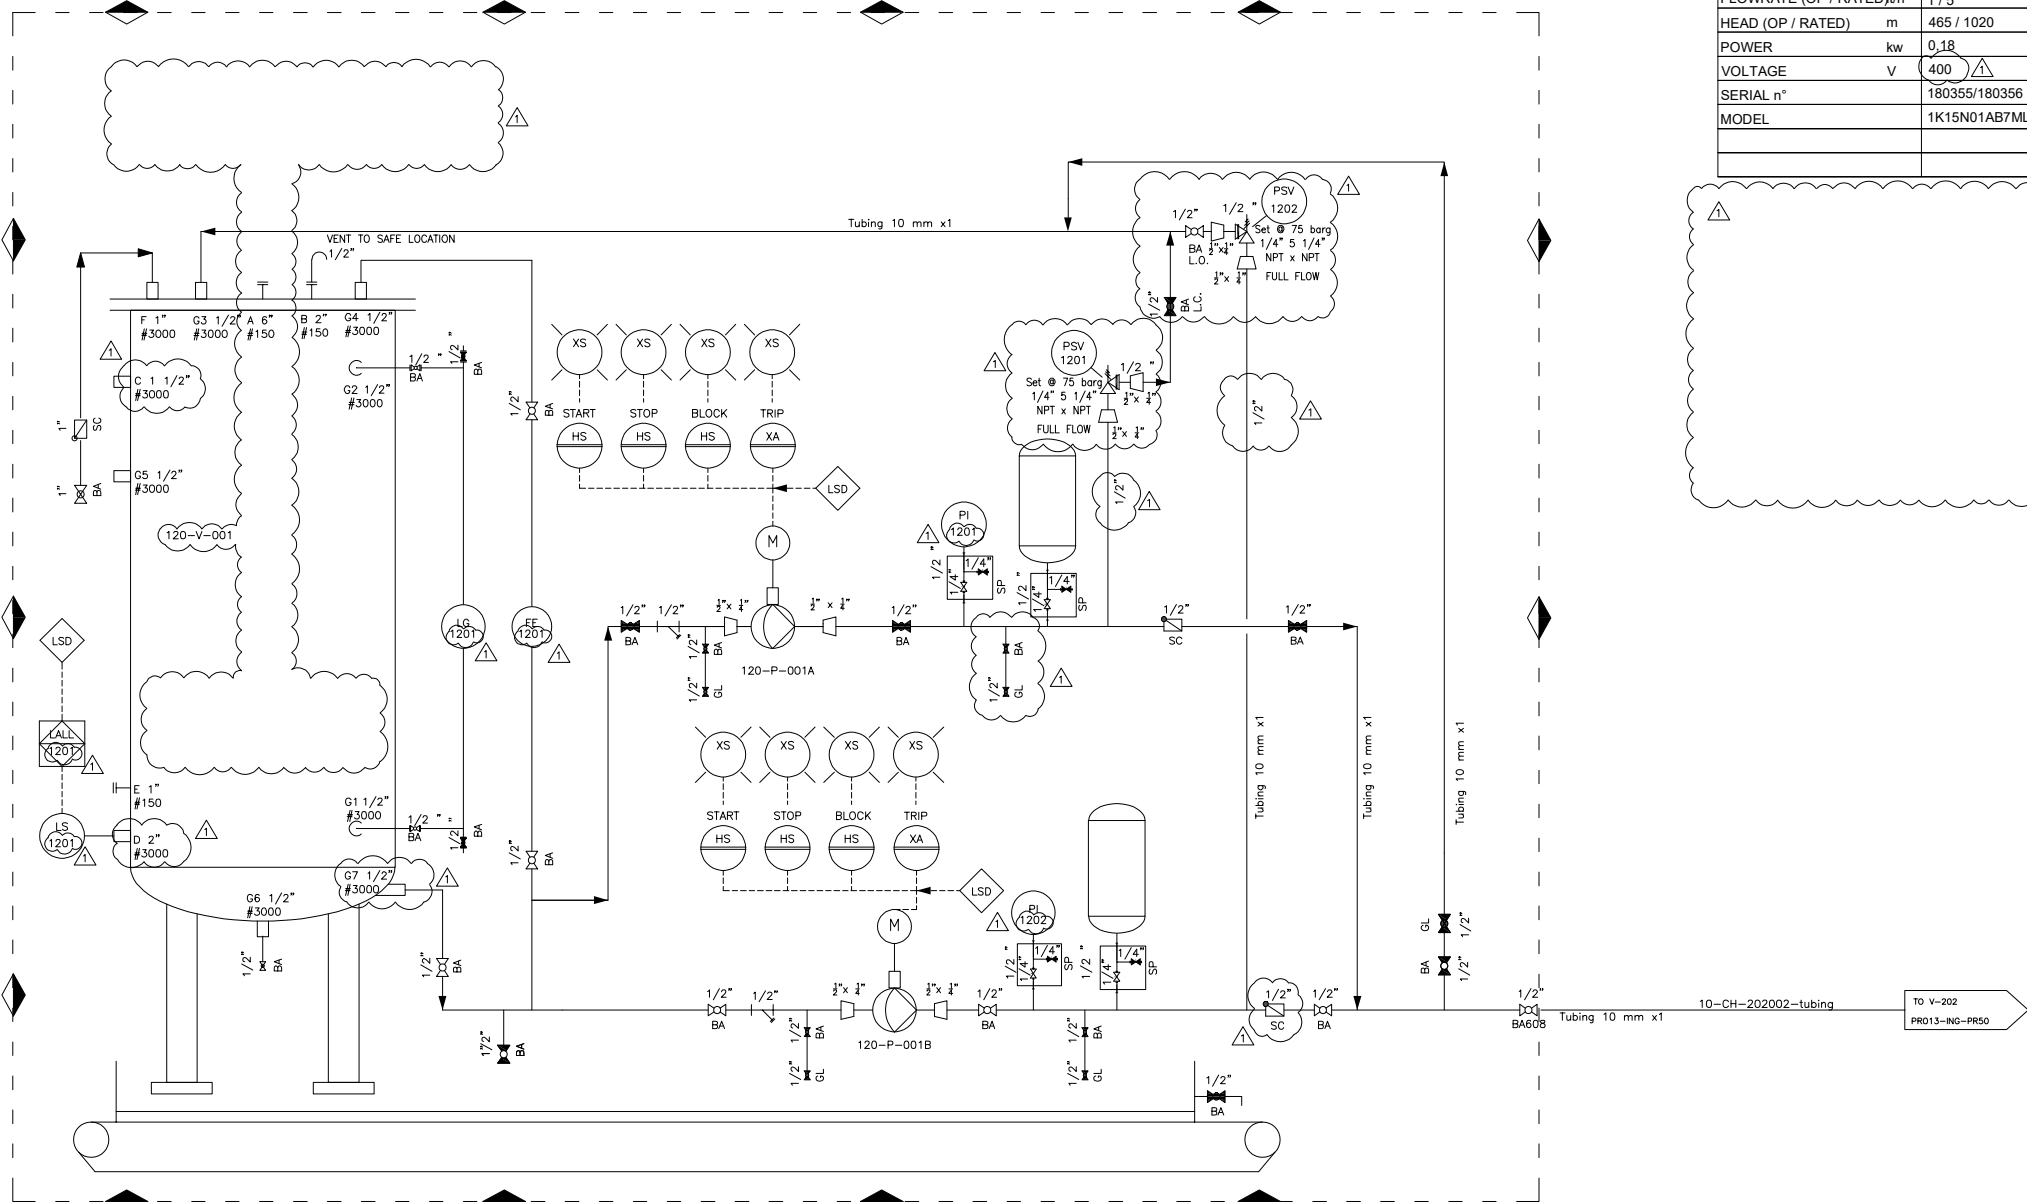

1	05 Jun 2024	ISSUED FOR CONSTRUCTION	P.Marziani	L.CAMPLONE	L.CAMPLONE
0	07 Jun 2023	ISSUED FOR APPROVAL	P.Marziani	L.CAMPLONE	L.CAMPLONE
Rev.	Date	Description	Draft (ITF)	Check's (ITF)	App'd's (ITF)
Customer: SOUND ENERGY			OFFICES: Espace les Patios 1st floor, Avenue Annakhi Hay Road, Rabat 10100		
Contractor: ITALFLUID			OFFICES: VIA VIVALDI,4 Tel.+39 085 4224374		
Engineering: ITALFLUID			OFFICES: VIA VIVALDI,4 Tel.+39 085 4224374		
Technology Vendor: TECHNICAL AMERICA INC			OFFICES: Ph.+1 951 272 9540		
TITLE: LNG TENDRARA PLANT			OBJECT: P&ID -UNIT 120- CORROSION INHIBITOR		
TYPE	SCALE	DOCUMENTS ID:	VENDOR DOC. CODE		SHEET/OF
A1	N/A	PRO13-ING-PR51	-		1/1