


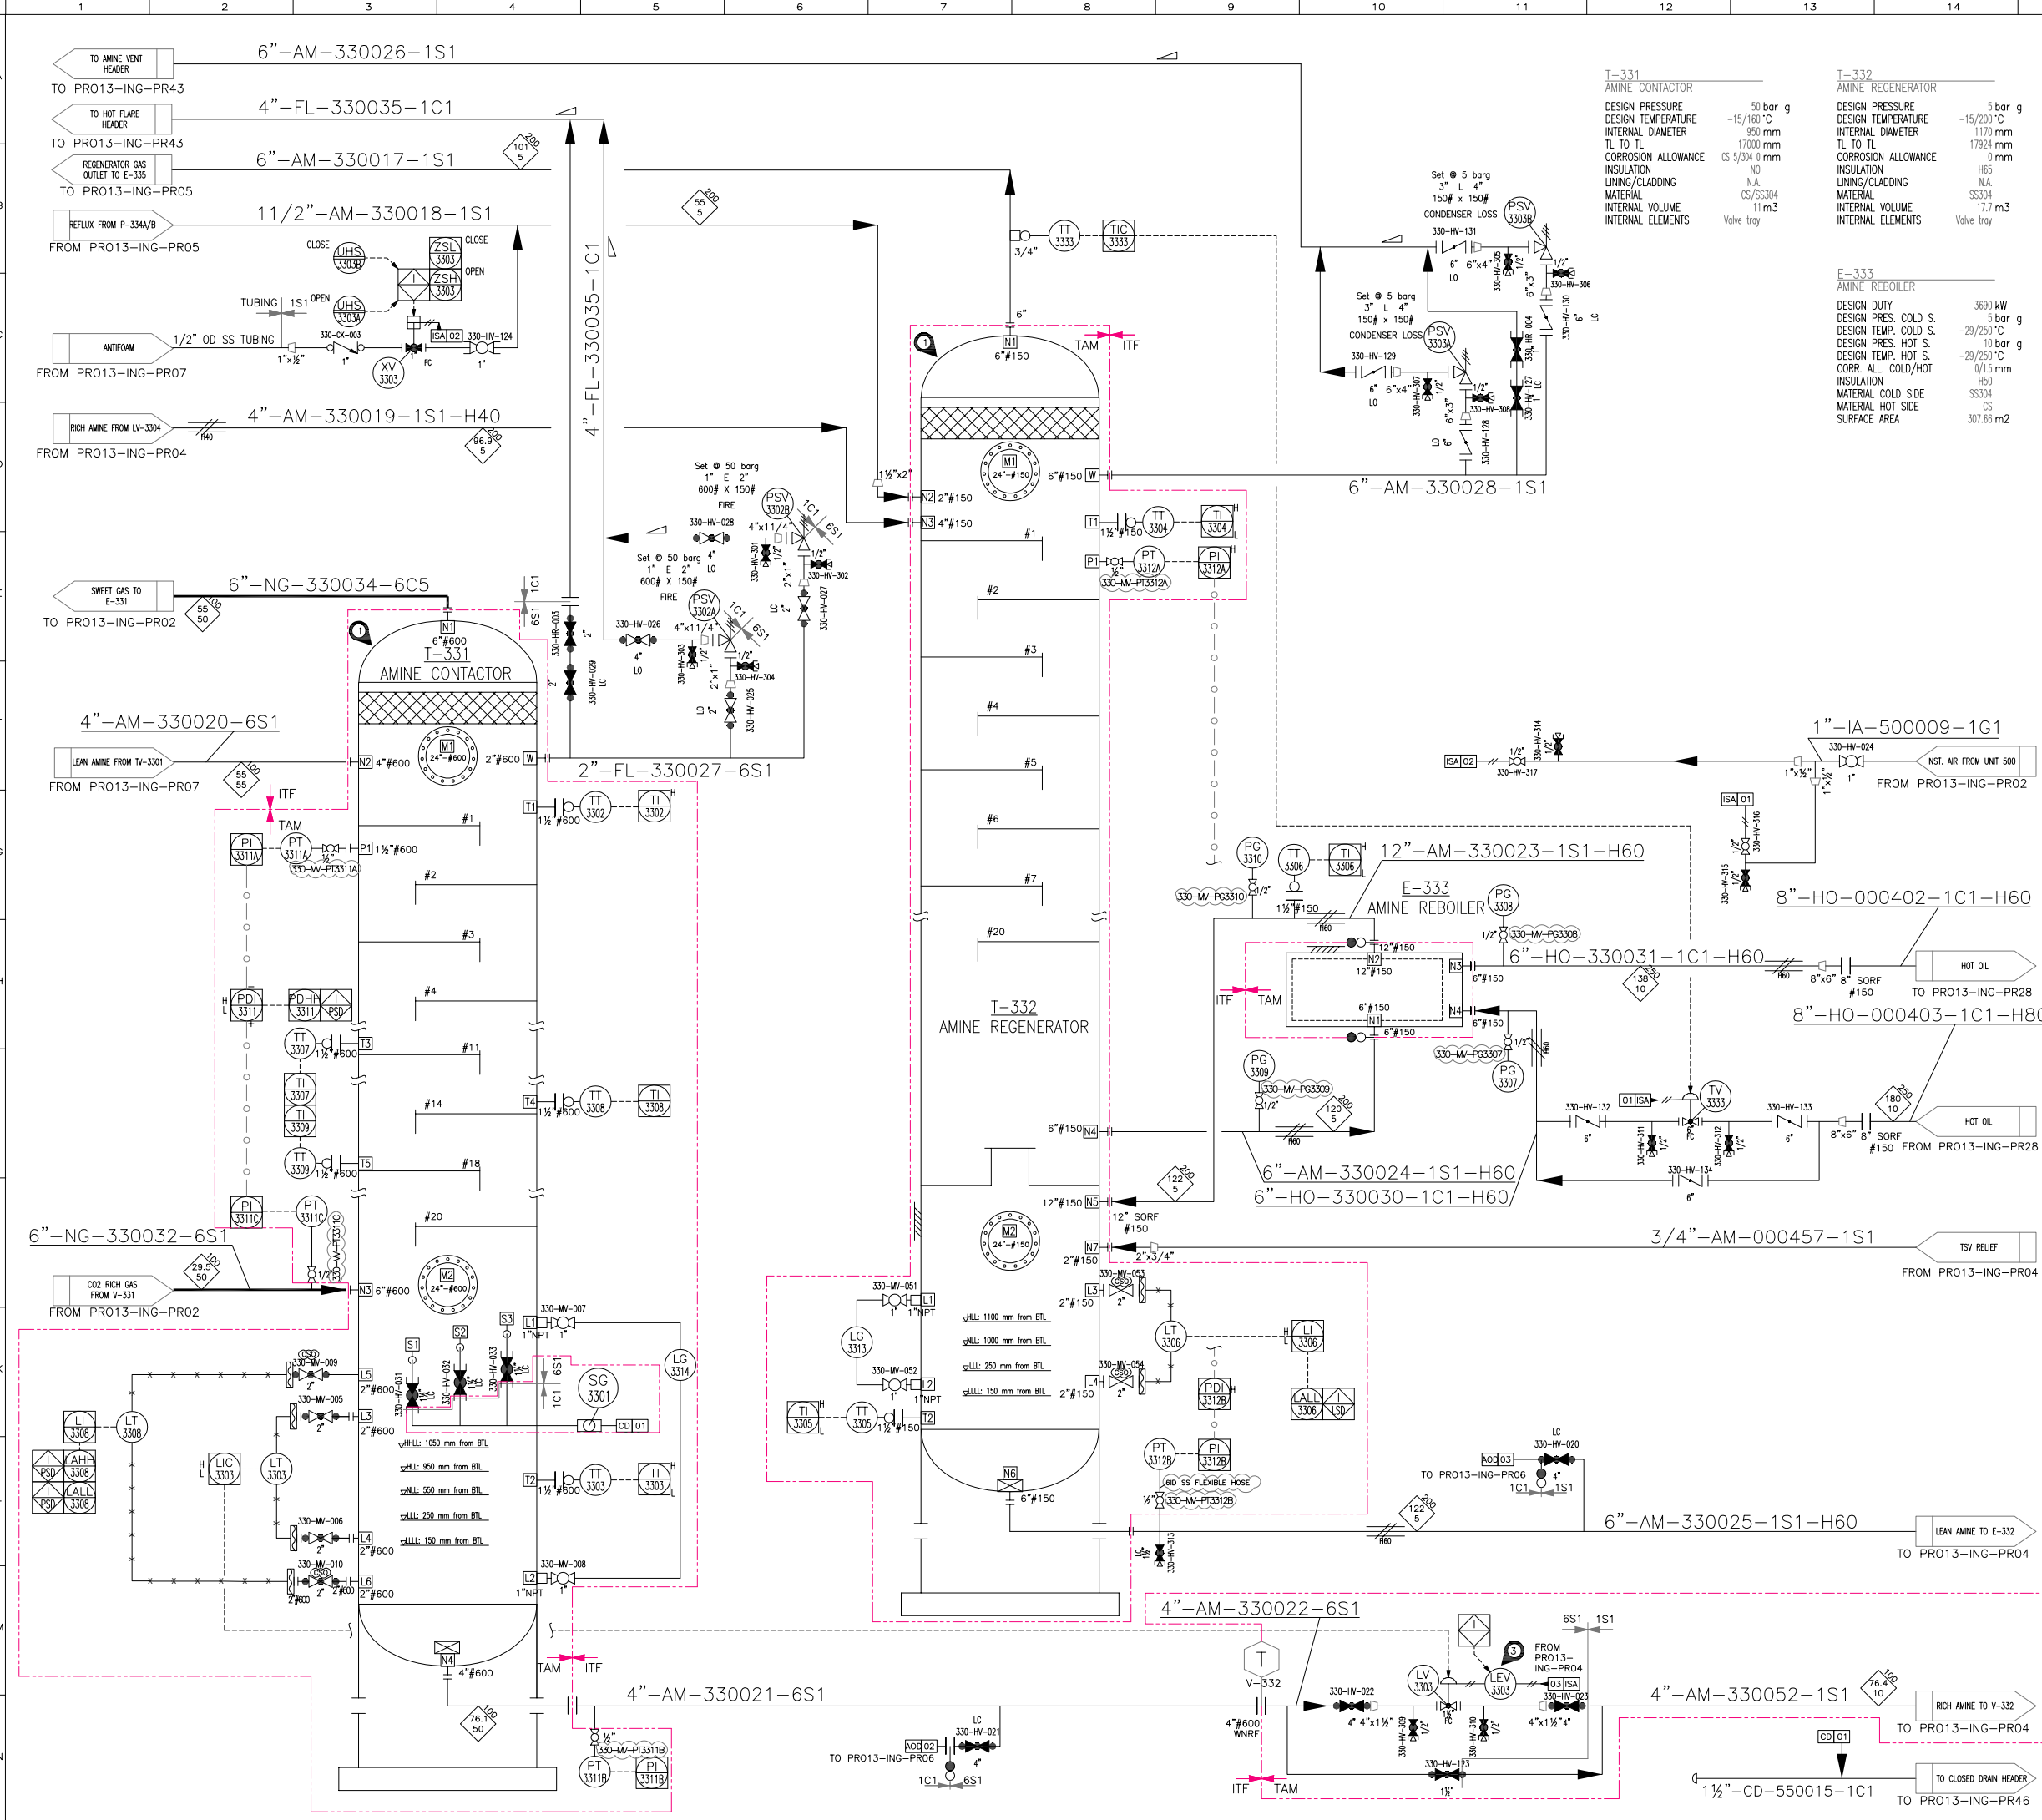

REFERENCE DOCUMENTS				
P&ID LEGEND		PRO13-ING-PRO0		
PROCESS FLOW DIAGRAM		21044-PR-PID-00000		
UTILITY FLOW DIAGRAM		PRO10-ING-PRO1/02/03/04		
MATERIAL SELECTION DIAGRAM		PRO10-ING-PRO5/11/12		
		21044-PR-PFD-00001		
		PRO08-ING-FR01		
		21044-PR-MSD-00001		

- ☒ ISA 001 INSTRUMENT SUPPLY AIR
- ☒ AOD 001 AMINE DRAIN
- ☒ FL 001 VENT TO FLARE HEADER

- NOTES
- 1 ALL INSTRUMENTS SHALL BE VISIBLE FROM GRADE.
 - 2 AMINE SHALL BE ANALYZED WEEKLY TO ASSURE PROPER QUALITY. SAMPLING POINT TO BE DEFINED.
 - 3 FIRESAFE GLOBE VALVE
 - 4 ALL INSTRUMENTS AND MANUAL VALVES ON THIS P&ID AND OUT OF SCOPE LIMITS WILL BE SUPPLIED BY TAM AS LOOSE ITEMS.

----- TAM SUPPLY LIMIT

8	27 Mar 2026	APPROVED FOR CONSTRUCTION	TAM (JB)	TAM (MM)	LOAMPLONE
7	05 Mar 2026	APPROVED FOR CONSTRUCTION	TAM (JB)	LOAMPLONE	W.BOUJALI
6	20 Feb 2026	APPROVED FOR CONSTRUCTION	TAM (JB)	LOAMPLONE	W.BOUJALI
5	09 Sep 2025	APPROVED FOR CONSTRUCTION	TAM (LD)	LOAMPLONE	W.BOUJALI
4	15 Feb 2024	APPROVED FOR CONSTRUCTION	TAM (LD)	LOAMPLONE	W.BOUJALI
3	18 Aug 2023	ISSUED FOR APPROVAL	TAM (LD)	LOAMPLONE	W.BOUJALI
2	08 Nov 2022	ISSUED FOR APPROVAL	TAM (LD)	LOAMPLONE	W.BOUJALI
1	21 Jul 2022	ISSUED FOR APPROVAL	TAM (ES)	TAM (LD)	LOAMPLONE
	24 Jun 2022	ISSUED FOR APPROVAL	TAM (ES)	TAM (LD)	LOAMPLONE
Rev.	Date	Description	Draft	Check'd	Approved
Customer: MANAENERGY			Offices: Mahaj Riad Center, Batiment 6, Jeme etage, Avenue Al Az, Hay Ryad, 10100 Rabat, Morocco		
Contractor: ITALFLUID			Offices: VIA VIVALDI,4 MONTESSILVANO (ITALY) Tel:+39 085 4224374 fax+39 085 4220742		
Engineering: ITALFLUID			Offices: VIA VIVALDI,4 MONTESSILVANO (ITALY) Tel:+39 085 4224374 fax+39 085 4220742		
Technology Vendor: TECHNICAL AMERICA INC			Offices: 301 N Smith Avenue, 92880 Corona, California (USA) Ph:+1 951 272 9540		
TITLE: LNG TENDRARA PLANT			OBJECT: P&ID - SWEETENING		
UNIT 330 T-331/T-332/E-333					
TYPE	SCALE	DOCUMENTS ID:	VENDOR DOC. CODE		SHEET/OF
A1	N/A	PRO13-ING-PRO3	21044-PR-PID-33002		1/1