


V-332
RICH AMINE SEPARATOR

DESIGN PRESSURE 10 bar g
DESIGN TEMPERATURE -15/100 °C
INTERNAL DIAMETER 1893 mm
SM TO SM 7850 mm
CORROSION ALLOWANCE 0 mm
INSULATION H (15 mm)
MATERIAL SS304
INTERNAL VOLUME 23.8 m3
INTERNAL ELEMENTS -

E-332
RICH/LEAN AMINE HEAT EXCHANGER

DESIGN DUTY 1512 kW
DESIGN PRES. COLD S. 10 bar g
DESIGN TEMP. COLD S. -29/160 °C
DESIGN PRES. HOT S. 10 bar g
DESIGN TEMP. HOT S. -29/160 °C
CORR. ALL. COLD/HOT 0/0 mm
INSULATION H (50 mm)
MATERIAL COLD SIDE PLATES SS316
MATERIAL HOT SIDE PLATES SS316
SURFACE AREA HOLD m2

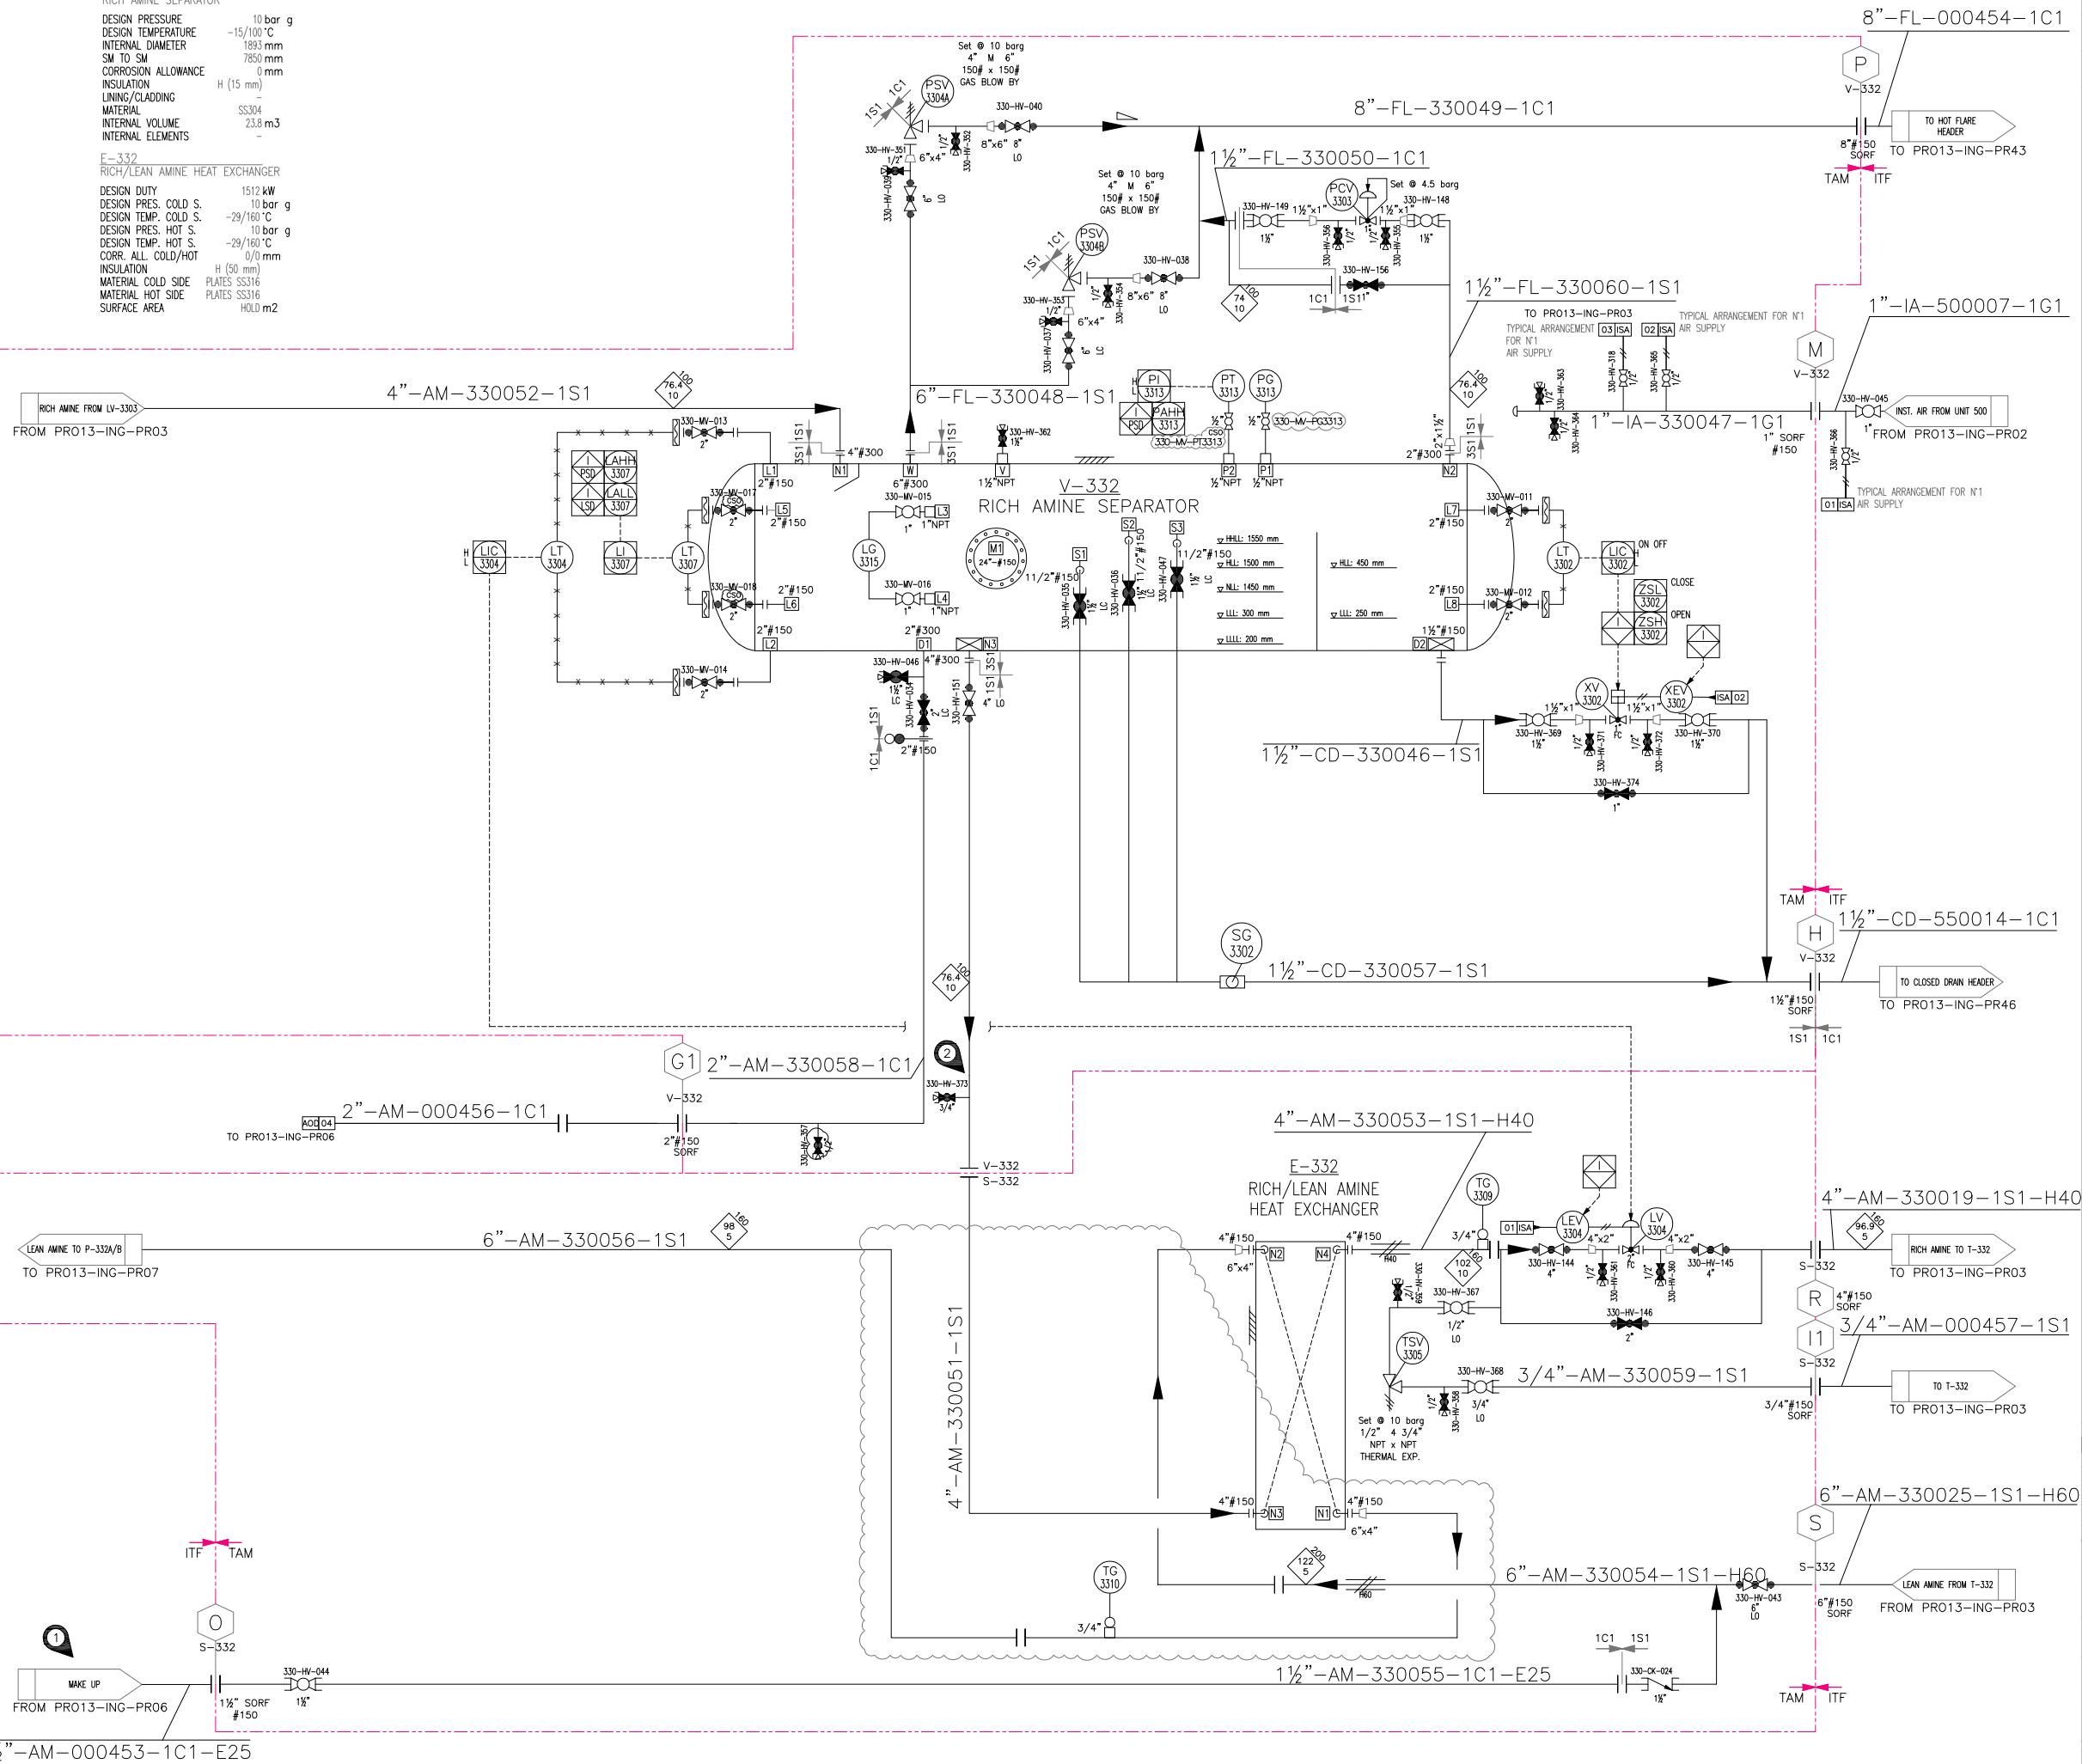

REFERENCE DOCUMENTS

P&ID LEGEND	PRO13-ING-PRO0 21044-PR-PID-00000
PROCESS FLOW DIAGRAM	PRO10-ING-PRO1/02/03/04 21044-PR-PFD-00001
UTILITY FLOW DIAGRAM	PRO10-ING-FR11/12 21044-PR-UFD-00001
MATERIAL SELECTION DIAGRAM	PRO08-ING-FR01 21044-PR-MSD-00001

ISA0X INSTRUMENT SUPPLY AIR
A020X AMINE DRAIN

NOTES:

- MANUAL AMINE AND WATER MAKE UP SHALL BE DONE WEEKLY IF NECESSARY BASED ON WEEKLY AMINE ANALYSIS.
- AMINE SAMPLING POINT.
- DESIGN AND EXECUTION OF ELECTRICAL TRACING BY ITF.

----- TAM SUPPLY LIMIT

6	27 Mar 2026	APPROVED FOR CONSTRUCTION	TAM (JB)	TAM (MM)	LOAMPLONE
5	09 Sep 2025	APPROVED FOR CONSTRUCTION	TAM (LD)	LOAMPLONE	W.BOUJALI
4	15 Feb 2024	APPROVED FOR CONSTRUCTION	TAM (LD)	LOAMPLONE	W.BOUJALI
3	18 Aug 2023	ISSUED FOR APPROVAL	TAM (LD)	LOAMPLONE	W.BOUJALI
2	02 Nov 2022	ISSUED FOR APPROVAL	TAM (LD)	LOAMPLONE	W.BOUJALI
1	21 Jul 2022	ISSUED FOR APPROVAL	TAM (LD)	LOAMPLONE	W.BOUJALI
0	24 Jun 2022	ISSUED FOR APPROVAL	TAM (LD)	LOAMPLONE	W.BOUJALI
Rev.	Date	Description	Draft	Check'd	Approved
Customer: MANAENERGY					
Contractor: ITALFLUID					
Engineering: ITALFLUID					
Technology Vendor: TECHNICAL AMERICA INC					
OFFICES: Mahaj Riad Center, Batiment 6, 3eme etage, Avenue Al Az, Hay Ryad, 10100 Rabat, Morocco					
OFFICES: VIA VIVALDI,4 MONTESILVANO (ITALY) Tel.+39 085 4224374 fax+39 085 4220742					
OFFICES: VIA VIVALDI,4 MONTESILVANO (ITALY) Tel.+39 085 4224374 fax+39 085 4220742					
OFFICES: 301 N Smith Avenue, 92880 Corona, California (USA) Ph:+1 951 272 9540					
TITLE: LNG TENDRARA PLANT			OBJECT: P&ID - SWEETENING UNIT 330 SKID S-332		
TYPE	SCALE	DOCUMENTS ID:	VENDOR DOC. CODE		
A1	N/A	PRO13-ING-PR04	21044-PR-PID-33003		
SHEET/OF					1/1