


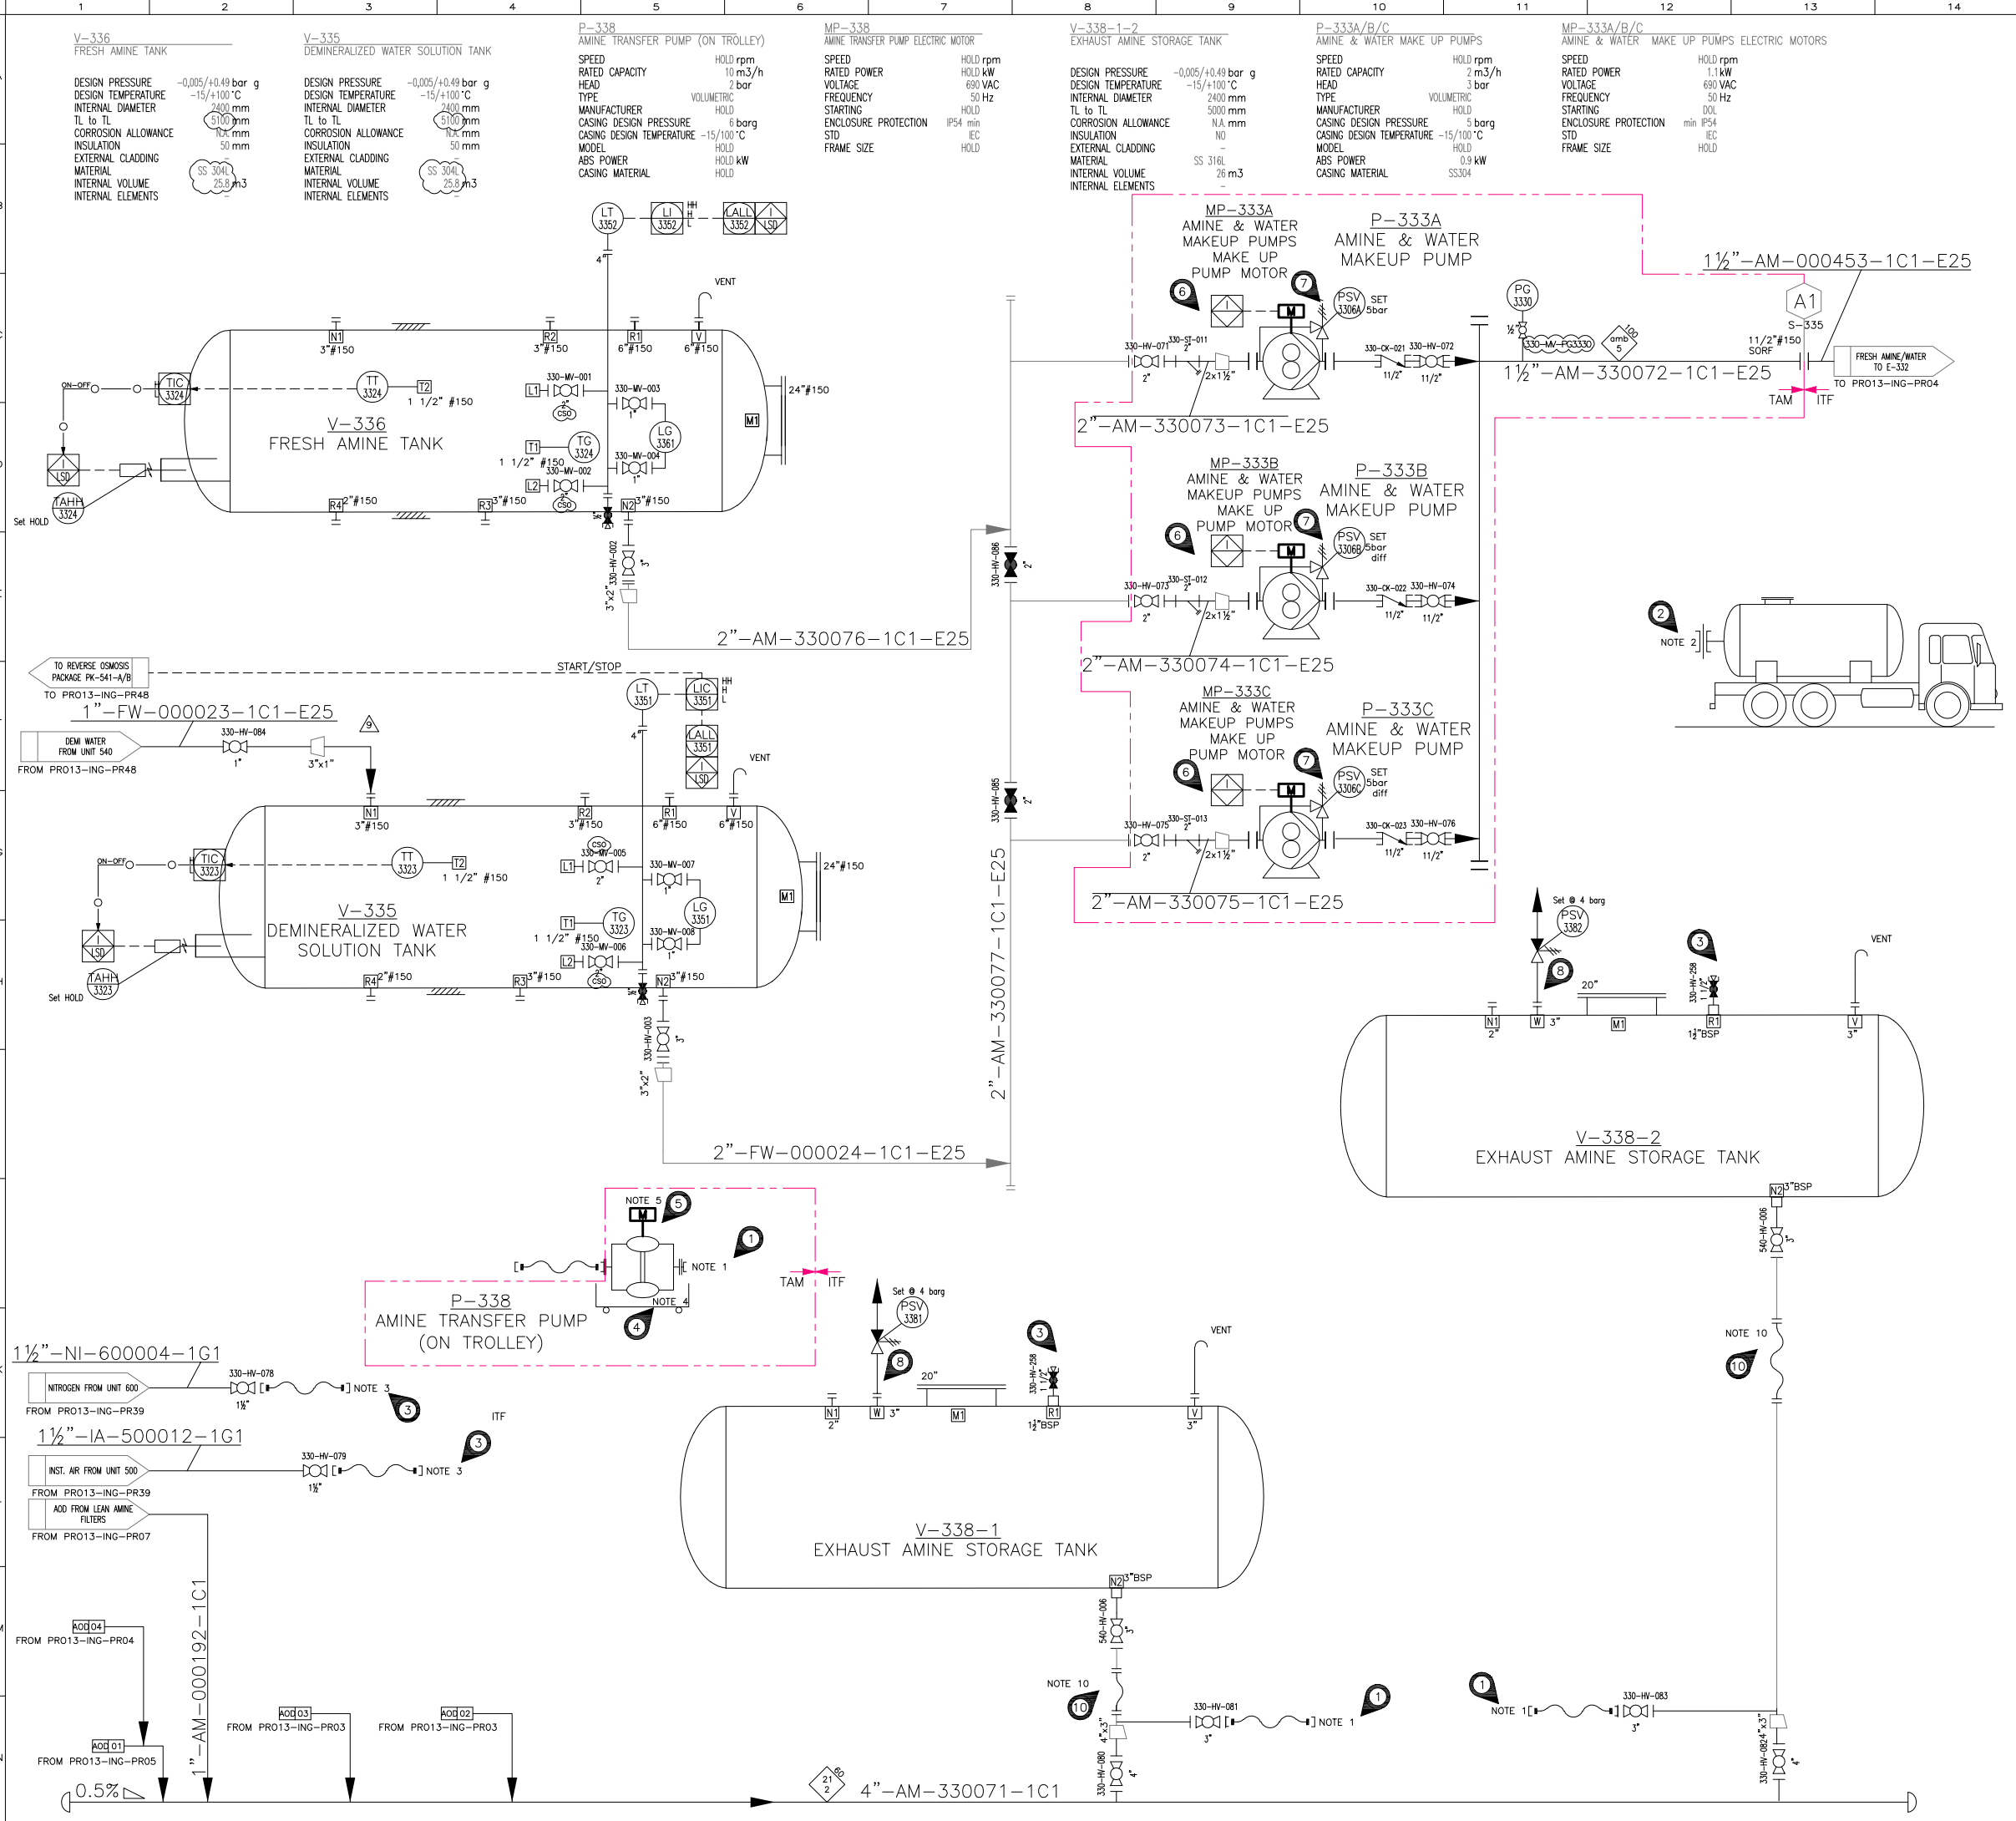

REFERENCE DOCUMENTS	
P&ID LEGEND	PRO13-ING-PRO0
PROCESS FLOW DIAGRAM	21044-PR-PID-00000
UTILITY FLOW DIAGRAM	PRO10-ING-PRO1/02/03/04
MATERIAL SELECTION DIAGRAM	21044-PR-PFD-00001
	PRO10-ING-PR11/13
	21044-PR-UFD-00001
	PRO08-ING-FR01
	21044-PR-MSD-00001

AMINE DRAIN

- NOTES:
- P-338 PUMP CAN BE ATTACHED TO V-338-1 OR V-338-2 WITH A HOSE.
 - A TRUCK ALSO COULD BE ATTACHED TO BOTH VESSELS BY MEANS OF A HOSE.
 - AIR AND NITROGEN CAN BE SUPPLIED TO ALL VESSELS BY MEANS OF A HOSE. AIR AND NITROGEN WILL HAVE DIFFERENT FITTINGS.
 - P-338 WILL BE MOUNTED ON A PLATFORM TROLLEY.
 - P-338 WILL BE CONNECTED WITH EXTENSION CORD TO A LOCAL UTILITY STATION PLUG. THE PUMP WILL BE MANUAL OPERATED WITH LOCAL PUSH BUTTON.
 - MANUAL AMINE AND WATER MAKE UP SHALL BE DONE WEEKLY IF NECESSARY BASED ON WEEKLY AMINE ANALYSIS.
 - PUMPS WILL BE EQUIPPED WITH ELECTRICAL TRACING AND INSULATION (50mm)
 - PRESSURE RELIEF VALVE (SPRING LOADED) PROVIDED WITH ISOTANK.
 - POSITION AND INSTALLATION TO BE DEFINED BY VENDOR.
 - FLANGED FLEXIBLE HOSE TO ALLOW REMOVAL OF FULL TANK AND REPLACEMENT WITH AN EMPTY TANK
- TAM SUPPLY LIMIT

10	02 Apr 2026	APPROVED FOR CONSTRUCTION	TAM (JB)	TAM (MM)	LCAMPLONE
9	23 Jan 2026	APPROVED FOR CONSTRUCTION	M.RAUSA	LCAMPLONE	W.BOUJALI
8	17 Jun 2025	APPROVED FOR CONSTRUCTION	P.MARZIANI	LCAMPLONE	W.BOUJALI
7	27 Mar 2025	APPROVED FOR CONSTRUCTION	P.MARZIANI	LCAMPLONE	W.BOUJALI
6	23 Jan 2025	APPROVED FOR CONSTRUCTION	P.MARZIANI	LCAMPLONE	W.BOUJALI
5	14 Oct 2024	APPROVED FOR CONSTRUCTION	TAM (LD)	LCAMPLONE	W.BOUJALI
4	08 Feb 2024	APPROVED FOR CONSTRUCTION	TAM (LD)	LCAMPLONE	W.BOUJALI
3	30 Apr 2023	ISSUED FOR APPROVAL	TAM (LD)	LCAMPLONE	W.BOUJALI
2	02 Nov 2022	ISSUED FOR APPROVAL	TAM (LD)	LCAMPLONE	W.BOUJALI
1	21 Jul 2022	ISSUED FOR APPROVAL	TAM (LD)	TAM (MM)	LCAMPLONE
0	24 Jun 2022	ISSUED FOR APPROVAL	TAM (LD)	TAM (MM)	LCAMPLONE
Rev.	Date	Description	Draft	Check'd	Approved
Customer: MANAENERGY			Offices: Mahaj Riad Center, Batiment 6, Jeme etage, Avenue Al Az, Hay Ryad, 10100 Rabat, Morocco		
Contractor: ITALFLUID			Offices: VIA VIVALDI,4 MONTESILVANO (ITALY) Tel.+39 085 4224374 fax+39 085 4220742		
Engineering: ITALFLUID			Offices: VIA VIVALDI,4 MONTESILVANO (ITALY) Tel.+39 085 4224374 fax+39 085 4220742		
Technology Vendor: TECHNICAL AMERICA INC			Offices: 301 N Smith Avenue, 92880 Corona, California (USA) Ph.+1 951 272 9540		
TITLE: LNG TENDRARA PLANT			OBJECT: P&ID - SWEETENING UNIT 330 AMINE UTILITIES / S-335		
TYPE	SCALE	DOCUMENTS ID	VENDOR DOC. CODE		SHEET/OF
A1	N/A	PRO13-ING-PRO6	21044-PR-PID-33005		1/1