


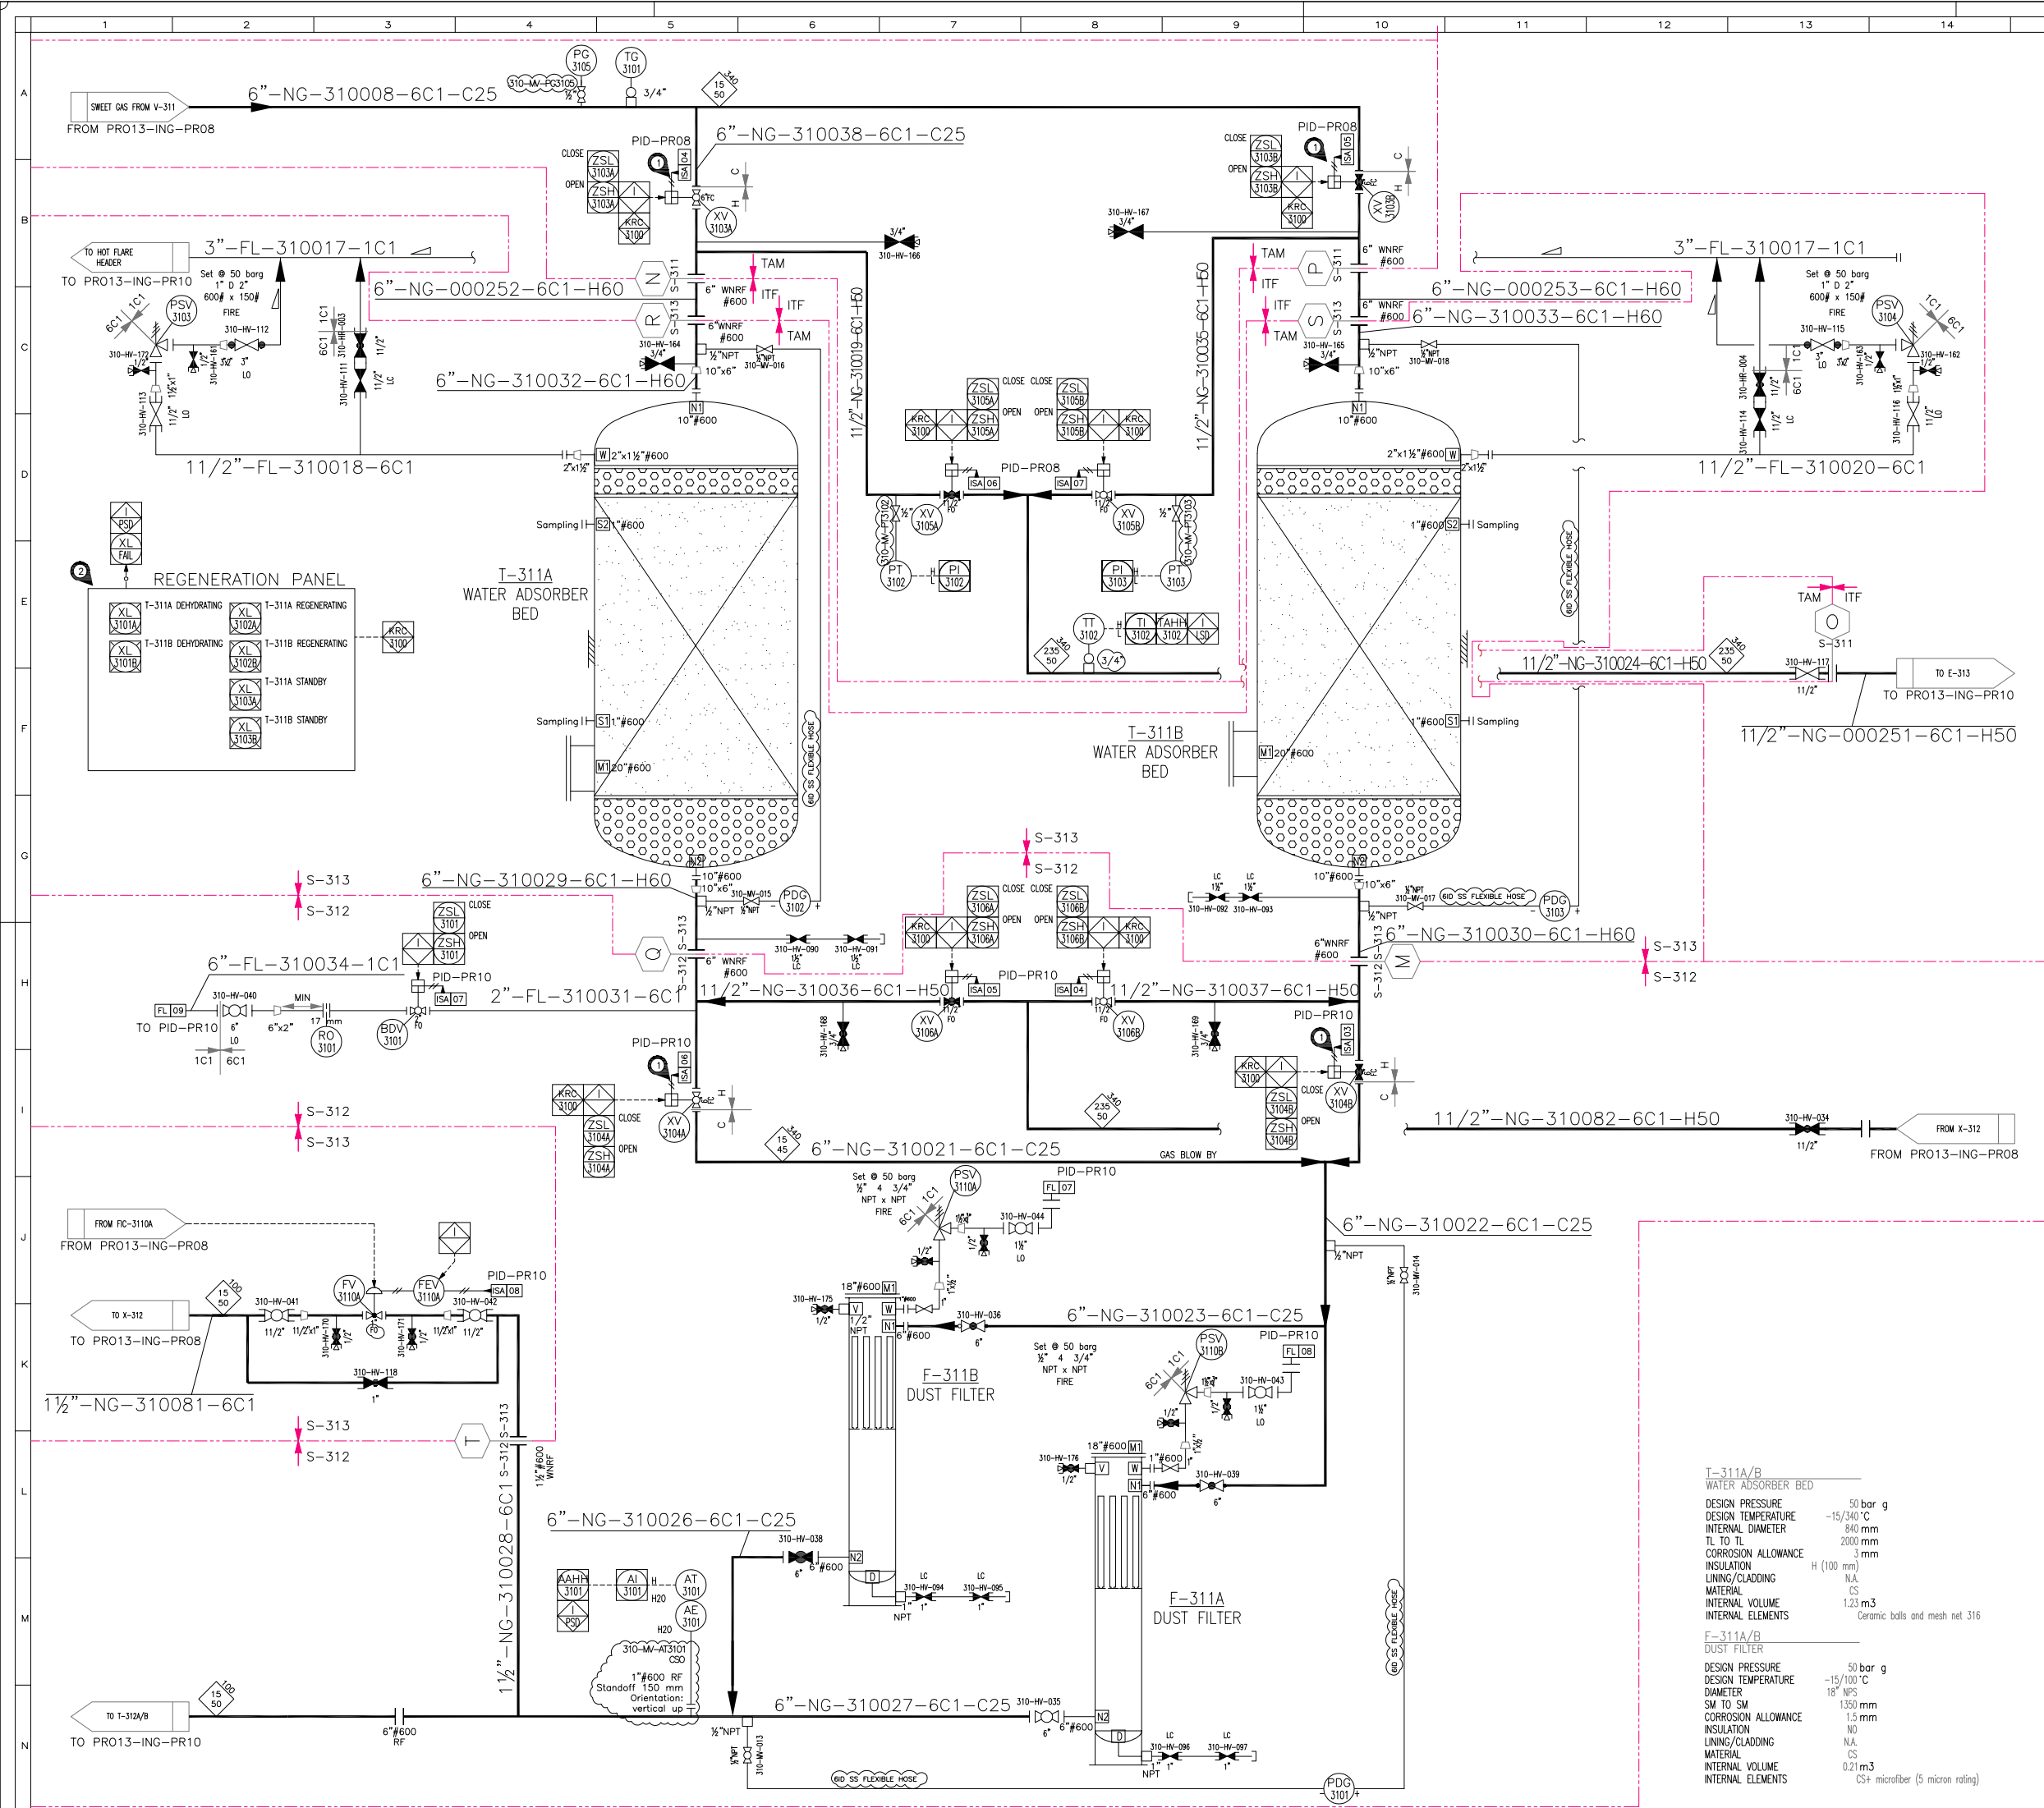

REFERENCE DOCUMENTS	
P&ID LEGEND	PRO13-ING-PRO0
PROCESS FLOW DIAGRAM	21044-PR-PID-00000
UTILITY FLOW DIAGRAM	PRO10-ING-PRO1/02/03/04
MATERIAL SELECTION DIAGRAM	21044-PR-PFD-00001
	PRO10-ING-PR12
	21044-PR-UFD-00001
	PRO08-ING-FR01
	21044-PR-MSD-00001

- ISA0X INSTRUMENT SUPPLY AIR
- FL0X VENT TO FLARE HEADER
- CD0X CLOSED DRAIN TO DRAIN HEADER

- NOTES
1. DURING VALVE PROCUREMENT WE DECIDE THE FINAL VALVE CONFIGURATION (GLOBE, BALL OR BUTTERFLY)
2. REGENERATION PROCESS STEPS
1. CHANGE OVER, PUTTING FRESH UNIT ON-LINE BEFORE ISOLATING SPENT COLUMN.
5 MINUTES
 2. PRESSURE CHANGE MAX 50 PSI/MIN = 0.833 PSI/SEC (3 BAR/MIN=0.05BAR/SEC).
5 MINUTES
 3. RAMP UP HEATING INLET TEMP OVER 5 MINUTES TO 232°C.
5 MINUTES
 4. HEAT COLUMN AT 232°C.
168 MINUTES
 5. COOL COLUMN TO WITHIN 16°C OF FEED TEMPERATURE.
66 MINUTES
 6. STAND BY TIME.
111 MINUTES
- ALL INSTRUMENTS AND MANUAL VALVES ON THIS P&ID WILL BE SUPPLIED BY TAM.

----- TAM SUPPLY LIMIT

6	31 Mar 2026	APPROVED FOR CONSTRUCTION	TAM (JB)	TAM (MM)	LOCOMPLONE
5	15 Jul 2025	APPROVED FOR CONSTRUCTION	TAM (LD)	LOCOMPLONE	W.BOUALAI
4	15 Feb 2024	APPROVED FOR CONSTRUCTION	TAM (LD)	LOCOMPLONE	W.BOUALAI
3	25 Jul 2023	ISSUED FOR APPROVAL	TAM (LD)	LOCOMPLONE	W.BOUALAI
2	02 Nov 2022	ISSUED FOR APPROVAL	TAM (LD)	LOCOMPLONE	W.BOUALAI
1	21 Jul 2022	ISSUED FOR APPROVAL	TAM (ES)	LOCOMPLONE	W.BOUALAI
0	28 Jun 2022	ISSUED FOR APPROVAL	TAM (ES)	LOCOMPLONE	W.BOUALAI
Rev.	Date	Description	Draft	Check'd	Approved
Customer: MANAENERGY					
Contractor: ITALFLUID					
Engineering: ITALFLUID					
Technology Vendor: TECHNICAL AMERICA INC					
OFFICES: Mahaj Riad Center, Batiment 6, 3eme etage, Avenue Al Az, Hay Ryad, 10100 Rabat, Morocco					
OFFICES: VIA VIVALDI,4 MONTESILVANO (ITALY) Tel.+39 085 4224374 fax+39 085 4220742					
OFFICES: VIA VIVALDI,4 MONTESILVANO (ITALY) Tel.+39 085 4224374 fax+39 085 4220742					
OFFICES: 301 N Smith Avenue, 92880 Corona, California (USA) Ph.+1 951 272 9540					
TITLE: LNG TENDRARA PLANT			OBJECT: P&ID DEHYDRATION UNIT 310 S-313/ S-312		
TYPE	SCALE	DOCUMENTS ID:	VENDOR DOC. CODE		
A1	N/A	PRO13-ING-PRO9	21044-PR-PID-31002		
					SHEET/OF 1/1