


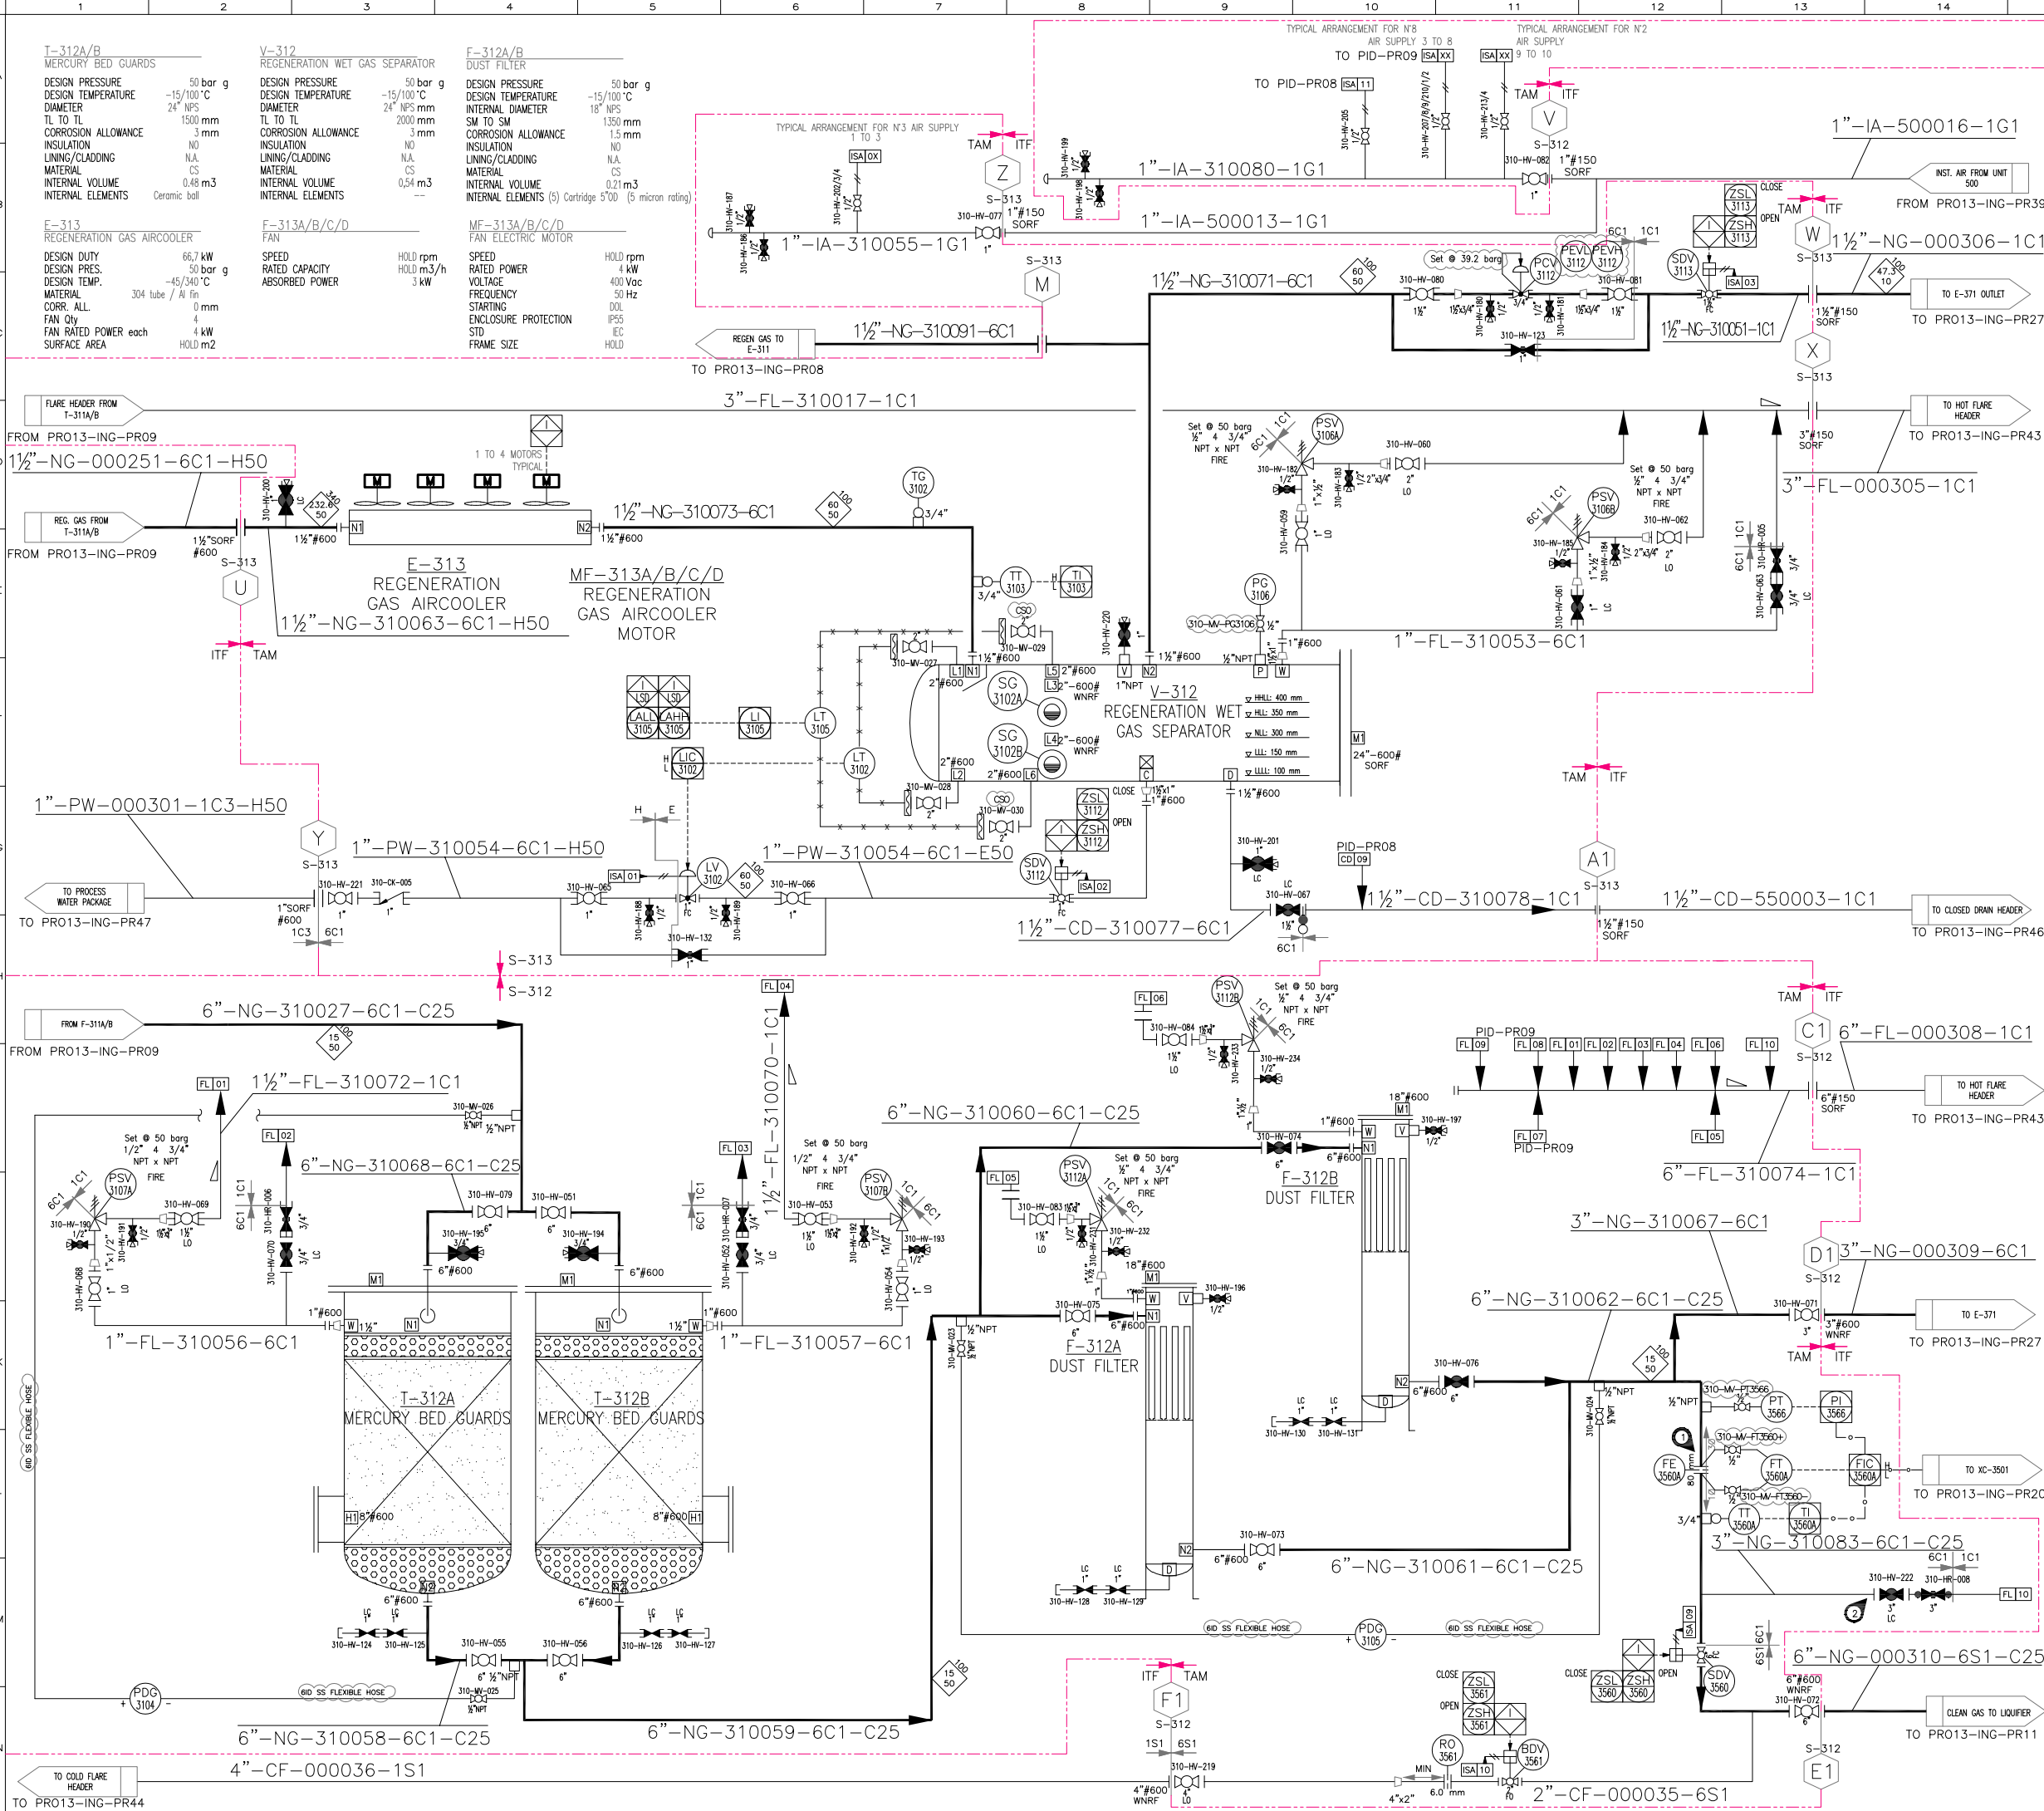

15	16	17	18
REFERENCE DOCUMENTS			
P&ID LEGEND		PRO13-ING-PRO0 21044-PR-PID-00000	
PROCESS FLOW DIAGRAM		PRO10-ING-PRO1/02/03/04 21044-PR-PFD-00001	
UTILITY FLOW DIAGRAM		PRO10-ING-PR11/12 21044-PR-UFD-00001	
MATERIAL SELECTION DIAGRAM		PRO08-ING-FR01 21044-PR-MSD-00001	
ISA 0X INSTRUMENT SUPPLY AIR FL 0X VENT TO FLARE HEADER CD 0X CLOSED DRAIN TO DRAIN HEADER			
NOTES			
1 COMPACT CONDITIONING ORIFICE PLATE FLOW METER EMERSON 4 HOLES ORIFICE PLATE. 2 VENT TO FLARE FOR START UP FOR PRESSURIZING UNIT 310. THIS LINE IS DESIGNED FOR 50% OF DESIGN FLOWRATE. 3 DESIGN AND EXECUTION OF ELECTRICAL TRACING BY ITF.			
----- TAM SUPPLY LIMIT			

6	30 Mar 2026	APPROVED FOR CONSTRUCTION	TAM (JB)	TAM (JM)	LCAMPLONE
5	15 Jul 2025	APPROVED FOR CONSTRUCTION	TAM (LD)	LCAMPLONE	WBOULAU
4	15 Feb 2024	APPROVED FOR CONSTRUCTION	TAM (LD)	LCAMPLONE	WBOULAU
3	25 Jul 2023	ISSUED FOR APPROVAL	TAM (LD)	LCAMPLONE	WBOULAU
2	08 Nov 2022	ISSUED FOR APPROVAL	TAM (LD)	LCAMPLONE	WBOULAU
1	21 Jul 2022	ISSUED FOR APPROVAL	TAM (ES)	LCAMPLONE	WBOULAU
0	28 Jun 2022	ISSUED FOR APPROVAL	TAM (ES)	LCAMPLONE	WBOULAU
Rev.	Date	Description	Draft	Check'd	Approved
Customer: MANAENERGY			OFFICES: Mahaq Riad Center, Batiment 6, 3eme etage, Avenue Al Arz, Hay Ryad, 10100 Rabat, Morocco		
Contractor: ITALFLUID			OFFICES: VIA VIVALDI,4 MONTESSILVANO (ITALY) Tel.+39 085 4224374 fax+39 085 4220742		
Engineering: ITALFLUID			OFFICES: VIA VIVALDI,4 MONTESSILVANO (ITALY) Tel.+39 085 4224374 fax+39 085 4220742		
Technology Vendor: TECHNICAL AMERICA INC			OFFICES: 301 N Smith Avenue, 92880 Corona, California (USA) Ph.+1 951 272 9540		
TITLE: LNG TENDRARA PLANT			OBJET: P&ID DEHYDRATION UNIT 310 SKID S-312/S-313		
TYPE	SCALE	DOCUMENTS ID:	VENDOR DOC. CODE		SHEET/OF
A1	N/A	PRO13-ING-PR10	21044-PR-PID-31003		1/1