


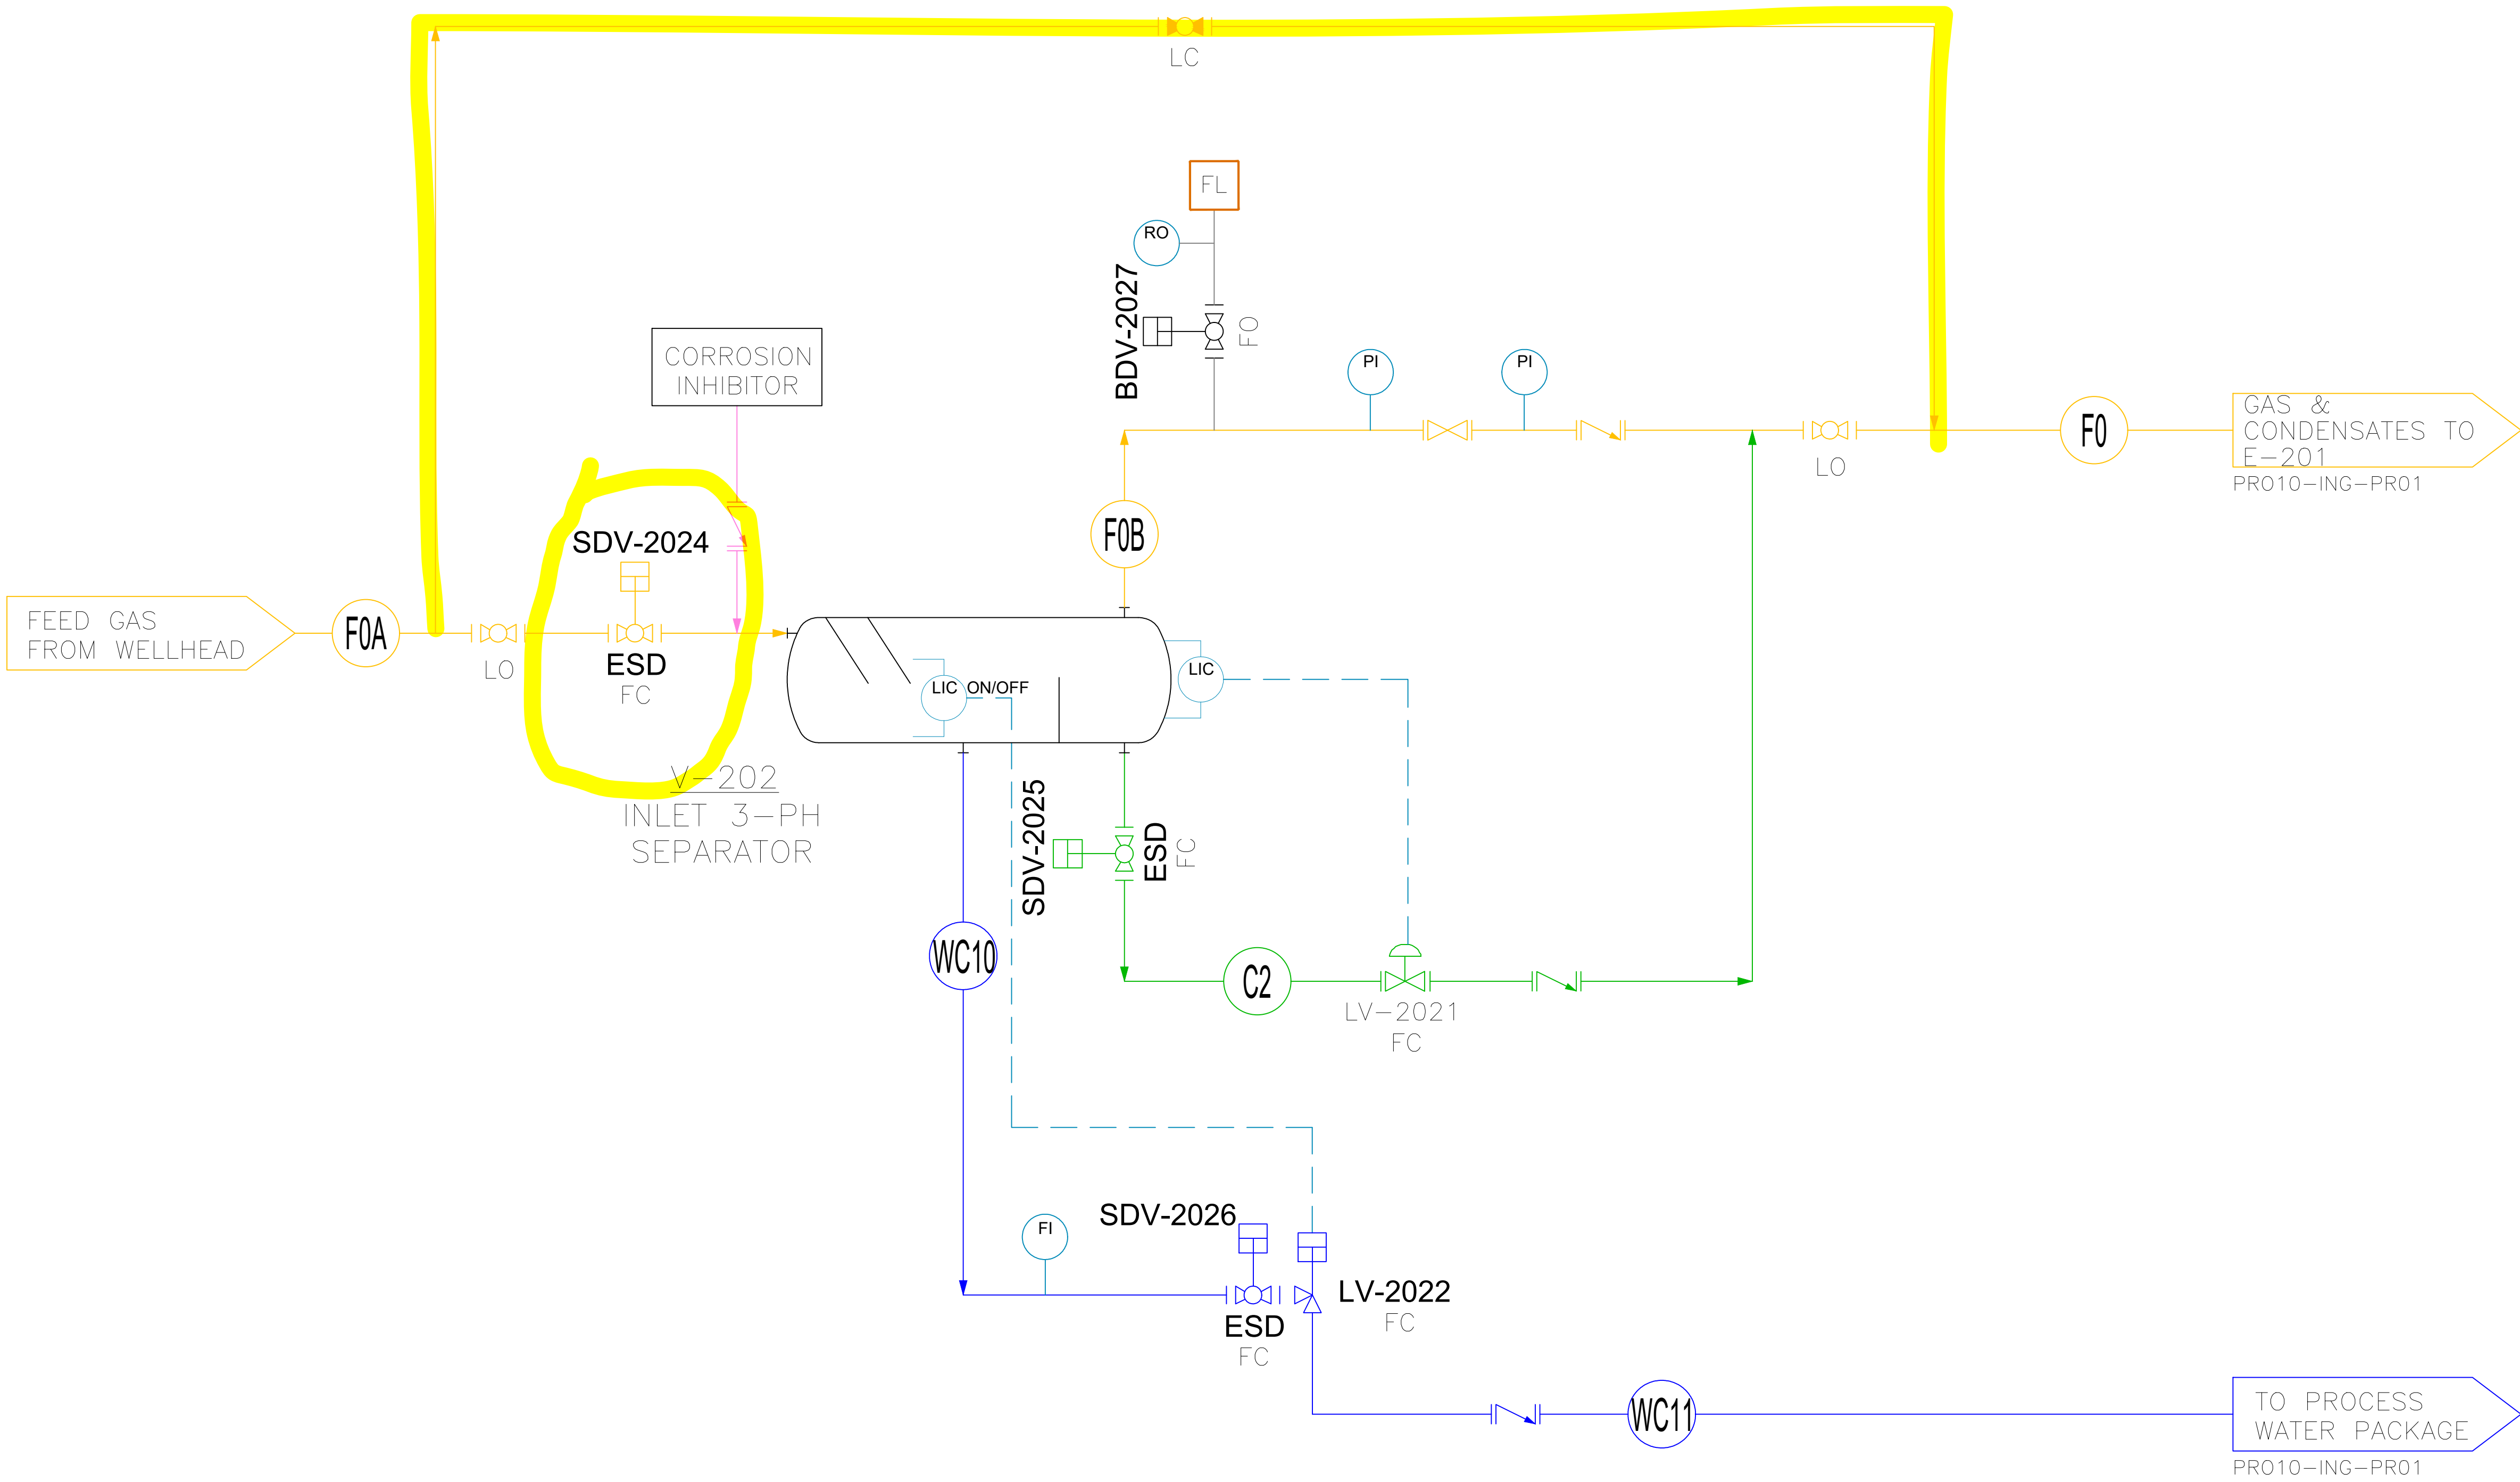

NOTES:

LEGEND:

FL TO FLARE SYSTEM

FLUID LIST

CONDENSATES	PSV
GAS	REFRIGERANT (AMMONIA)
PROCESS WATER	INSTRUMENTAL LINE
FRESH WATER	DIESEL
AMINE	INERT GAS
HOT OIL	MIXED REFRIGERANT
LNG	CHEMICAL

0	13 Apr 2023	ISSUED FOR APPROVAL	M.FERRARINI	L.CAMPIONE	W. BOULALI	
Rev.	Date	Description	Draft	Check'd(IFT)	App'd (MSP)	SOUND ENERGY
		Customer:	SOUND ENERGY			
		Contractor:	I.M.S.P. MOROCCO			
		Engineering:	ITALFLUID			
		Technology Vendor:	TECHNICAL AMERICA INC			
TITLE:		LNG TENDRARA PLANT		OBJET:		
				PROCESS FLOW DIAGRAM (INLET SEPARATOR)		
TYPE	SCALE	DOCUMENTS ID:	VENDOR DOC. CODE:		SHEET/OF	
A1	N/A	PRO10-ING-PR14	21044-PR-PFD-00001		1/1	

- NOTES:
- 1- FUEL GAS MAKE UP LINE / ADDITIONAL MAKEUP LINE UPSTREAM THIS BRANCH WILL ALSO BE PROVIDED TO ALLOW POWER GENERATION INDEPENDENT STARTUP

2- DESIGNED FOR WINTER CASE.

3- SEPARATOR CAN BE VERTICAL/HORIZONTAL. TO BE DECIDED BY TG DURING SKID DETAILED ENGINEERING.

4- UNIT 330 IS DESIGN TO WORK UNTIL 10% CO2 MAXIMUM.

5- LIQUID CONTROL USED ONLY FOR START-UP. AFTER START-UP MANUAL VALVE SHALL BE LOCKED CLOSED.

6- MANUAL AMINE AND WATER MAKEUP.

LEGEND:

- HO

FL

N2

CO2
- HOT OIL

TO FLARE SYSTEM

NITROGEN

CO2 RICH STREAM TO VENT HEADER (ATM)

FLUID LIST

- CONDENSATES

GAS

PROCESS WATER

FRESH WATER

AMINE

HOT OIL

LNG
- PSV

REFRIGERANT (AMMONIA)

INSTRUMENTAL LINE

DIESEL

INERT GAS

MIXED REFRIGERANT

7	4 Apr 2023	ISSUED FOR APPROVAL	TAM (LD)	I.CAMPLONE	W. BOULALI	
6	24 Jun 2022	ISSUED FOR APPROVAL	TAM (LD)	I.CAMPLONE	W. BOULALI	
5	25 Apr 2022	ISSUED FOR APPROVAL	TAM (LD)	I.CAMPLONE	W. BOULALI	
4	22 Feb 2021	PRELIMINARY ISSUE FOR TECHNICAL PROPOSED	M.FERRARINI	I.CAMPLONE	W. BOULALI	
3	15 Dec 2021	PRELIMINARY ISSUE FOR TECHNICAL PROPOSED	M.FERRARINI	I.CAMPLONE	W. BOULALI	
2	12 Mar 2021	PRELIMINARY ISSUE FOR TECHNICAL PROPOSED	M.FERRARINI	I.CAMPLONE	W. BOULALI	
1	24 Jan 2021	PRELIMINARY ISSUE FOR TECHNICAL PROPOSED	M.FERRARINI	I.CAMPLONE	W. BOULALI	
0	22 Sept 2020	PRELIMINARY ISSUE FOR TECHNICAL PROPOSED	M.FERRARINI	I.CAMPLONE	W. BOULALI	
Rev.	Date	Description	Draft	Check'd (ITF)	App'd (MSP)	SOUND ENERGY

Customer:
SOUND ENERGY

Contractor:
I.M.S.P. MOROCCO

Engineering:
ITALFLUID

Technology Vendor:
TECHNICAL AMERICA INC


OFFICES:
Espace les Patios 1st floor,
Avenue Annakhil Hay Riad, Rabat 10100


OFFICES:
Regus Maroc Twin Center, Tour Ouest, Casablanca
Tel:+39 085 4224374 fax+39 085 4220742

OFFICES:
VIA VIVALDI,4
Tel.+39 085 4224374 fax+39 085 4220742

OFFICES:
301 N Smith Avenue, 92880 Corona, California (USA)
Ph:+1 951 272 9540

TITLE: LNG TENDRARA PLANT			OBJET: PROCESS FLOW DIAGRAM (GAS SWEETENING)		
TYPE	SCALE	DOCUMENTS ID	VENDOR DOC. CODE	SHEET/OF	
A1	N/A	PRO10-ING-PR01	21044-PR-PFD-00001	1/1	

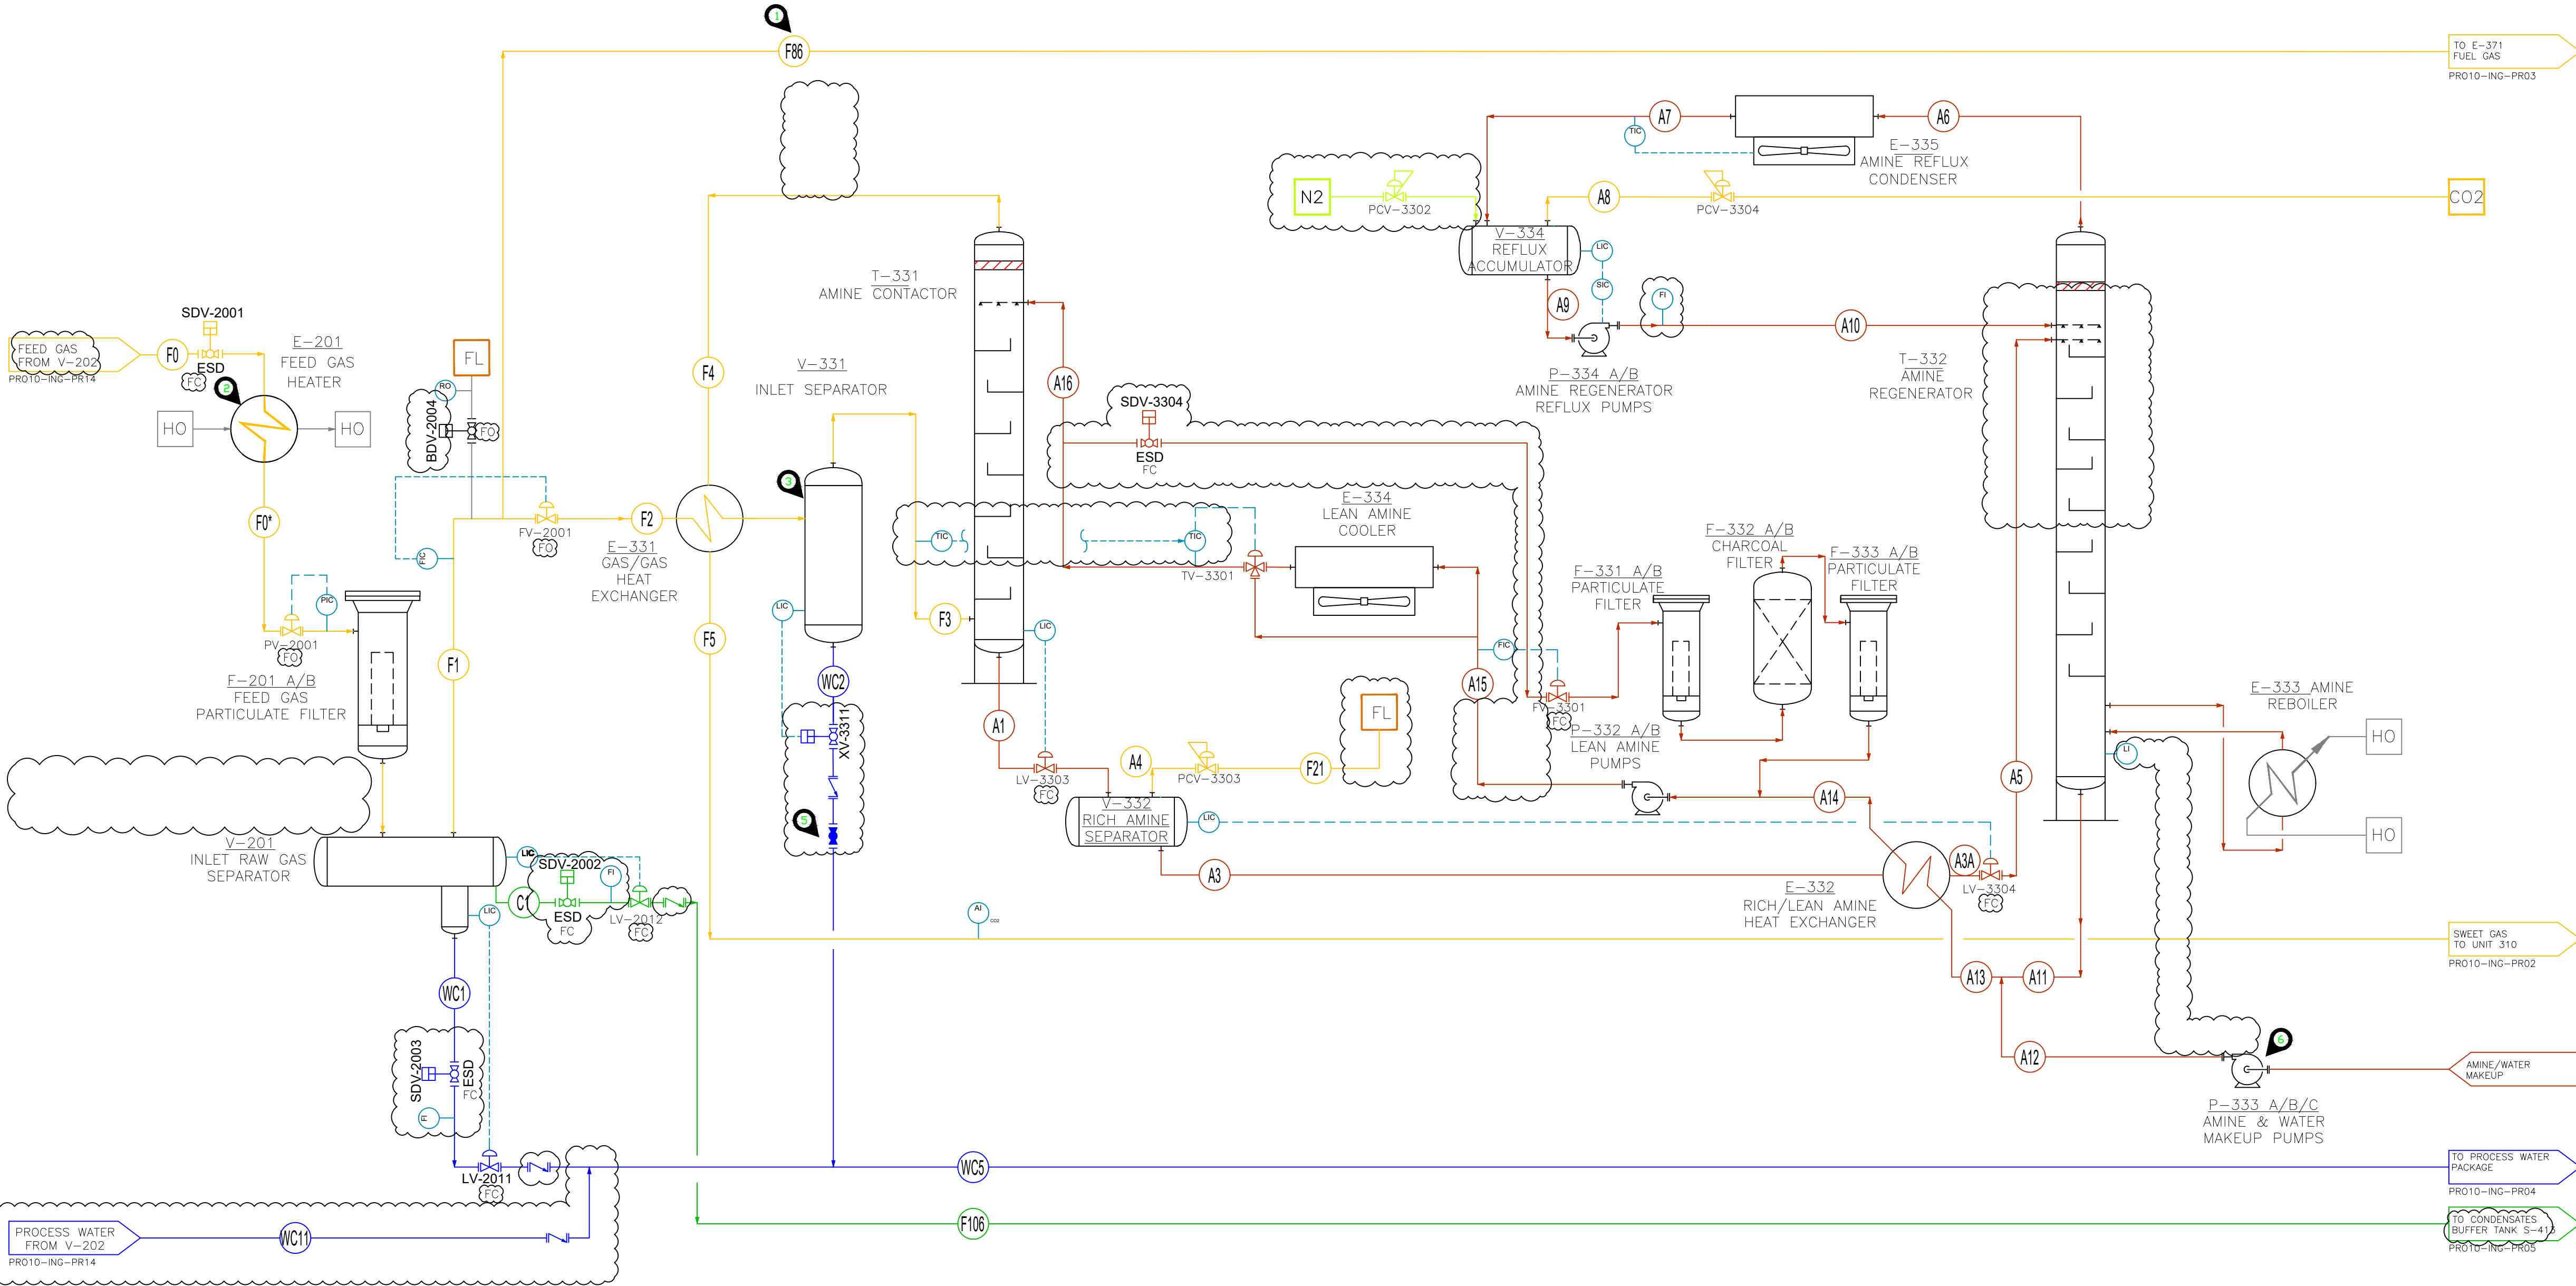

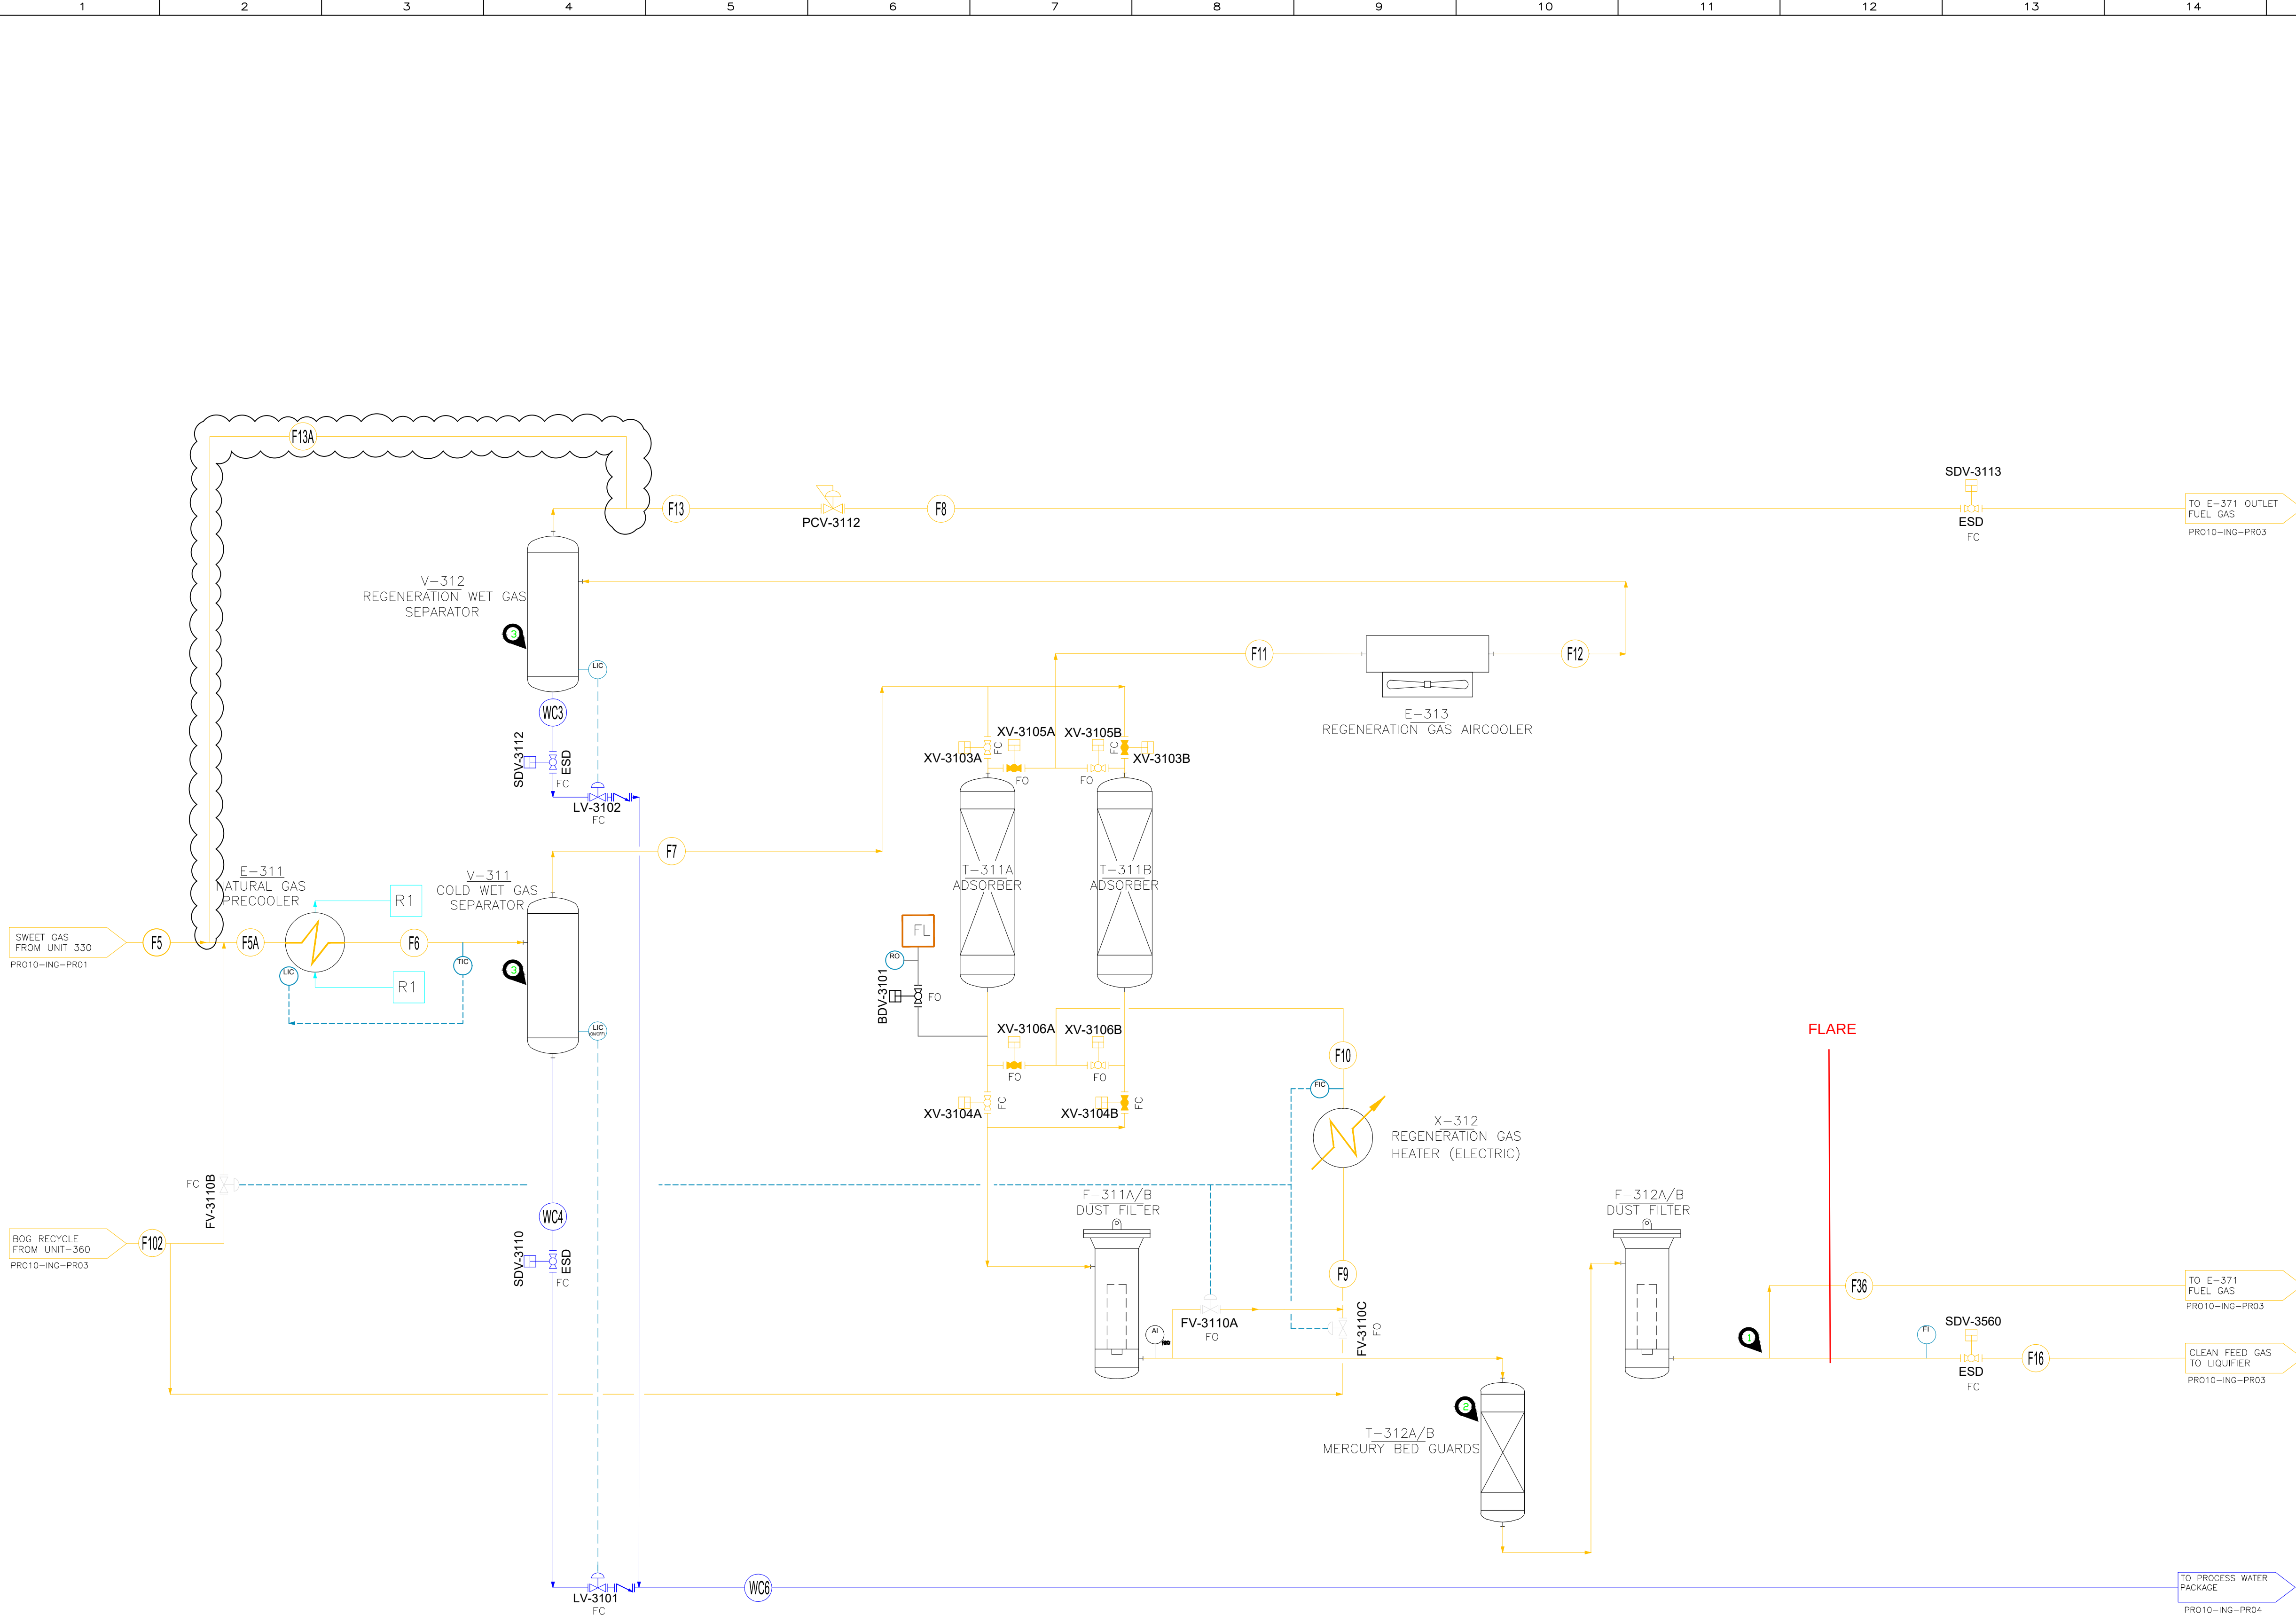

NOTES:

1- FUEL GAS MAKE UP LINE / ADDITIONAL MAKEUP LINE UPSTREAM THIS BRANCH WILL ALSO BE PROVIDED TO ALLOW POWER GENERATION INDEPENDENT STARTUP

2- NOT REGENERABLE MERCURY BED

3- SEPARATOR CAN BE VERTICAL/HORIZONTAL. TO BE DECIDED BY TG DURING SKID DETAILED ENGINEERING.


LEGEND:

FL TO FLARE SYSTEM

R1 R1 REFRIGERANT (AMMONIA)

FLUID LIST			
	CONDENSATES		PSV
	GAS		REFRIGERANT (AMMONIA)
	PROCESS WATER		INSTRUMENTAL LINE
	FRESH WATER		DIESEL
	AMINE		INERT GAS
	HOT OIL		MIXED REFRIGERANT
	LNG		

8	19 Dic 2024	ISSUED FOR APPROVAL	TAM (LD)	I.CAMPLONE	W. BOULALI	
7	6 Oct 2022	ISSUED FOR APPROVAL	TAM (LD)	I.CAMPLONE	W. BOULALI	
6	24 Jun 2022	ISSUED FOR APPROVAL	TAM (LD)	I.CAMPLONE	W. BOULALI	
5	25 Apr 2022	ISSUED FOR APPROVAL	TAM (LD)	I.CAMPLONE	W. BOULALI	
4	22 Feb 2022	PRELIMINARY ISSUE FOR TECHNICAL PROPOSED	M.FERRARINI	I.CAMPLONE	W. BOULALI	
3	15 Dec 2021	PRELIMINARY ISSUE FOR TECHNICAL PROPOSED	M.FERRARINI	I.CAMPLONE	W. BOULALI	
2	12 Mar 2021	PRELIMINARY ISSUE FOR TECHNICAL PROPOSED	M.FERRARINI	I.CAMPLONE	W. BOULALI	
1	24 Jan 2021	PRELIMINARY ISSUE FOR TECHNICAL PROPOSED	M.FERRARINI	I.CAMPLONE	W. BOULALI	
0	22 Sept 2020	PRELIMINARY ISSUE FOR TECHNICAL PROPOSED	M.FERRARINI	I.CAMPLONE	W. BOULALI	
Rev.	Date	Description	Draft	Check'd (ITF)	App'd (MSP)	SOUND ENERGY
SOUND ENERGY Customer: SOUND ENERGY I.M.S.P. MOROCCO Contractor: I.M.S.P. MOROCCO ITALFLUID Engineering: ITALFLUID TECHNICAL AMERICA Technology Vendor: TECHNICAL AMERICA INC MONTE SILVANO Offices: VIA VIVALDI,4 301 N Smith Avenue, 92880 Corona, California (USA) Ph:+1 951 272 9540 Regus Maroc Twin Center, Tour Ouest, Casablanca Tel: +39 085 4224374 fax +39 085 4220742 MONTE SILVANO (ITALY) Offices: VIA VIVALDI,4 301 N Smith Avenue, 92880 Corona, California (USA) Ph:+1 951 272 9540						
TITLE: LNG TENDRARA PLANT						
OBJECT: PROCESS FLOW DIAGRAM (GAS DEHYDRATION)						
TYPE	SCALE	DOCUMENTS ID	VENDOR DOC. CODE		SHEET/OF	
A1	N/A	PRO10-ING-PRO2	21044-PR-PFD-00001		1/1	

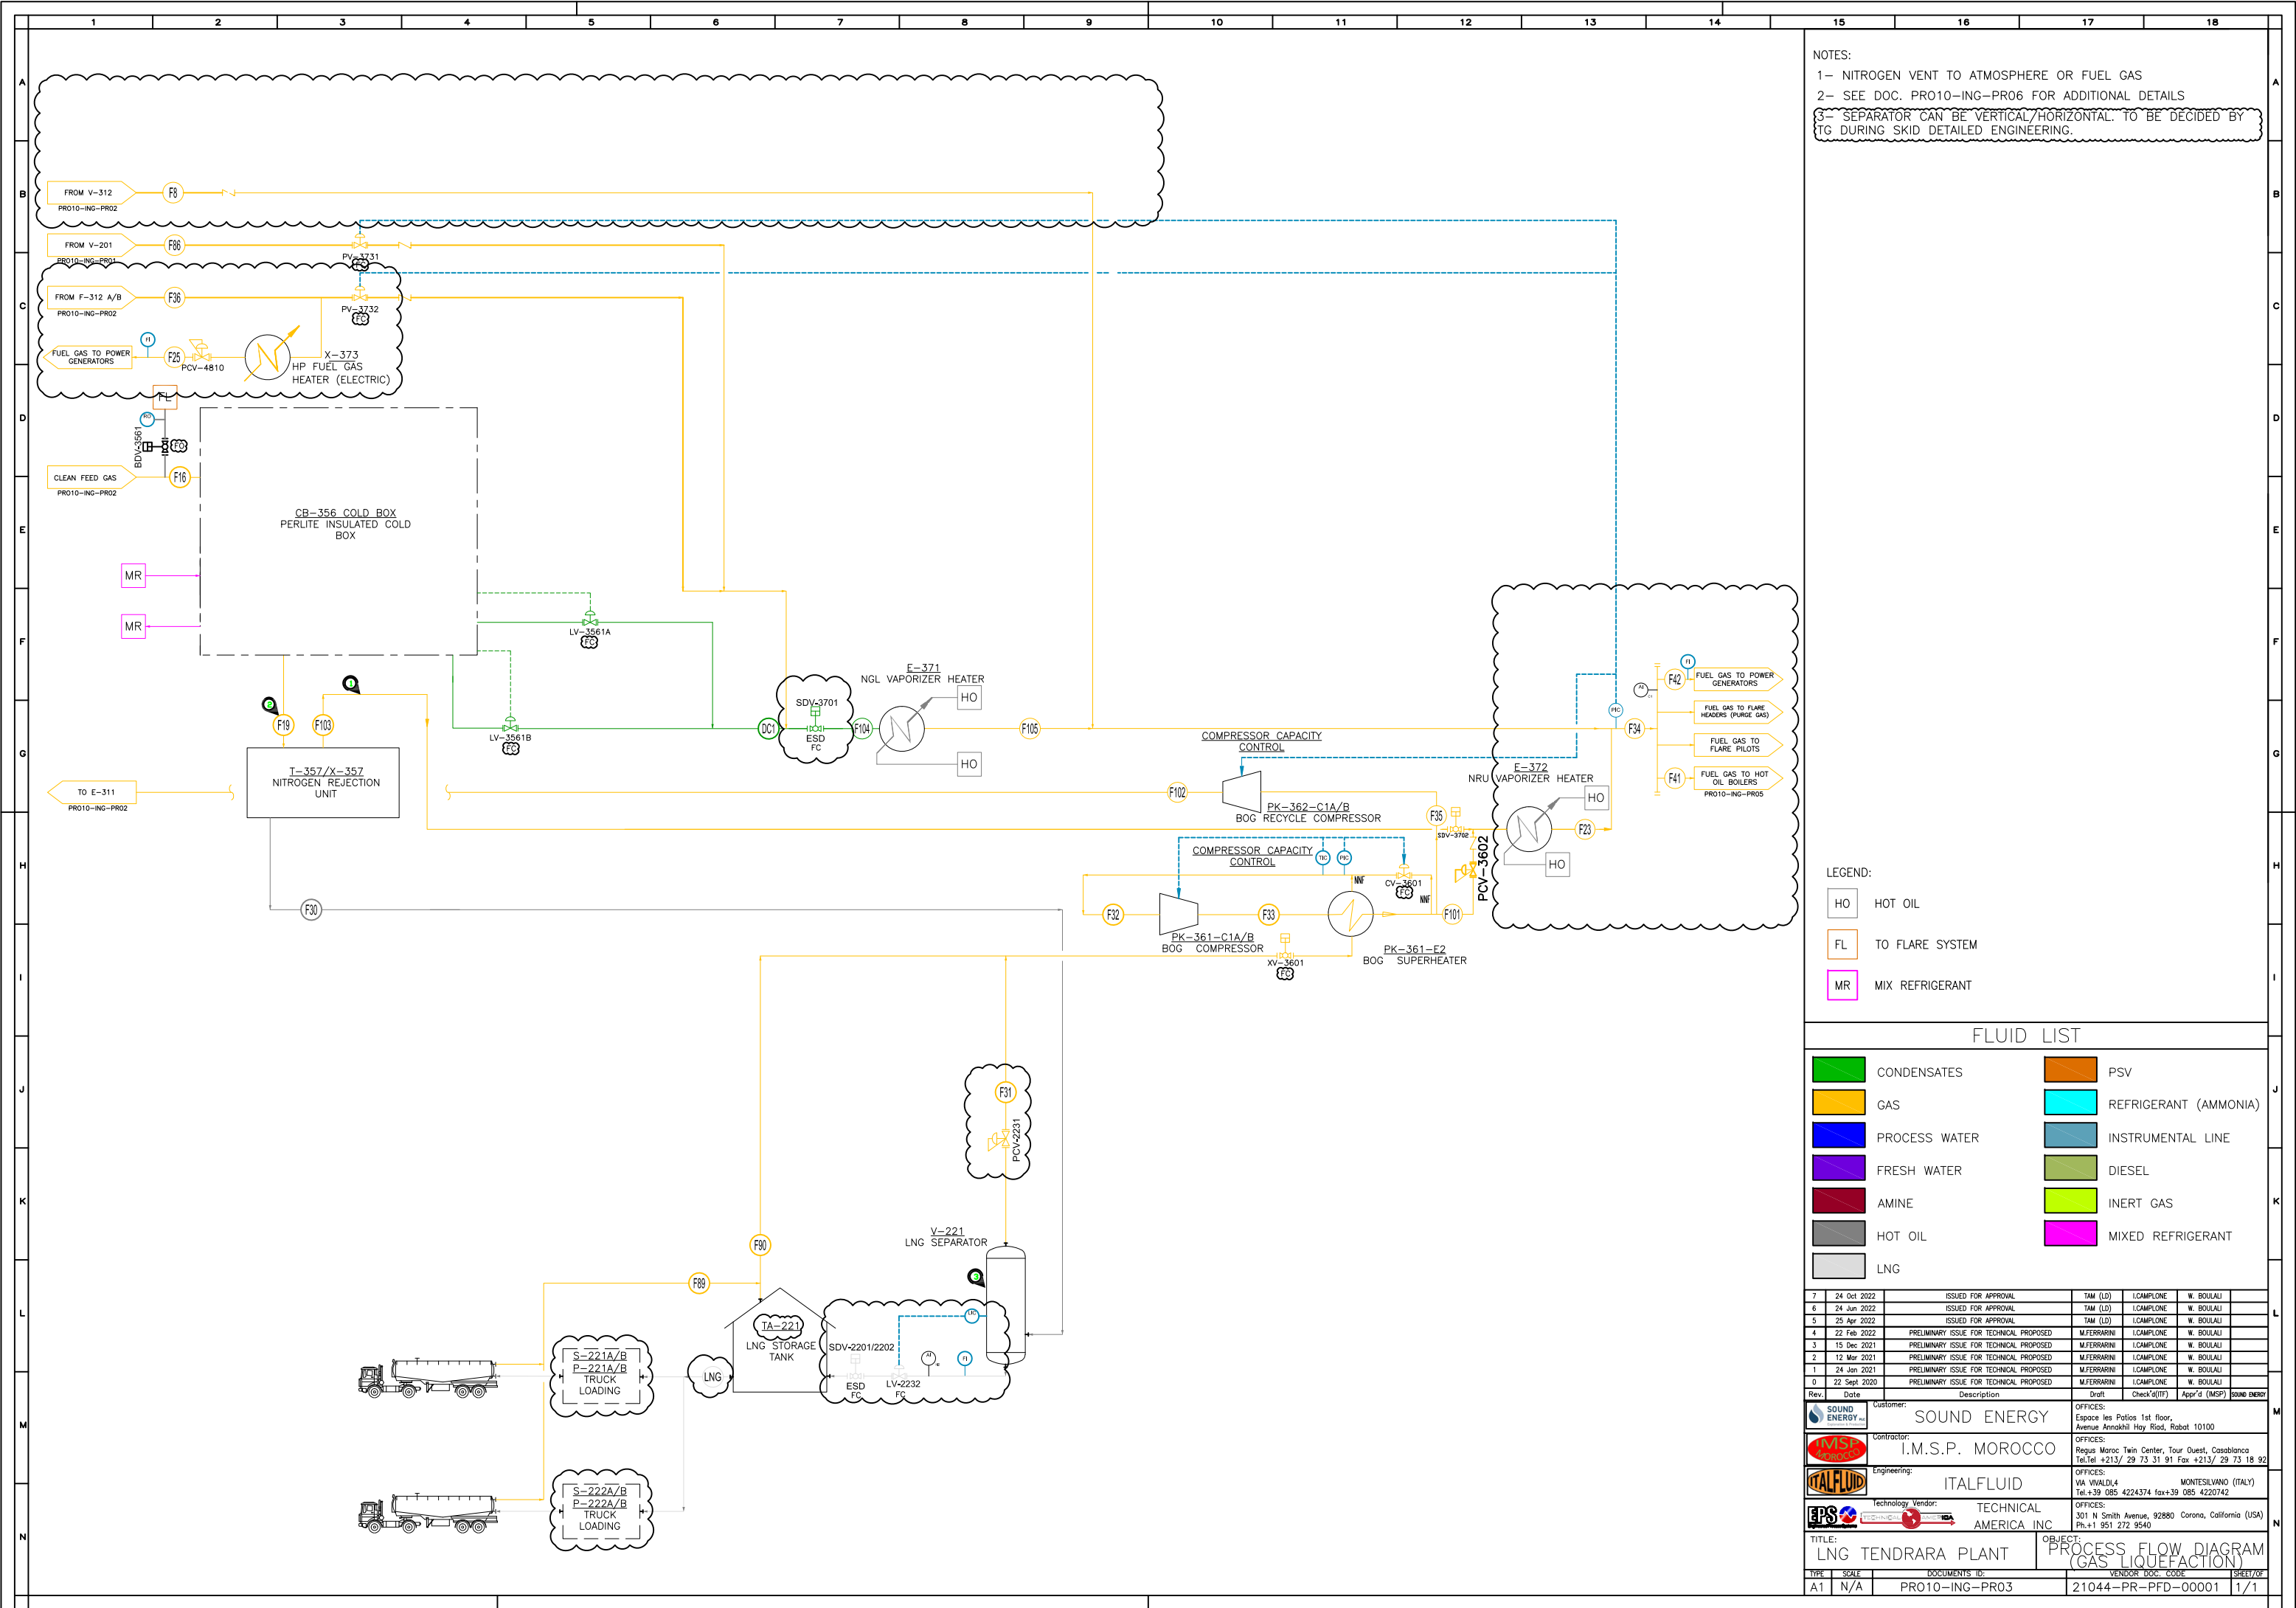

NOTES:
1- NITROGEN VENT TO ATMOSPHERE OR FUEL GAS
2- SEE DOC. PRO10-ING-PR06 FOR ADDITIONAL DETAILS
3- SEPARATOR CAN BE VERTICAL/HORIZONTAL. TO BE DECIDED BY TG DURING SKID DETAILED ENGINEERING.

- LEGEND:
- HO HOT OIL
 - FL TO FLARE SYSTEM
 - MR MIX REFRIGERANT

FLUID LIST			
	CONDENSATES		PSV
	GAS		REFRIGERANT (AMMONIA)
	PROCESS WATER		INSTRUMENTAL LINE
	FRESH WATER		DIESEL
	AMINE		INERT GAS
	HOT OIL		MIXED REFRIGERANT
	LNG		

7	24 Oct 2022	ISSUED FOR APPROVAL	TAM (LD)	LCAMPLONE	W. BOULAL	
6	24 Jun 2022	ISSUED FOR APPROVAL	TAM (LD)	LCAMPLONE	W. BOULAL	
5	25 Apr 2022	ISSUED FOR APPROVAL	TAM (LD)	LCAMPLONE	W. BOULAL	
4	22 Feb 2022	PRELIMINARY ISSUE FOR TECHNICAL PROPOSED	M.FERRARINI	LCAMPLONE	W. BOULAL	
3	15 Dec 2021	PRELIMINARY ISSUE FOR TECHNICAL PROPOSED	M.FERRARINI	LCAMPLONE	W. BOULAL	
2	12 Mar 2021	PRELIMINARY ISSUE FOR TECHNICAL PROPOSED	M.FERRARINI	LCAMPLONE	W. BOULAL	
1	24 Jun 2021	PRELIMINARY ISSUE FOR TECHNICAL PROPOSED	M.FERRARINI	LCAMPLONE	W. BOULAL	
0	22 Sep 2020	PRELIMINARY ISSUE FOR TECHNICAL PROPOSED	M.FERRARINI	LCAMPLONE	W. BOULAL	
Rev.	Date	Description	Draft	Check'd (ITF)	App'd (MSP)	SOUND ENERGY
Customer: SOUND ENERGY			OFFICES: Espace les Patios 1st floor, Avenue Annakhlil Hay Road, Rabat 10100			
Contractor: I.M.S.P. MOROCCO			OFFICES: Regus Maroc Twin Center, Tour Ouest, Casablanca Tel.+39 085 4224374 Fax+39 085 4220742			
Engineering: ITALFLUID			OFFICES: VIA VIVALDI,4 MONTE SILVANO (ITALY) Tel.+39 085 4224374 fax+39 085 4220742			
Technology Vendor: TECHNICAL AMERICA INC.			OFFICES: 301 N Smith Avenue, 92880 Corona, California (USA) Ph.+1 951 272 9540			
TITLE: LNG TENDRARA PLANT			OBJECT: PROCESS FLOW DIAGRAM (GAS LIQUEFACTION)			
TYPE	SCALE	DOCUMENTS ID:	VENDOR DOC. CODE		SHEET/OF	
A1	N/A	PRO10-ING-PR03	21044-PR-PFD-00001		1/1	